

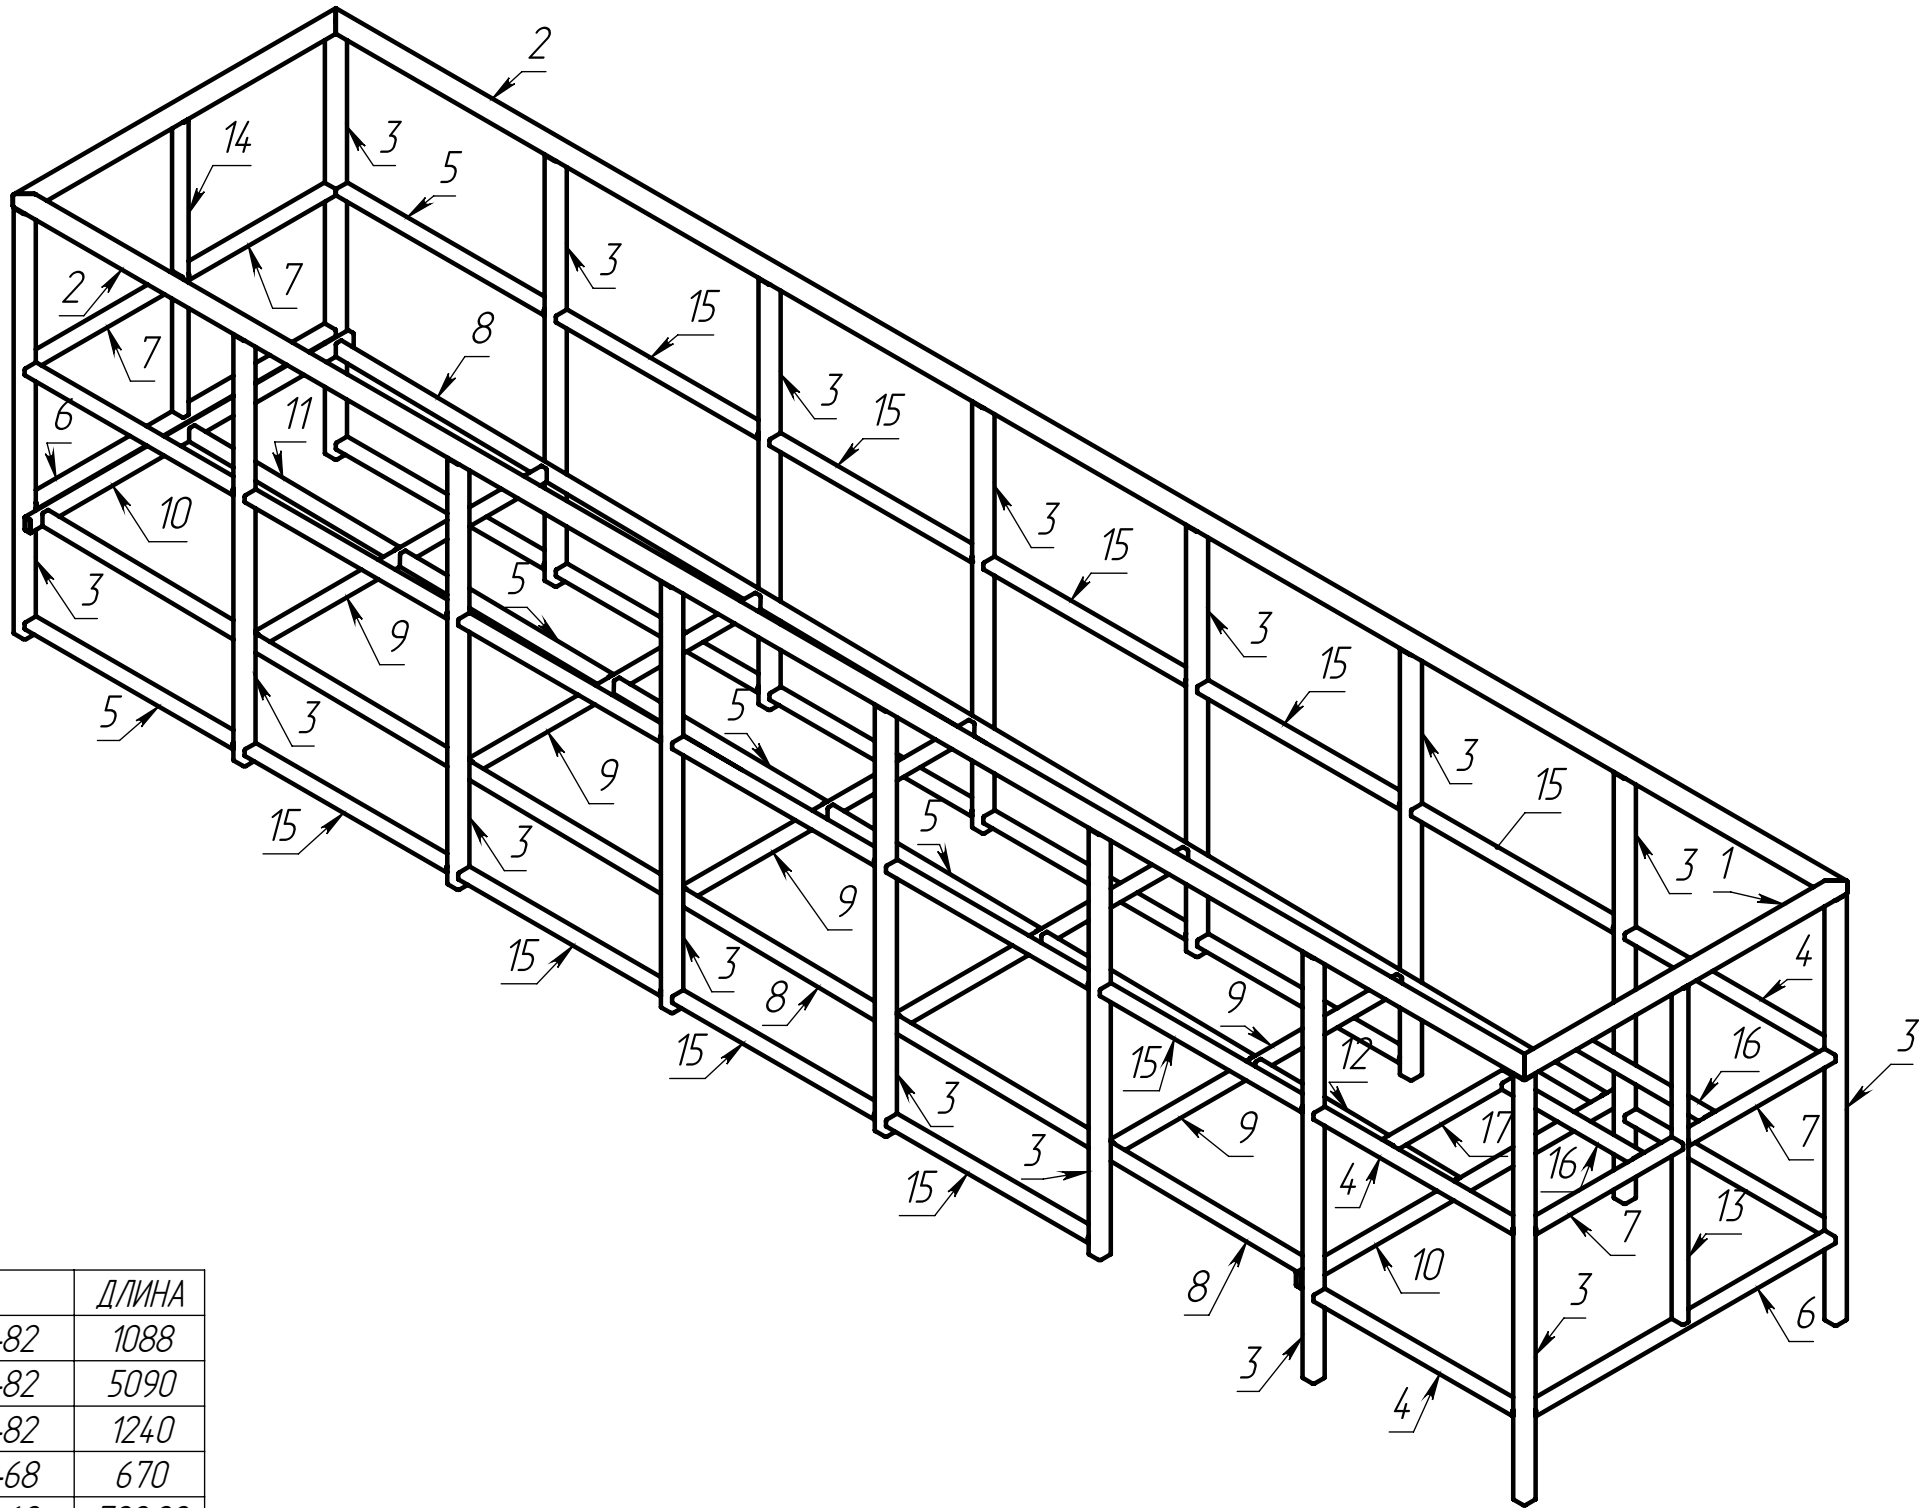


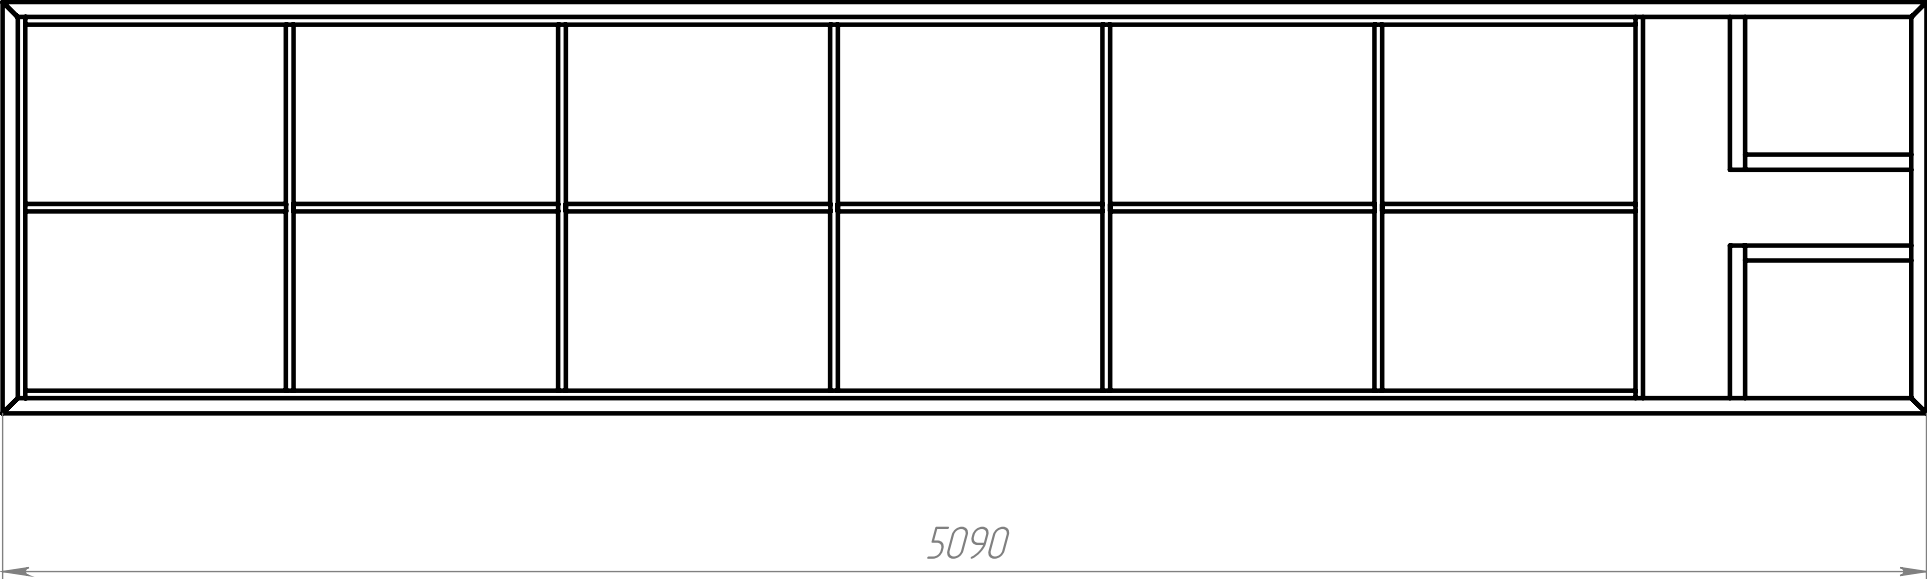

Позиция	Количество	Наименование	ДЛИНА
1	2	Труба 40 X 40 X 3 ГОСТ8639-82	1088
2	2	Труба 40 X 40 X 3 ГОСТ8639-82	5090
3	16	Труба 40 X 40 X 3 ГОСТ8639-82	1240
4	4	Труба 40 X 20 X 2 ГОСТ8645-68	670
5	8	Труба 40 X 20 X 2 ГОСТ8645-68	700.08
6	2	Труба 40 X 20 X 2 ГОСТ8645-68	1008
7	4	Труба 40 X 20 X 2 ГОСТ8645-68	494
8	2	Труба 40 X 20 X 2 ГОСТ8645-68	4261.04
9	5	Труба 40 X 20 X 2 ГОСТ8645-68	968
10	2	Труба 40 X 20 X 2 ГОСТ8645-68	1088
11	1	Труба 40 X 20 X 2 ГОСТ8645-68	690.07
12	1	Труба 40 X 20 X 2 ГОСТ8645-68	670.66
13	1	Труба 40 X 20 X 2 ГОСТ8645-68	980
14	1	Труба 40 X 20 X 2 ГОСТ8645-68	860
15	18	Труба 40 X 20 X 2 ГОСТ8645-68	680
16	2	Труба 40 X 20 X 2 ГОСТ8645-68	440
17	2	Труба 40 X 20 X 2 ГОСТ8645-68	404

					ВРХИ.ХХХХХХ.ХХ.ХХ.ХХ		
					Рама		
					Лит. Масса Масштаб		
					187.89 1:18		
					Лист 1 Листов 9		
					Сварная конструкция AISI 304		
Изм.	Лист	№ докум.	Подп.	Дата			
Разраб.							
Пров.							
Т. контр.							
Н. контр.							
Утв.							


ВРХИ.ХХХХХХ.ХХ.ХХ.ХХ

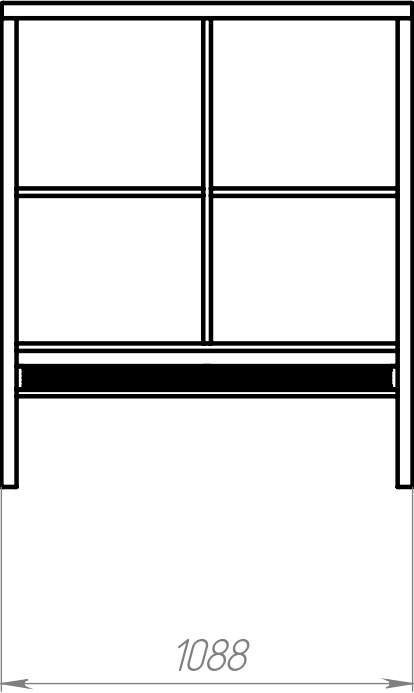

					ВРХИ.ХХХХХХ.ХХ.ХХ.ХХ						
					Рама	Лит.			Масса	Масштаб	
Изм.	Лист	№ докум.	Подп.	Дата					187.89	1:20	
Разраб.											
Пров.											
Т. контр.						Лист 2			Листов 9		
					Сварная конструкция AISI 304						
Н. контр.											
Утв.											

BPXN.XXXXXX.XX.XX.XX


Расположение элементов длинных сторон рамы

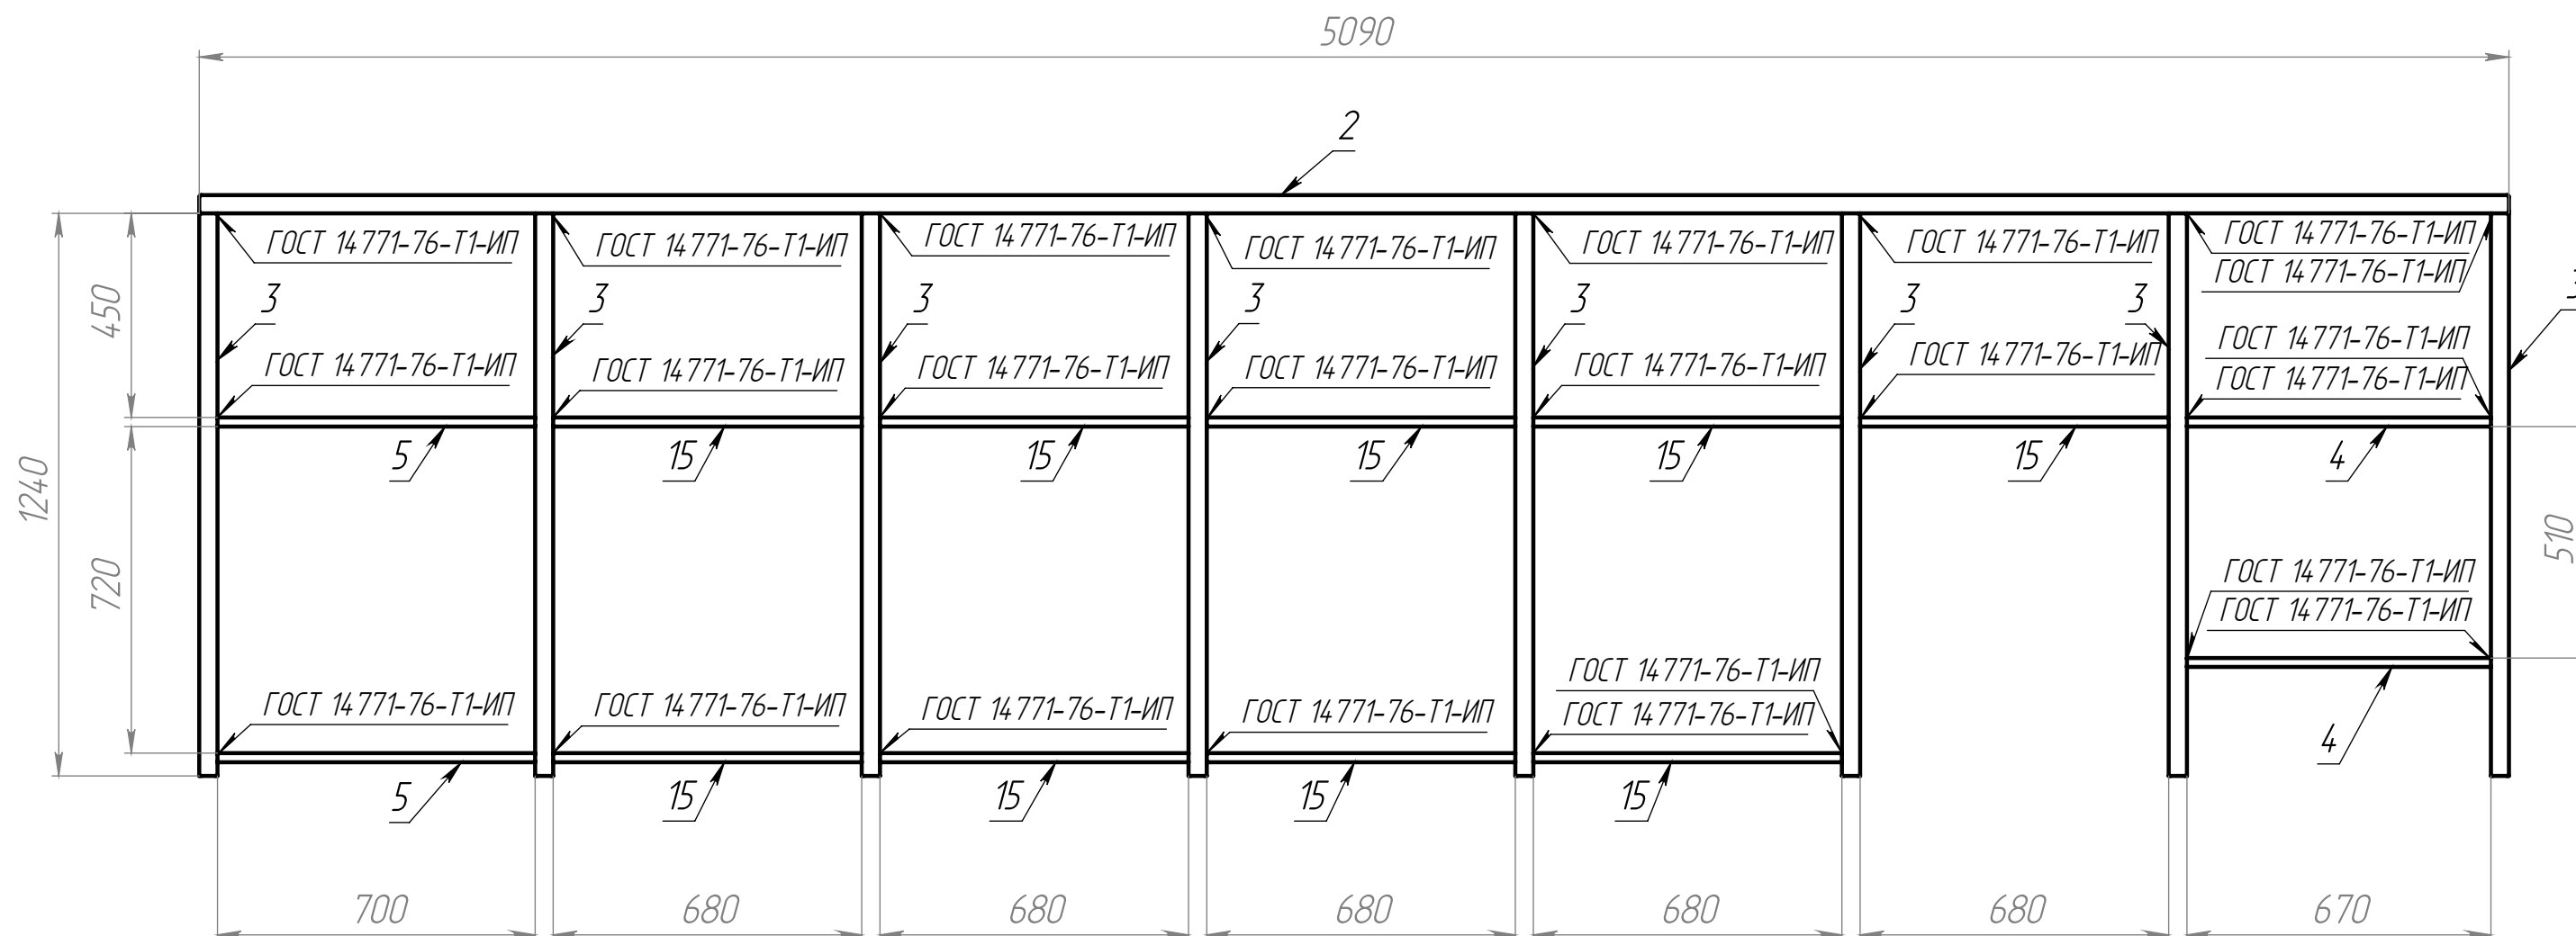

					ВРХИ.ХХХХХХ.ХХ.ХХ.ХХ						
					Рама	Лит.			Масса	Масштаб	
Изм.	Лист	№ докум.	Подп.	Дата					187.89	1:15	
Разраб.											
Пров.											
Т. контр.						Лист 3			Листов 9		
					Сварная конструкция AISI 304						
Н. контр.											
Утв.											

BPXN.XXXXXX.XX.XX.XX

Вид слева

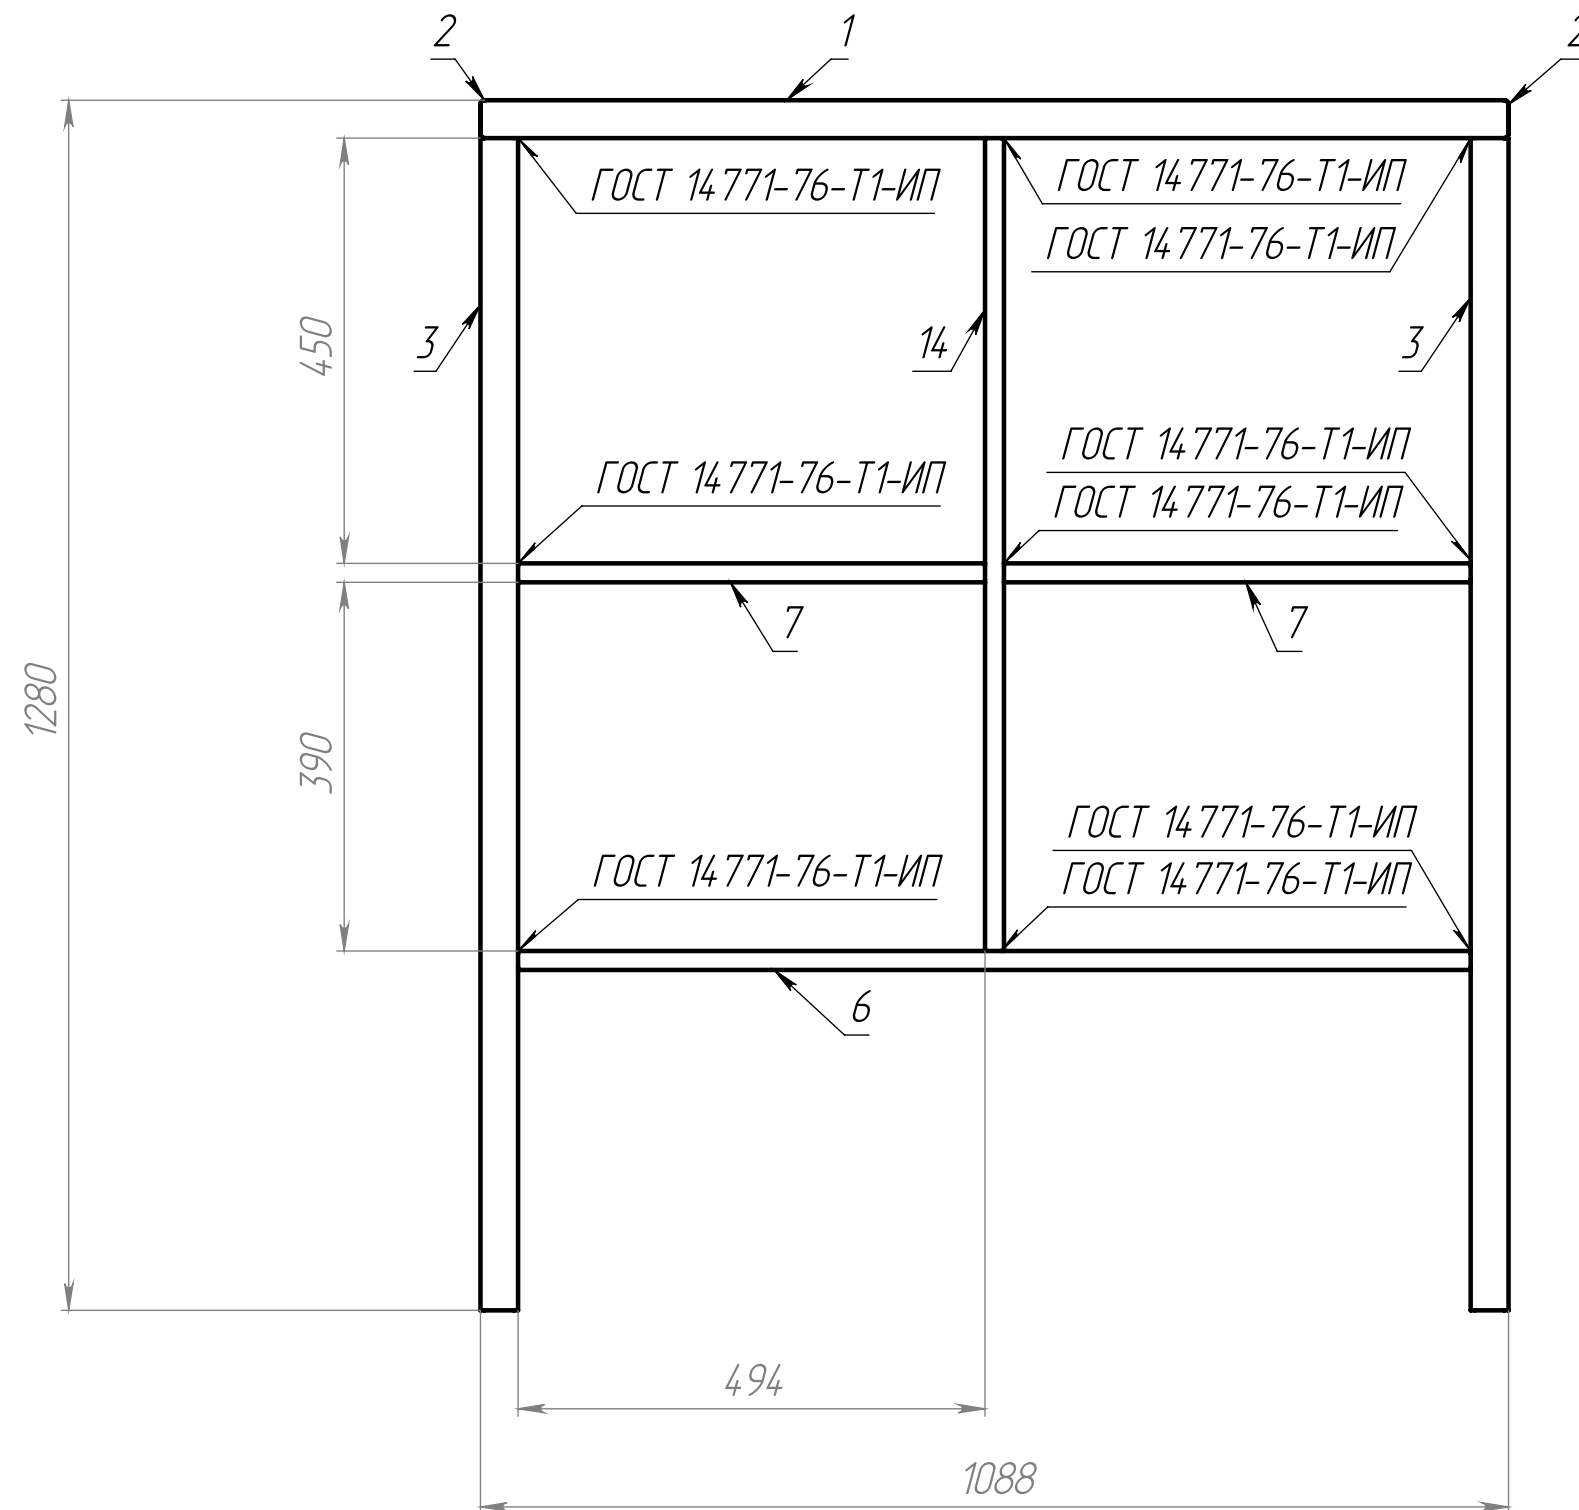

					<i>ВРХИ.ХХХХХХ.ХХ.ХХ.ХХ</i>				
					<i>Рама</i>	<i>Лит.</i>		<i>Масса</i>	<i>Масштаб</i>
<i>Изм.</i>	<i>Лист</i>	<i>№ докум.</i>	<i>Подп.</i>	<i>Дата</i>				<i>187.89</i>	<i>1:8</i>
<i>Разраб.</i>									
<i>Пров.</i>									
<i>Т. контр.</i>						<i>Лист 4</i>		<i>Листов 9</i>	
					<u>Сварная конструкция</u> <u>AISI 304</u>				
<i>Н. контр.</i>									
<i>Утв.</i>									

ВРХИ.ХХХХХХ.ХХ.ХХ.ХХ

Перв. примен.

Справ. №

Подп. и дата


Инв. № дубл.

Взам. инв. №

Подп. и дата

Инв. № подл.

Вид справа

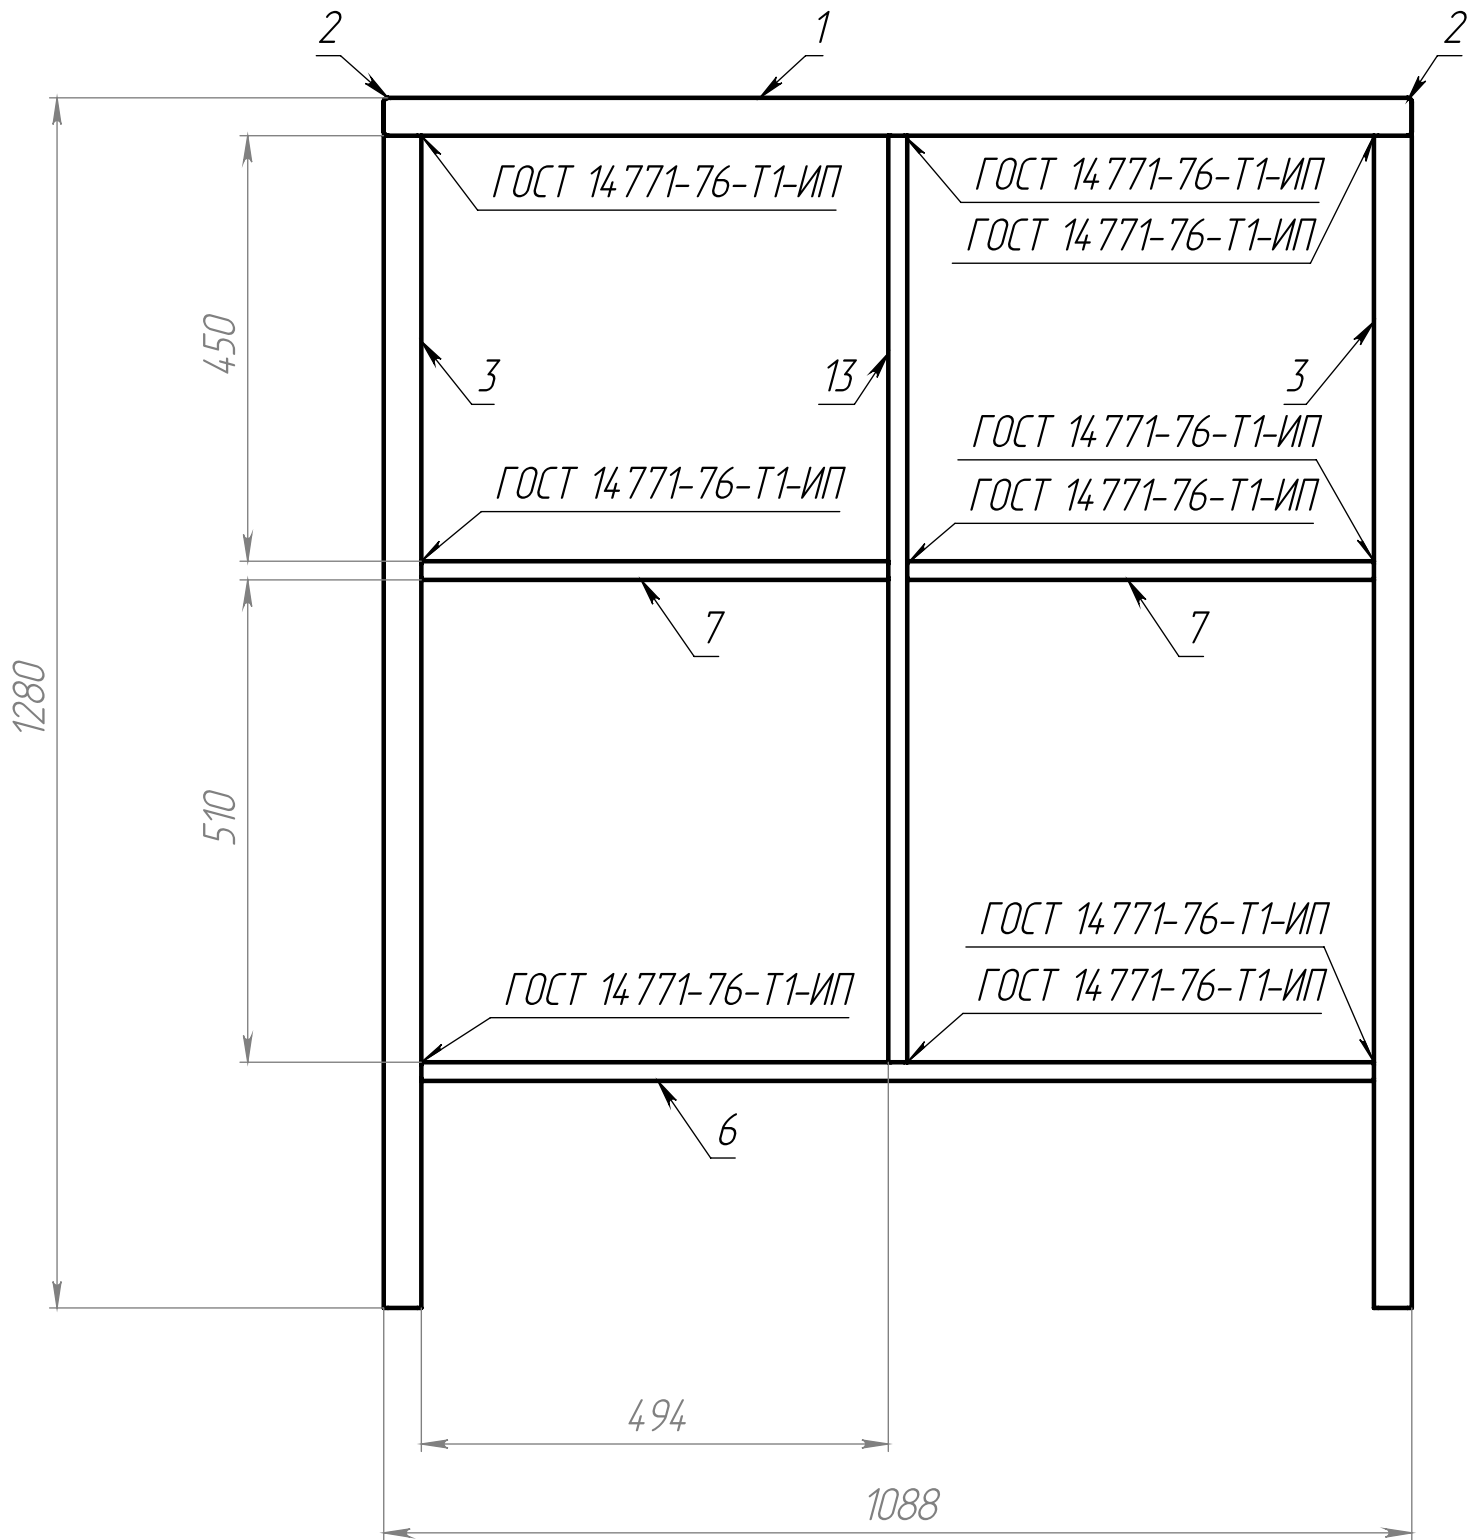

					ВРХИ.ХХХХХХ.ХХ.ХХ.ХХ						
					Рама	Лит.			Масса	Масштаб	
Изм.	Лист	№ докум.	Подп.	Дата					187.89	1:8	
Разраб.											
Пров.											
Т. контр.					Лист 5			Листов 9			
Н. контр.					Сварная конструкция		АISI 304				
Утв.											




2

1



BPXN.XXXXXX.XX.XX.XX

Расположение элементов дна



$A(1:10)$

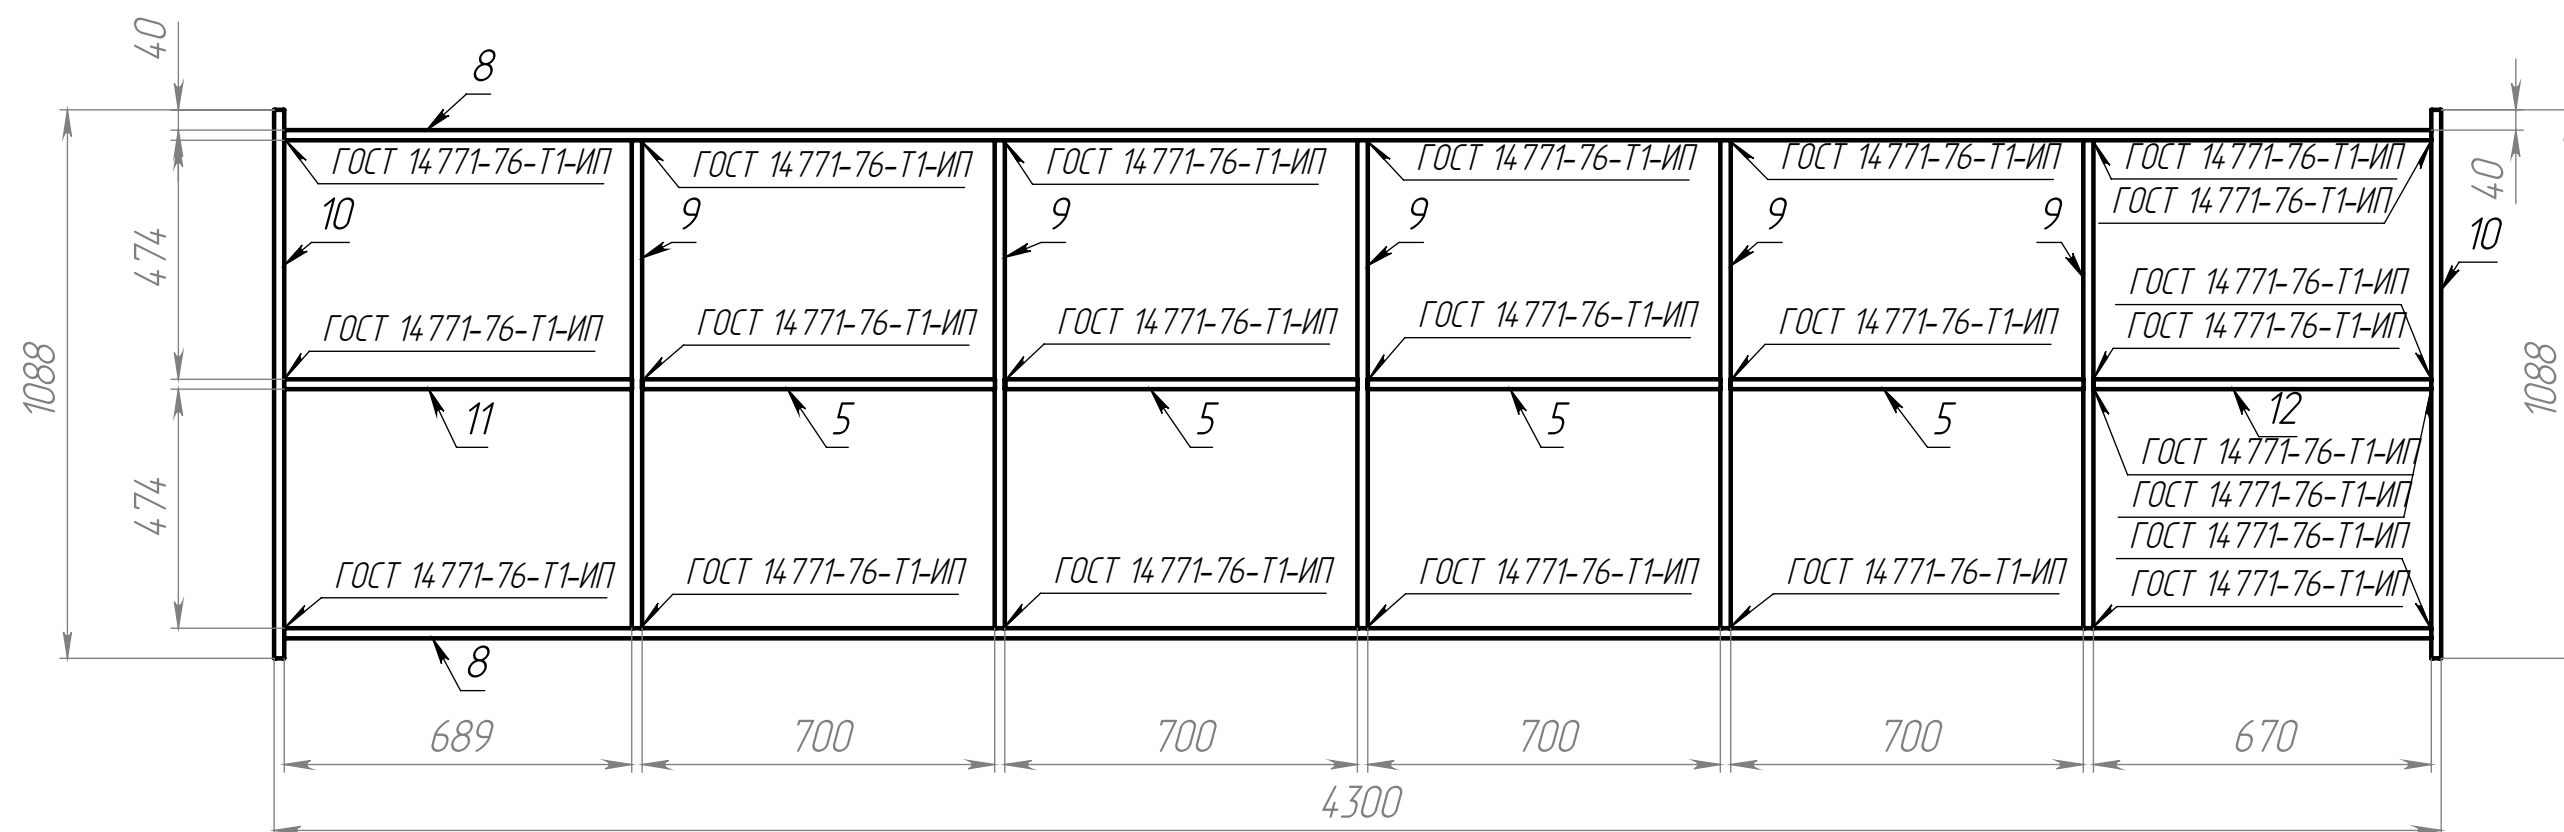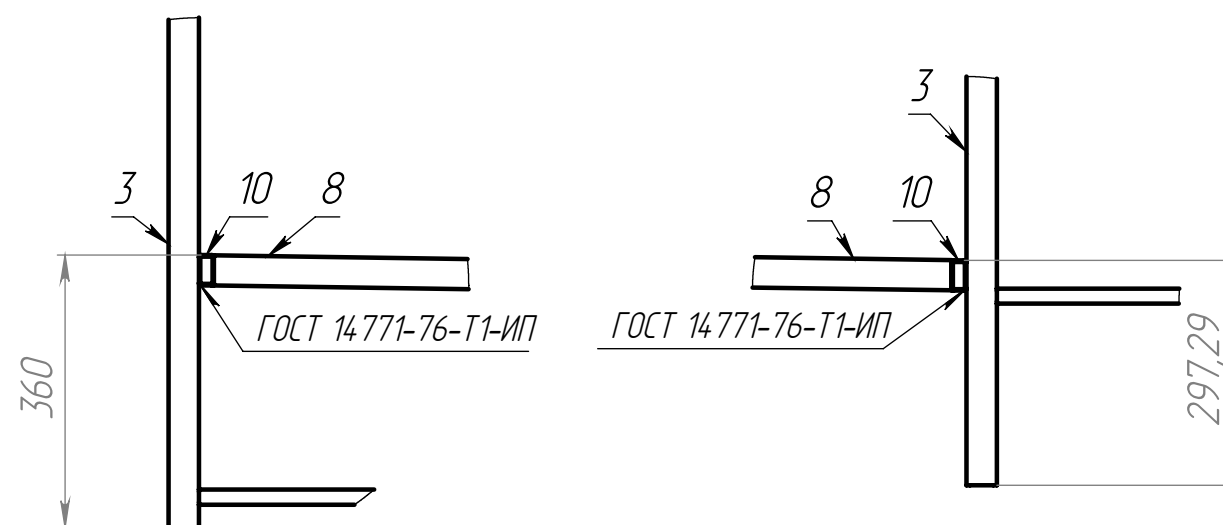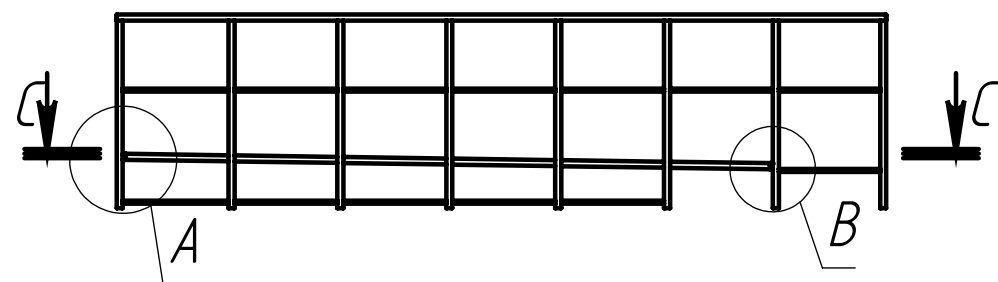 $B(1:10)$ 




$D (1 : 10)$

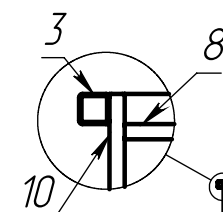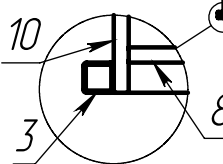 $E(1:10)$ 

C-C (1:50)

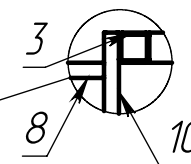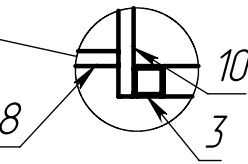 $F(1:10)$  $G(1:10)$ 

					ВРХИ.ХХХХХХ.ХХ.ХХ.ХХ				
					Рама	Лит.		Масса	Масштаб
Изм.	Лист	№ докум.	Подп.	Дата				187.89	1:15
Разраб.									
Пров.									
Т. контр.						Лист 6		Листов 9	
Н. контр.					Сварная конструкция		AISI 304		
Утв.									

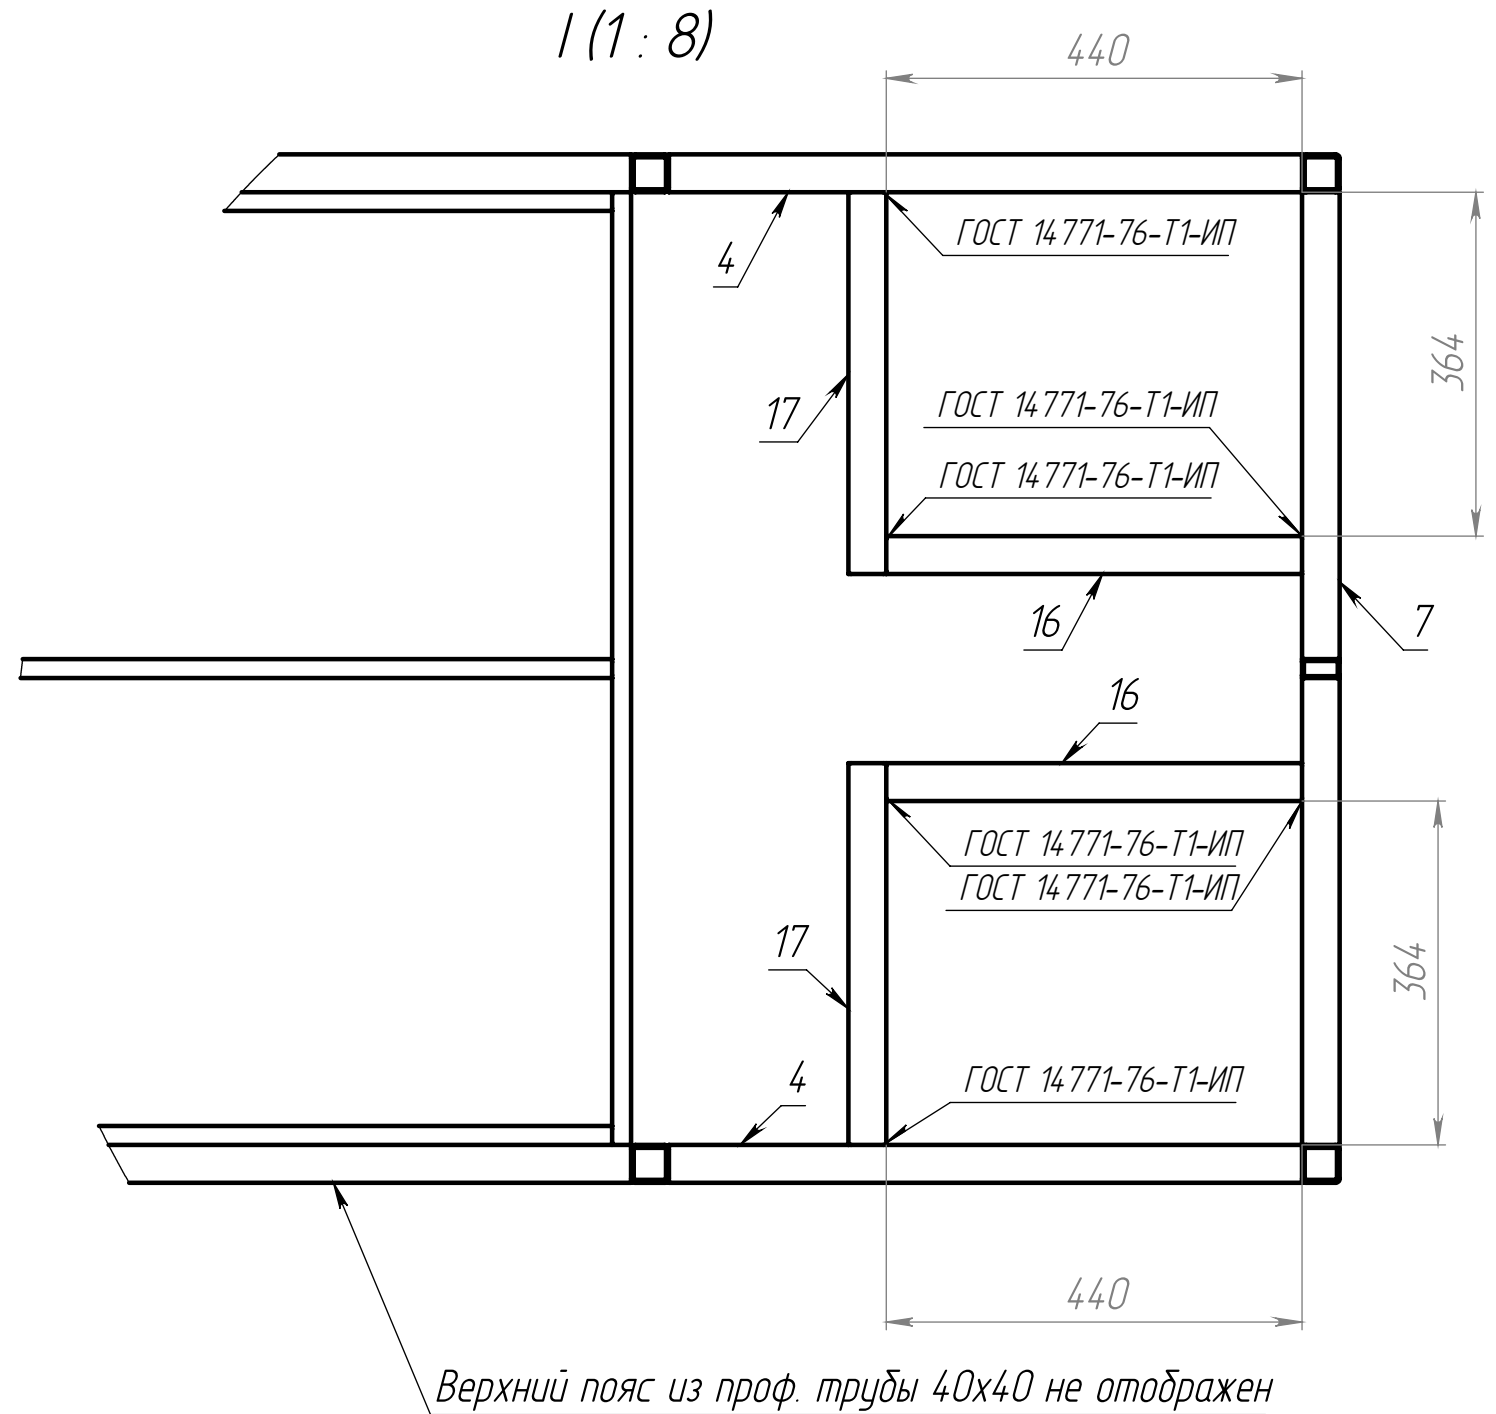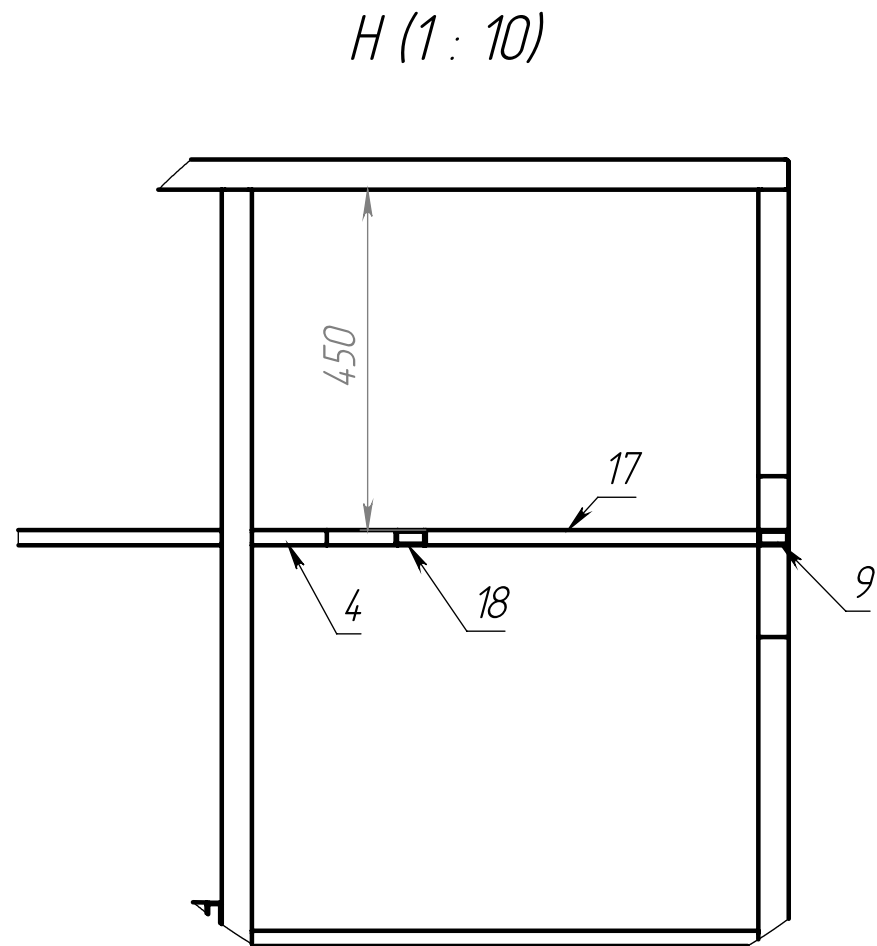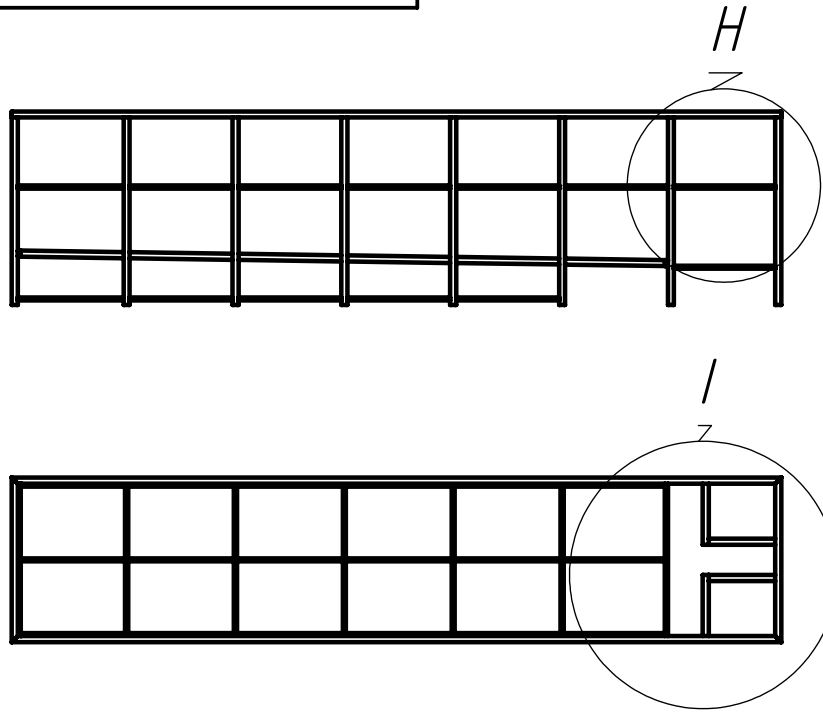

					ВРХИ.ХХХХХХ.ХХ.ХХ.ХХ						
					Рама	Лит.		Масса	Масштаб		
Изм.	Лист	№ докум.	Подп.	Дата					187.89	1:50	
Разраб.											
Пров.											
Т. контр.					Лист 7		Листов 9				
					Сварная конструкция	АISI 304					
Н. контр.											
Утв.											

