

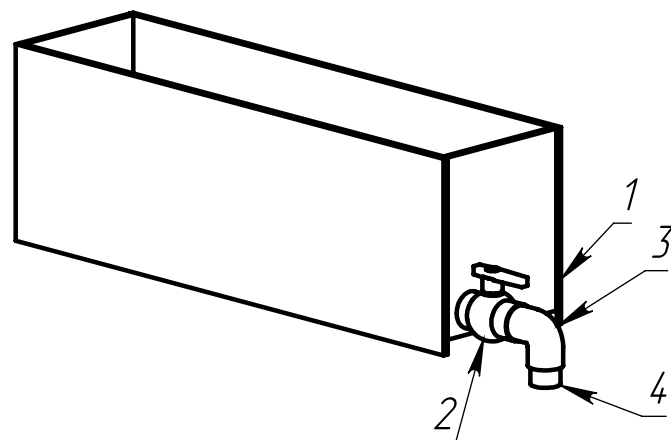
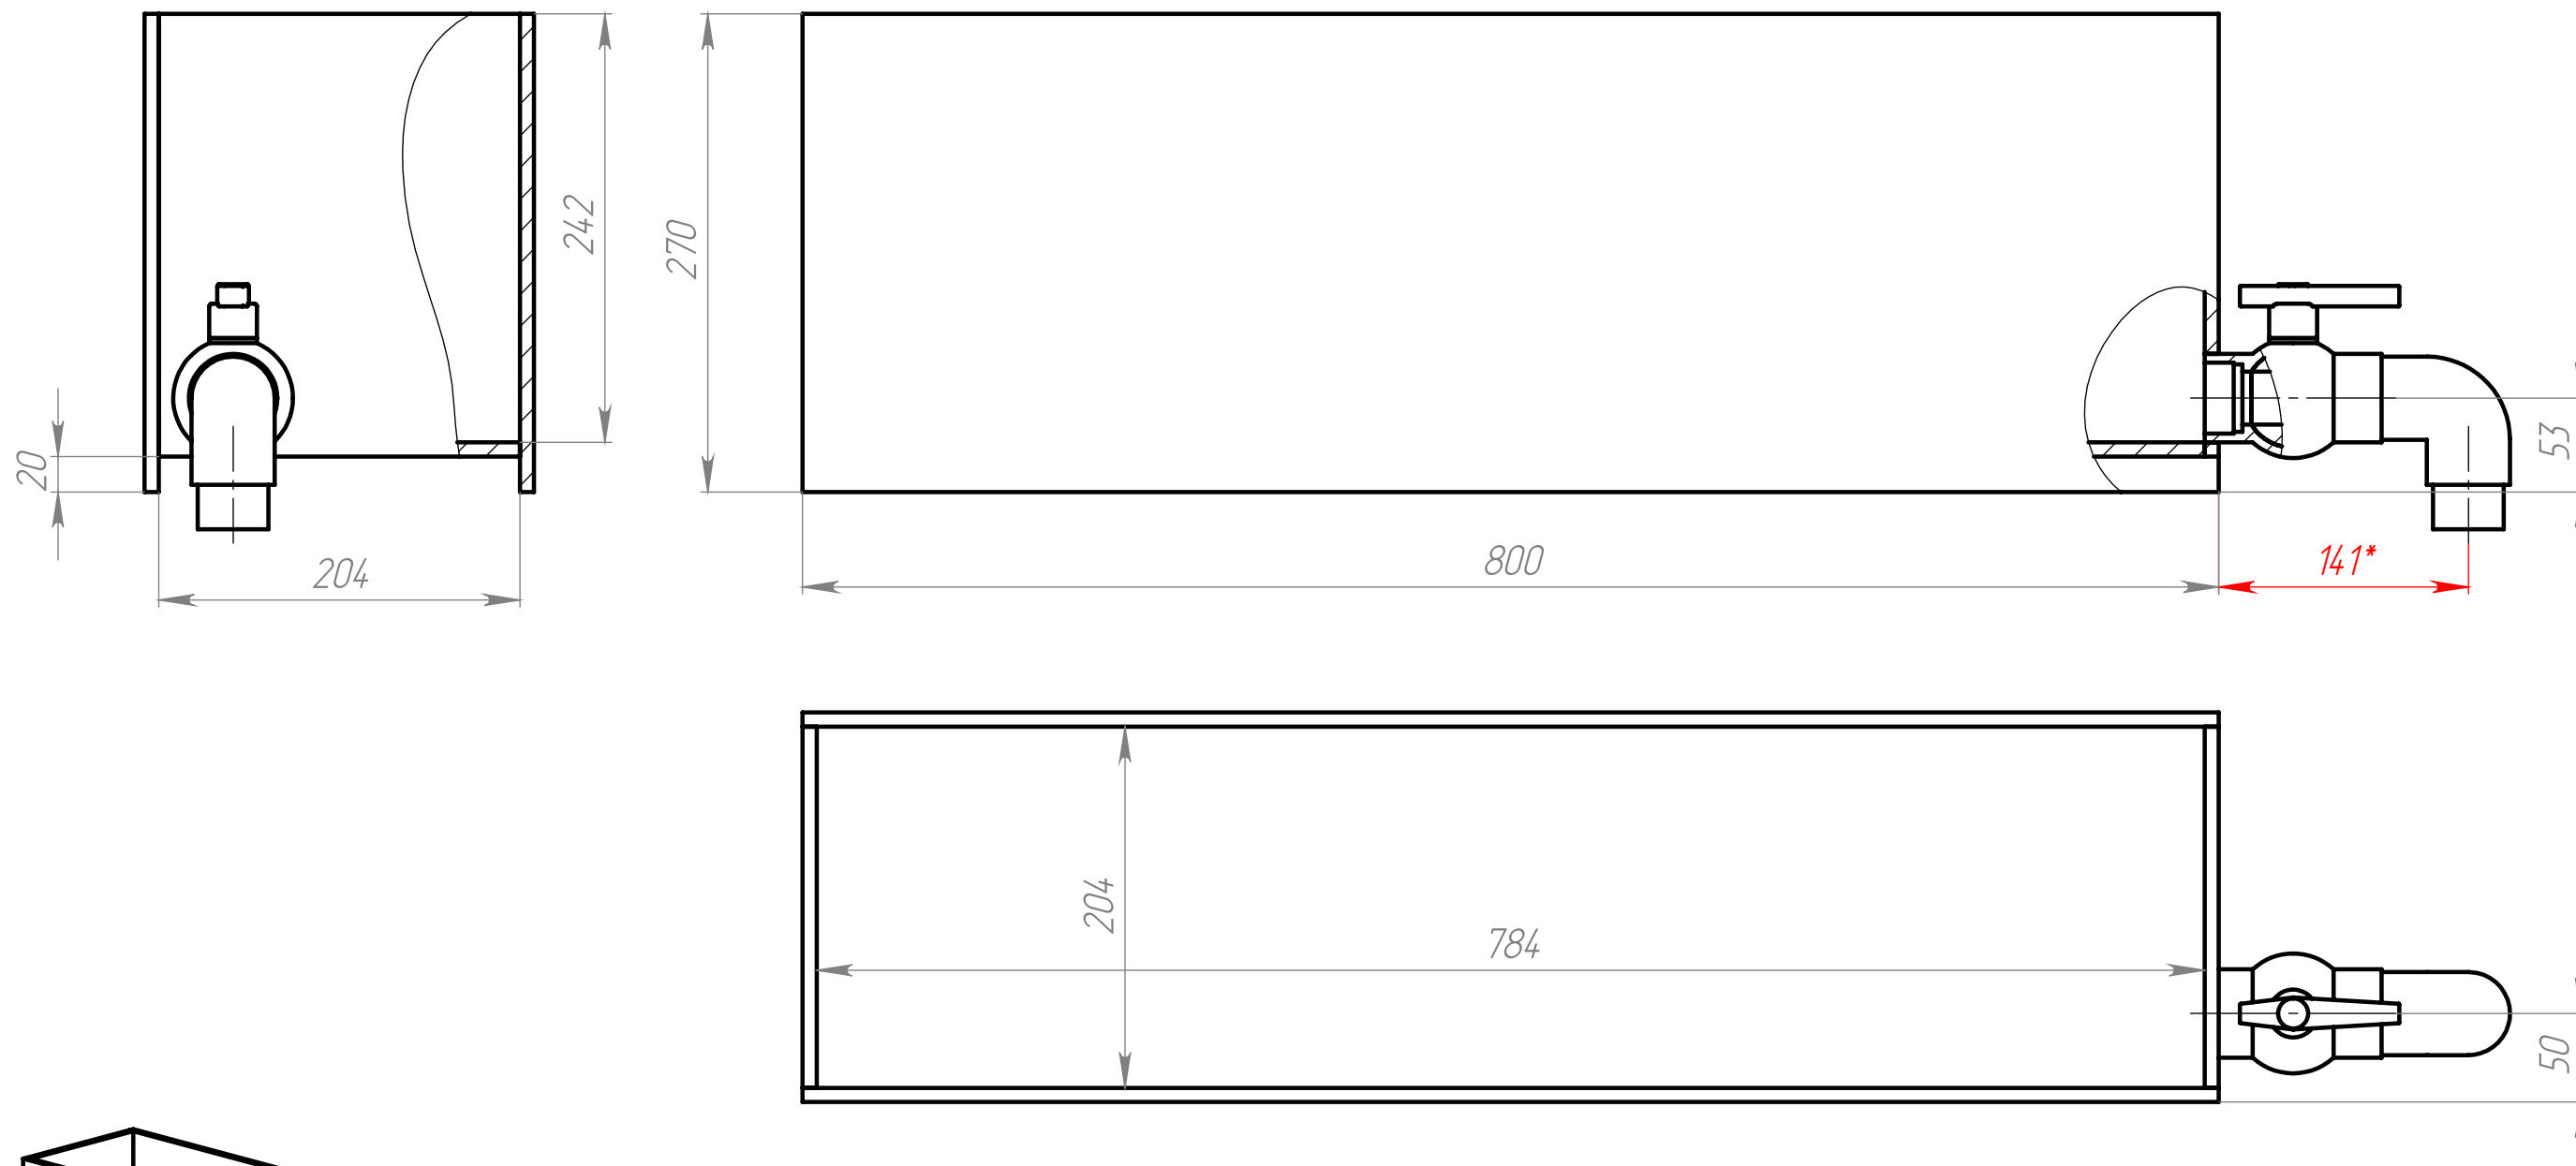
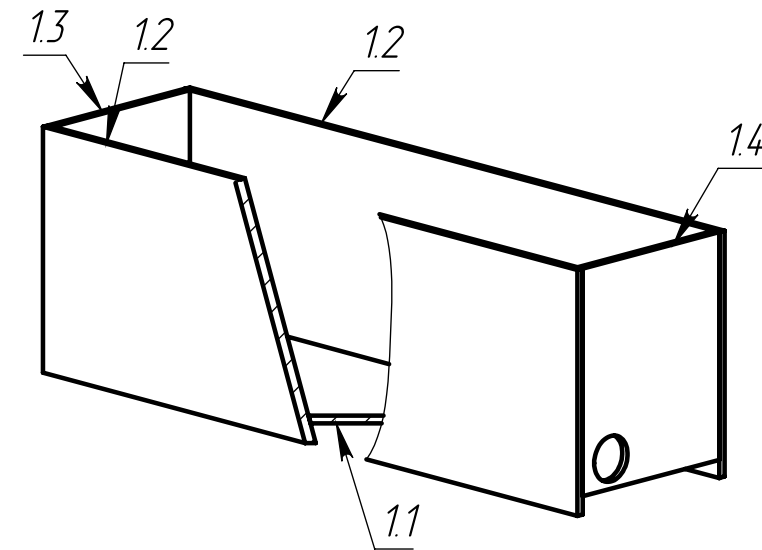


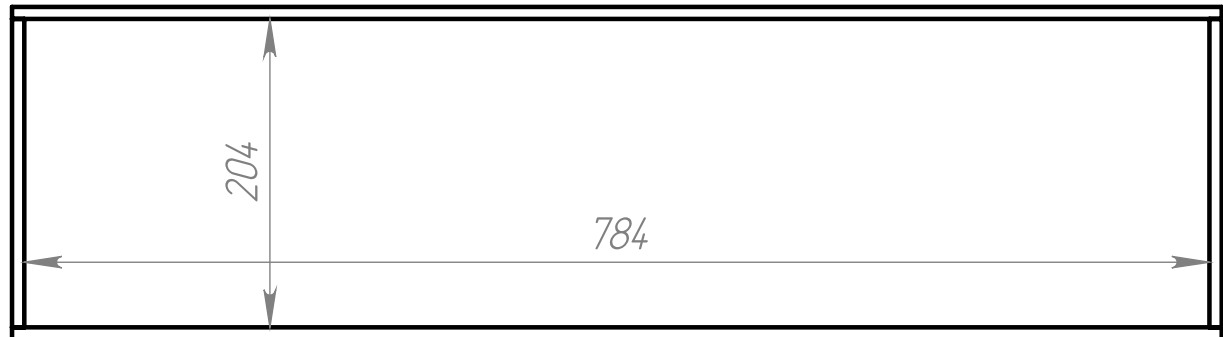

* – Размер указан ориентировочный. Фактический размер зависит от геометрических размеров применяемых фитингов.

Поз.	ОБОЗНАЧЕНИЕ	ОПИСАНИЕ	К-ВО
1	Каркас ванны для диз. раствора	ВРХИ.ВМ93.01.92.32 СБ	1
2	Кран D40	Стандартное изделие	1
3	ПП Угол 90 D40	Стандартное изделие	1
4	ПП Труба D40 L1	Стандартное изделие	1

					ВРХИ.ВМ.92.01.00.32 СБ							
					Ванна для диз. раствора			Лит.	Масса	Масштаб		
Изм.	Лист	№ докум.	Подп.	Дата							5.59	1:4
Разраб.												
Пров.												
Т. контр.												
								Лист 1	Листов 10			
					Сборочная единица							
Н. контр.												
Утв.												

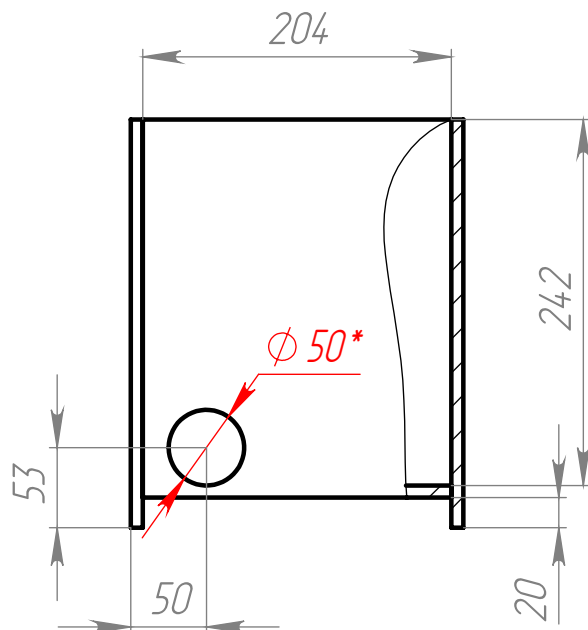

Поз.	ОБОЗНАЧЕНИЕ	ОПИСАНИЕ	К-ВО
1	Каркас ванны для диз. раствора	ВРХИ.ВМ93.01.92.32 СБ	1
1.1	Дно	ВРХИ.ВМ93.04.92.32	1
1.2	Длинная стенка	ВРХИ.ВМ93.01.92.32	2
1.3	Глухой торец	ВРХИ.ВМ93.02.92.32	1
1.4	Сливной торец	ВРХИ.ВМ93.03.92.32	1


					ВРХИ.ВМ93.01.92.32 СБ								
					Каркас ванны для диз. раствора				Лит.		Масса	Масштаб	
Изм.	Лист	№ докум.	Подп.	Дата								4.98	1:5
Разраб.													
Пров.													
Т. контр.									Лист 2		Листов 10		
					Сборочная единица								
Н. контр.													
Утв.													

* - Диаметр отверстия ориентировочный. Фактический диаметр зависит от наружного диаметра применяемого фитинга.

BPXN.BM01.01.93.32 C5

Перв. примен.

Справ. №

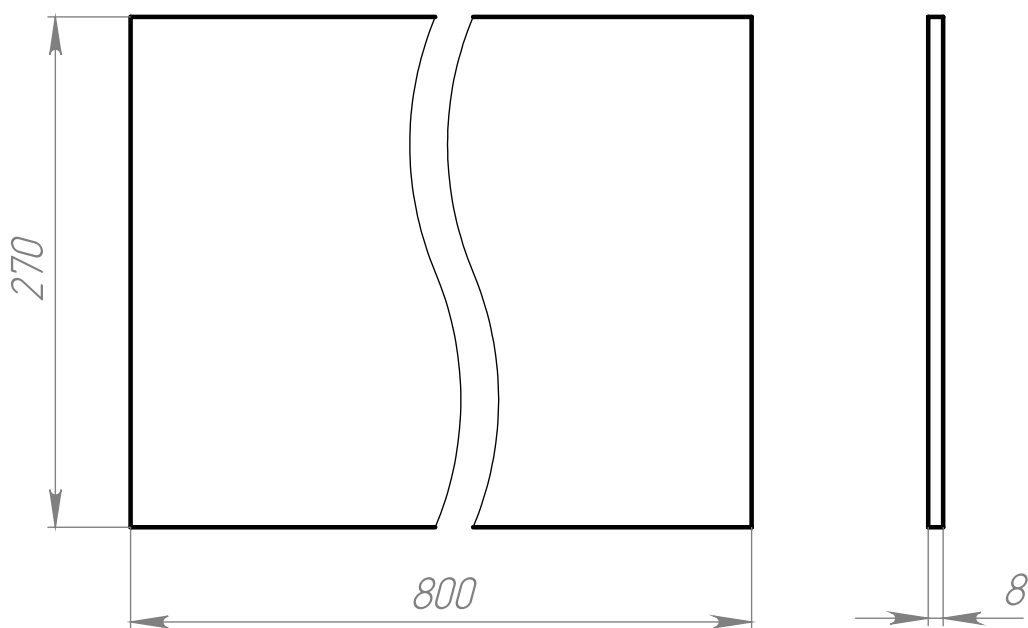

Инв. № подл.	Подп. и дата	Взам. инв. №	Инв. № дубл.	Подп. и дата

<i>Изм.</i>	<i>Лист</i>	<i>№ докум.</i>	<i>Подп.</i>	<i>Дата</i>
<i>Разраб.</i>				
<i>Пров.</i>				
<i>Т. контр.</i>				
<i>Н. контр.</i>				
<i>Утв.</i>				

ВРХИ.ВМ01.01.93.32 СБ

Длинная стенка

Лист Полипропилен ГОСТ 26996-86

Лит.			Масса	Масштаб
			1.56	1:4
Лист 3			Листов 10	

ВРХИ.ВМ02.01.93.32 СБ

Глухой торец

Лист Полипропилен ГОСТ 26996-86

Лит.

Macca

Масштаб

0.37

1:4

Лист 4

Листов 10

Справ. №

Подп. и дата

ИНВ. № дубл.

Взам. инв. №

Подп. и дата


ИНВ. № подл.

Изм.	Лист	№ докум.	Подп.	Дата
Разраб.				
Пров.				
Т. контр.				
Н. контр.				
Утв.				

Справ. №	Перв. примен.
----------	---------------

Инв. № подл.	Подп. и дата	Взам. инв. №	Инв. № дубл.	Подп. и дата
--------------	--------------	--------------	--------------	--------------

ВРХИ.ВМ03.01.93.32 СБ

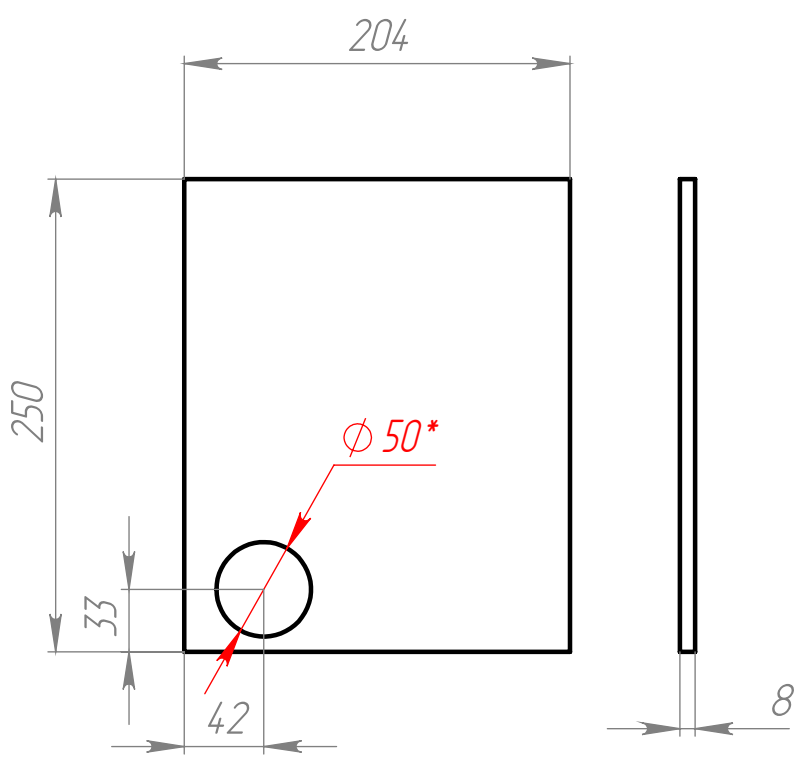


* - Диаметр отверстия ориентировочный. Фактический диаметр зависит от наружного диаметра применяемого фитинга.

ВРХИ.ВМ03.01.93.32 СБ					Лит.			Масса	Масштаб
Изм.	Лист	№ докум.	Подп.	Дата	Сливной торец			0.35	1:4
Разраб.									
Пров.									
Т. контр.								Лист 5	Листов 10
Н. контр.					Лист Полипропилен ГОСТ 26996-86				
Утв.									

Справ. №	Перв. примен.
----------	---------------

Инв. № подл.	Подп. и дата	Взам. инв. №	Инв. № дубл.	Подп. и дата
--------------	--------------	--------------	--------------	--------------

ВРХИ.ВМ04.01.93.32 СБ

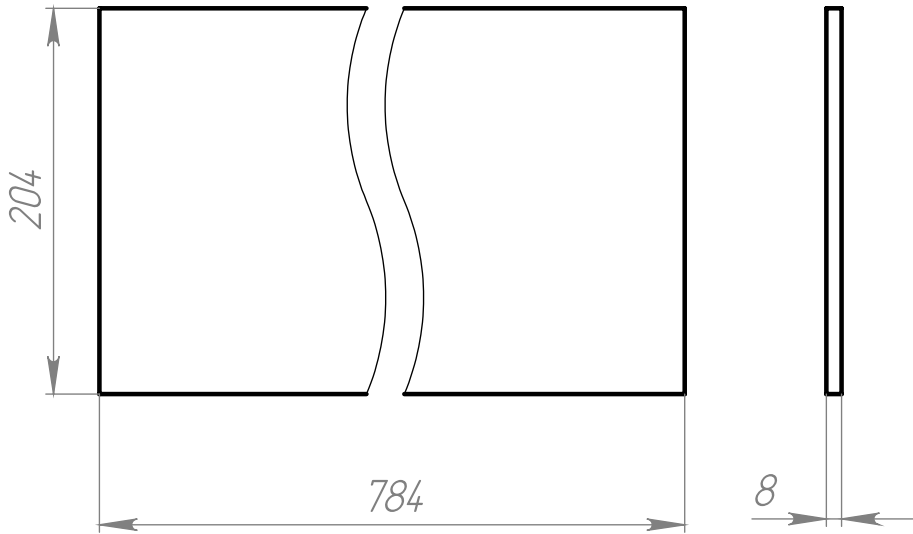

Изм.	Лист	№ докум.	Подп.	Дата
Разраб.				
Пров.				
Т. контр.				
Н. контр.				
Утв.				

ВРХИ.ВМ04.01.93.32 СБ

Дно

Лит.	Масса	Масштаб
	1.15	1:4
Лист 6	Листов 10	

Лист Полипропилен ГОСТ 26996-86

Перв. примен.

Справ. №

Подп. и дата

Инв. № дубл.

Взам. инв. №

Подп. и дата

Инв. № подл.

ВРХИ.ВМ80.01.00.32

Дополнения к конструкции мальковой ванны

Полка малая

250

75

Ø 64

Вырезать в детали "Полка малая" дополнительное отверстие. Диаметр отверстия указан ориентировочный. Фактический диаметр зависит от наружного диаметра раструбной части соединительной канализационной муфты D50.

Полка малая

Муфта D50

ПП угол и ПП труба не показаны

Припаять муфту D50 к полке.

1

1

1

1

1

1

1

Полка малая

Лит. 1.58

Масса 1.58

Масштаб 1:5

Лист 9

Листов 10

Лист Полипропилен ГОСТ 26996-86



1 Копировал

Формат А3

Файл: 92. Диз. ванна (ВРХИ.ВМ.92.01.00.32 СБ)

BPXN.BM.01.32 CB

Установка ванны для диз. раствора

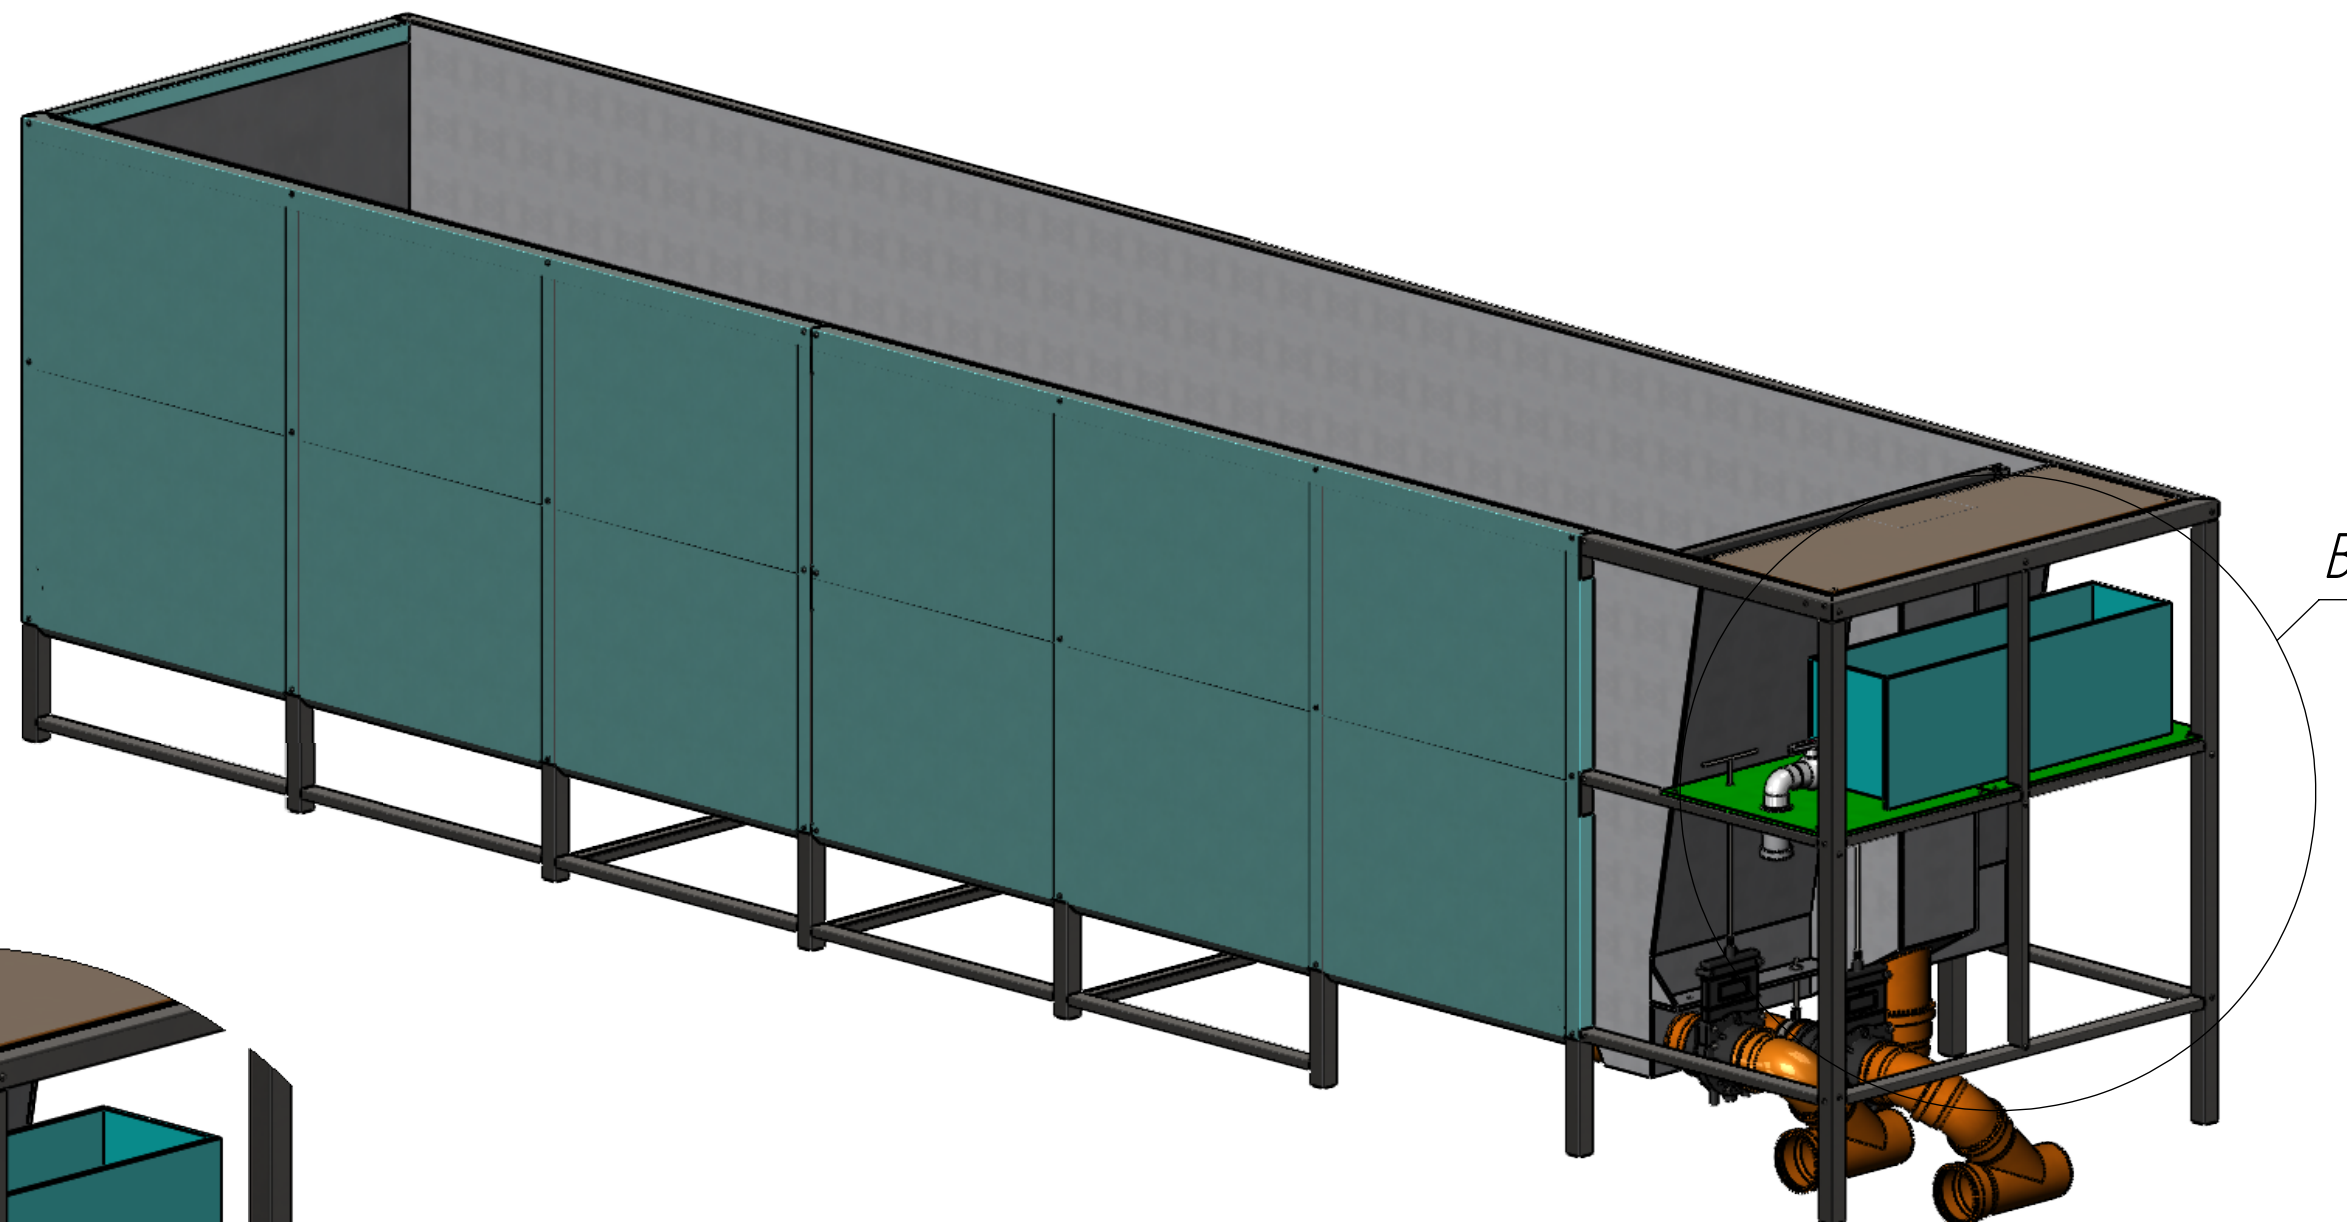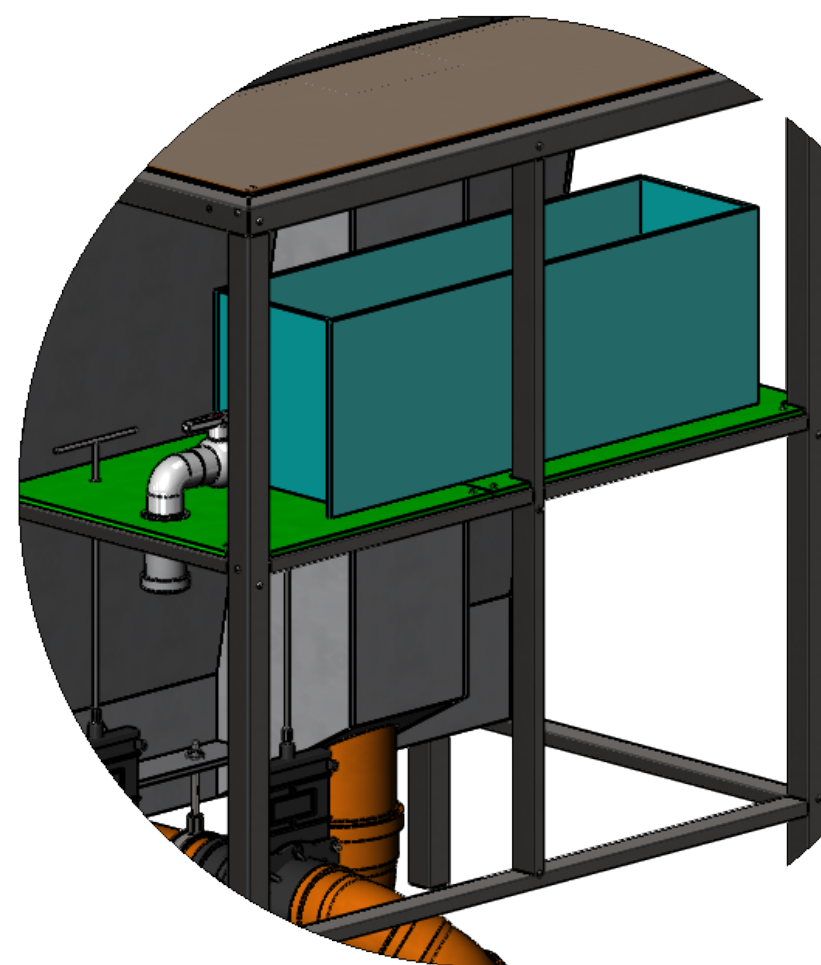 $B(1:10)$ 

					ВРХИ.ВМ.01.32 СБ				
					Ванна (прав. стена)	Лит.		Масса	Масштаб
Изм.	Лист	№ докум.	Подп.	Дата				400.96	1:15
Разраб.									
Пров.									
Т. контр.						Лист 10		Листов 10	
					Сборочная единица				
Н. контр.									
Утв.									