
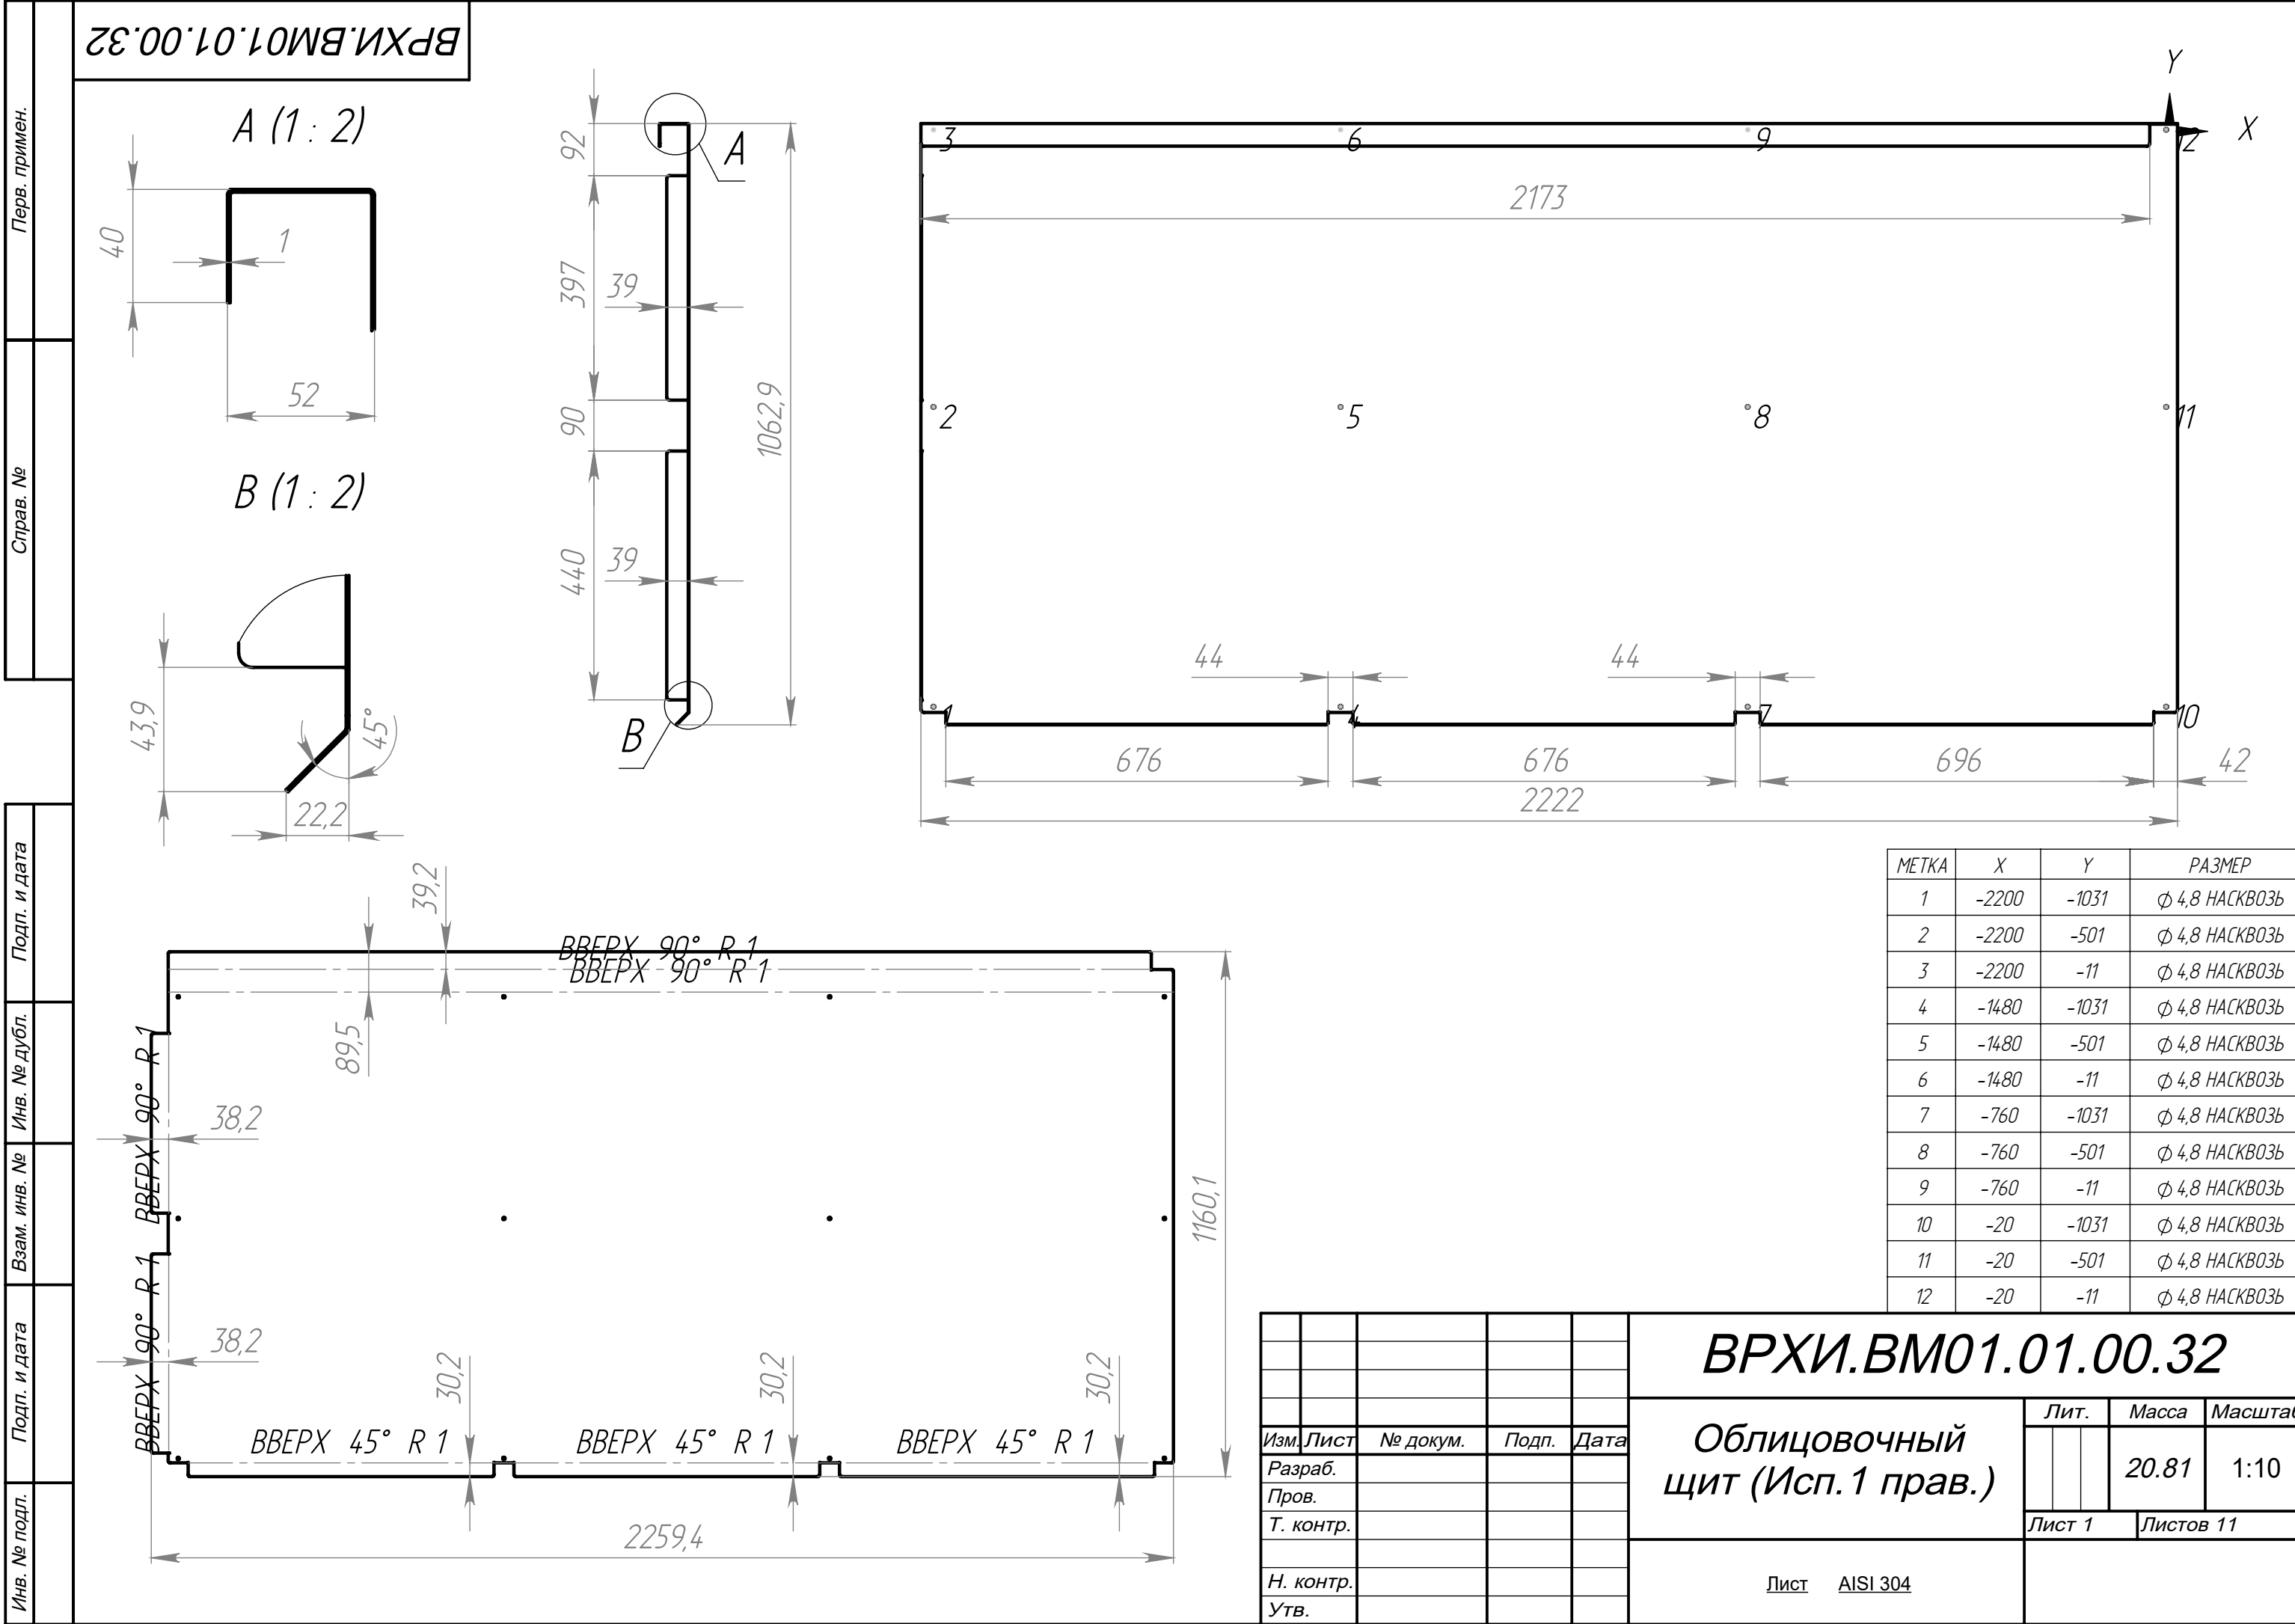
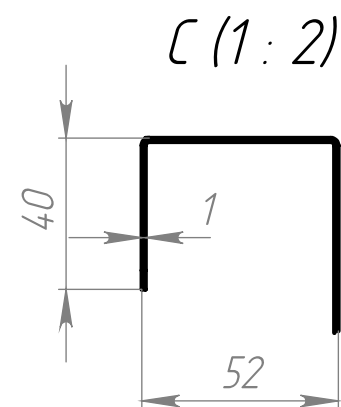
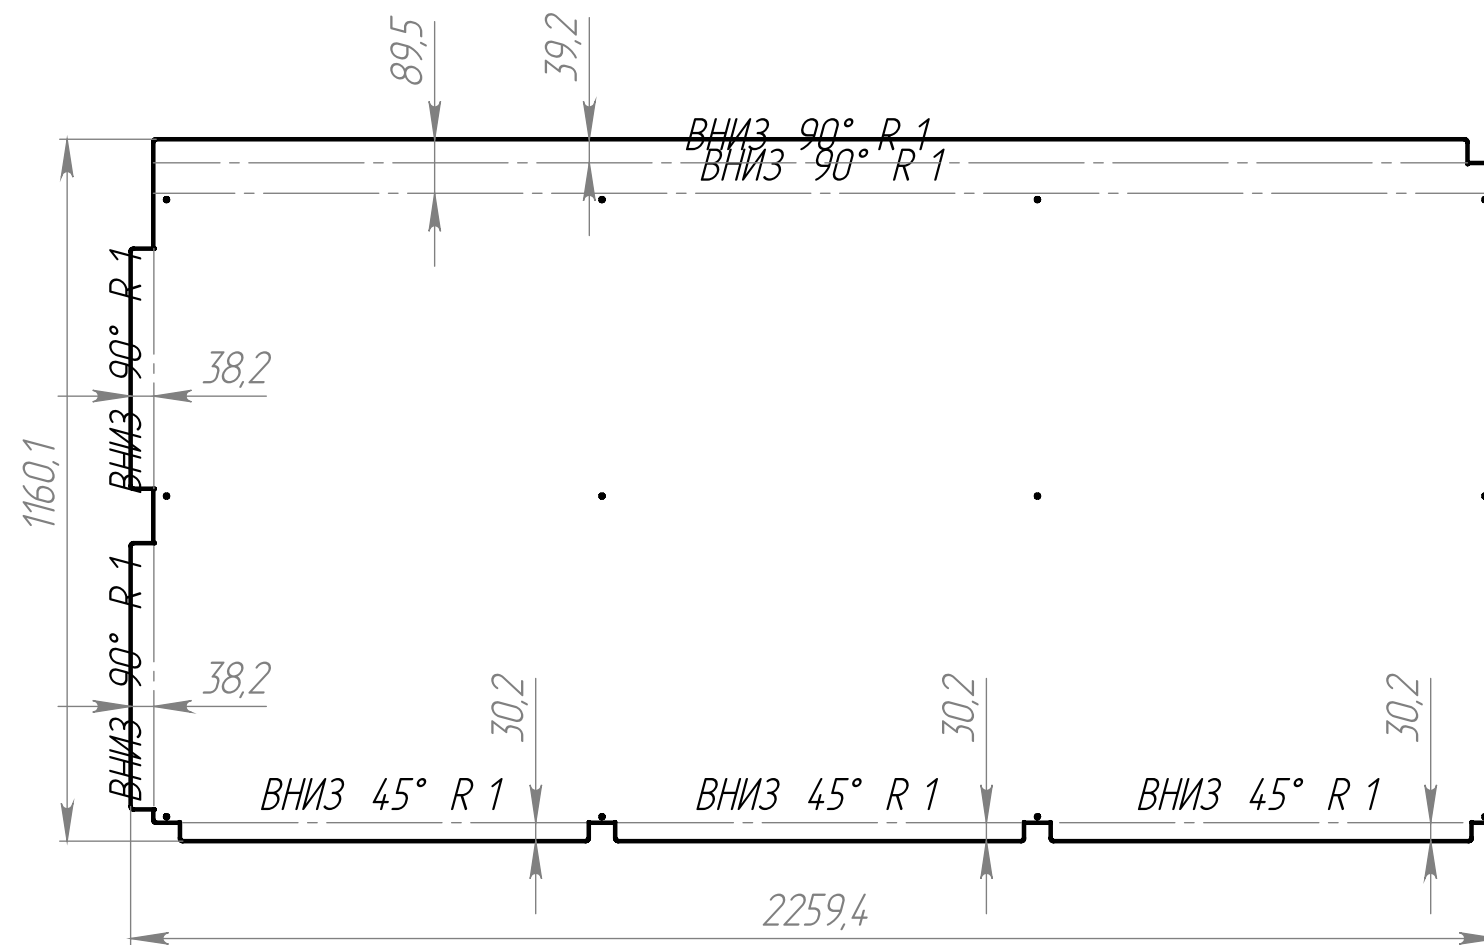
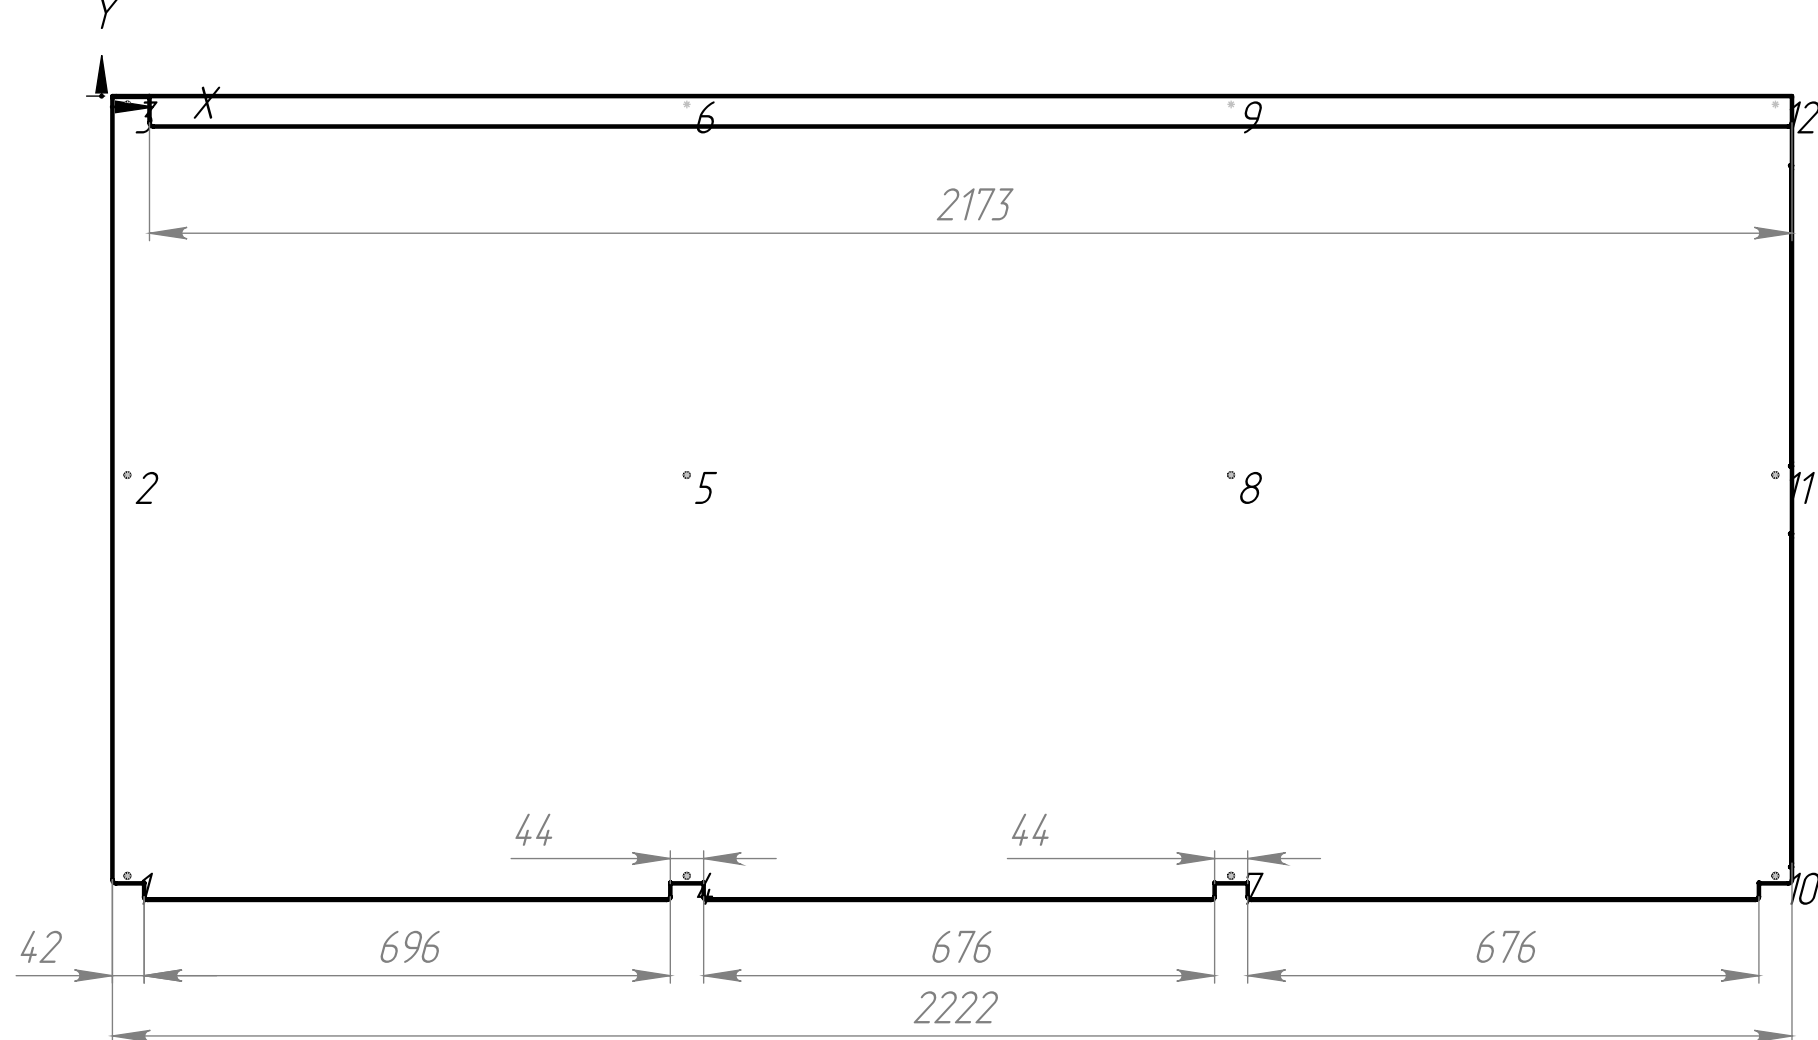
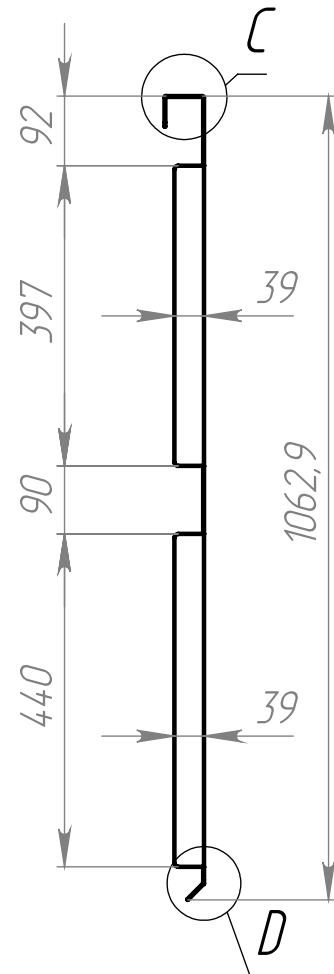


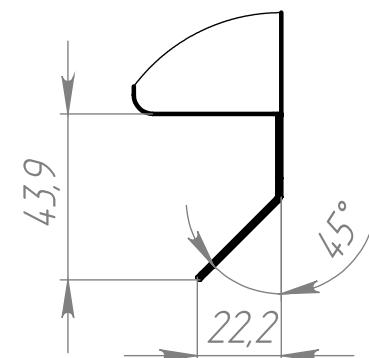






BPXN.BM02.01.00.32

 $D(1:2)$ 

МЕТКА	X	Y	РАЗМЕР
1	20	-1031	Ø 4,8 НАКБ03Б
2	20	-501	Ø 4,8 НАКБ03Б
3	20	-11	Ø 4,8 НАКБ03Б
4	760	-1031	Ø 4,8 НАКБ03Б
5	760	-501	Ø 4,8 НАКБ03Б
6	760	-11	Ø 4,8 НАКБ03Б
7	1480	-1031	Ø 4,8 НАКБ03Б
8	1480	-501	Ø 4,8 НАКБ03Б
9	1480	-11	Ø 4,8 НАКБ03Б
10	2200	-1031	Ø 4,8 НАКБ03Б
11	2200	-501	Ø 4,8 НАКБ03Б
12	2200	-11	Ø 4,8 НАКБ03Б

					ВРХИ.ВМ02.01.00.32								
					Облицовочный щит (Исп.1 лев.)				Лит.		Масса	Масштаб	
Изм.	Лист	№ докум.	Подп.	Дата								20.81	1:10
Разраб.													
Пров.													
Т. контр.									Лист 2			Листов 11	
					Лист AISI 304								
Н. контр.													
Утв.													






BPXN.BM03.01.00.32

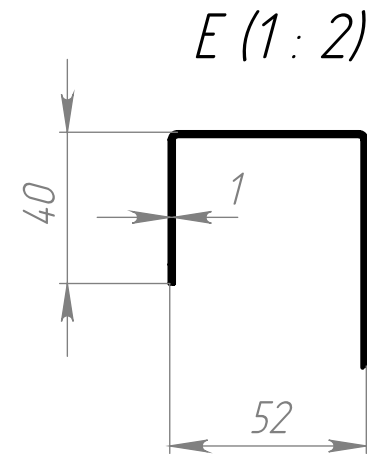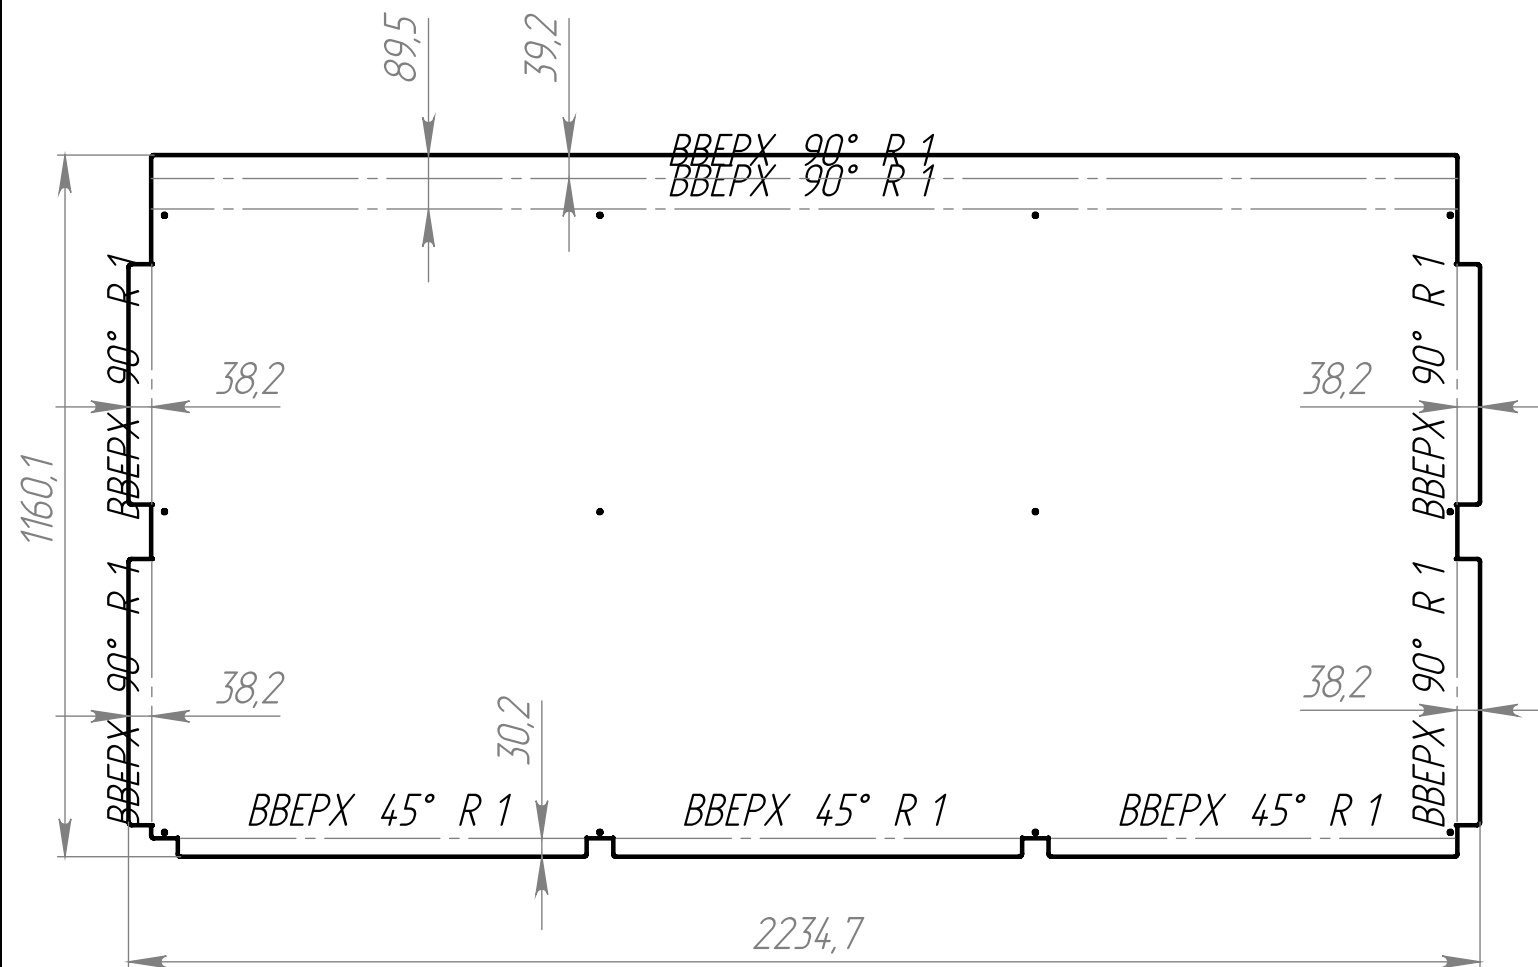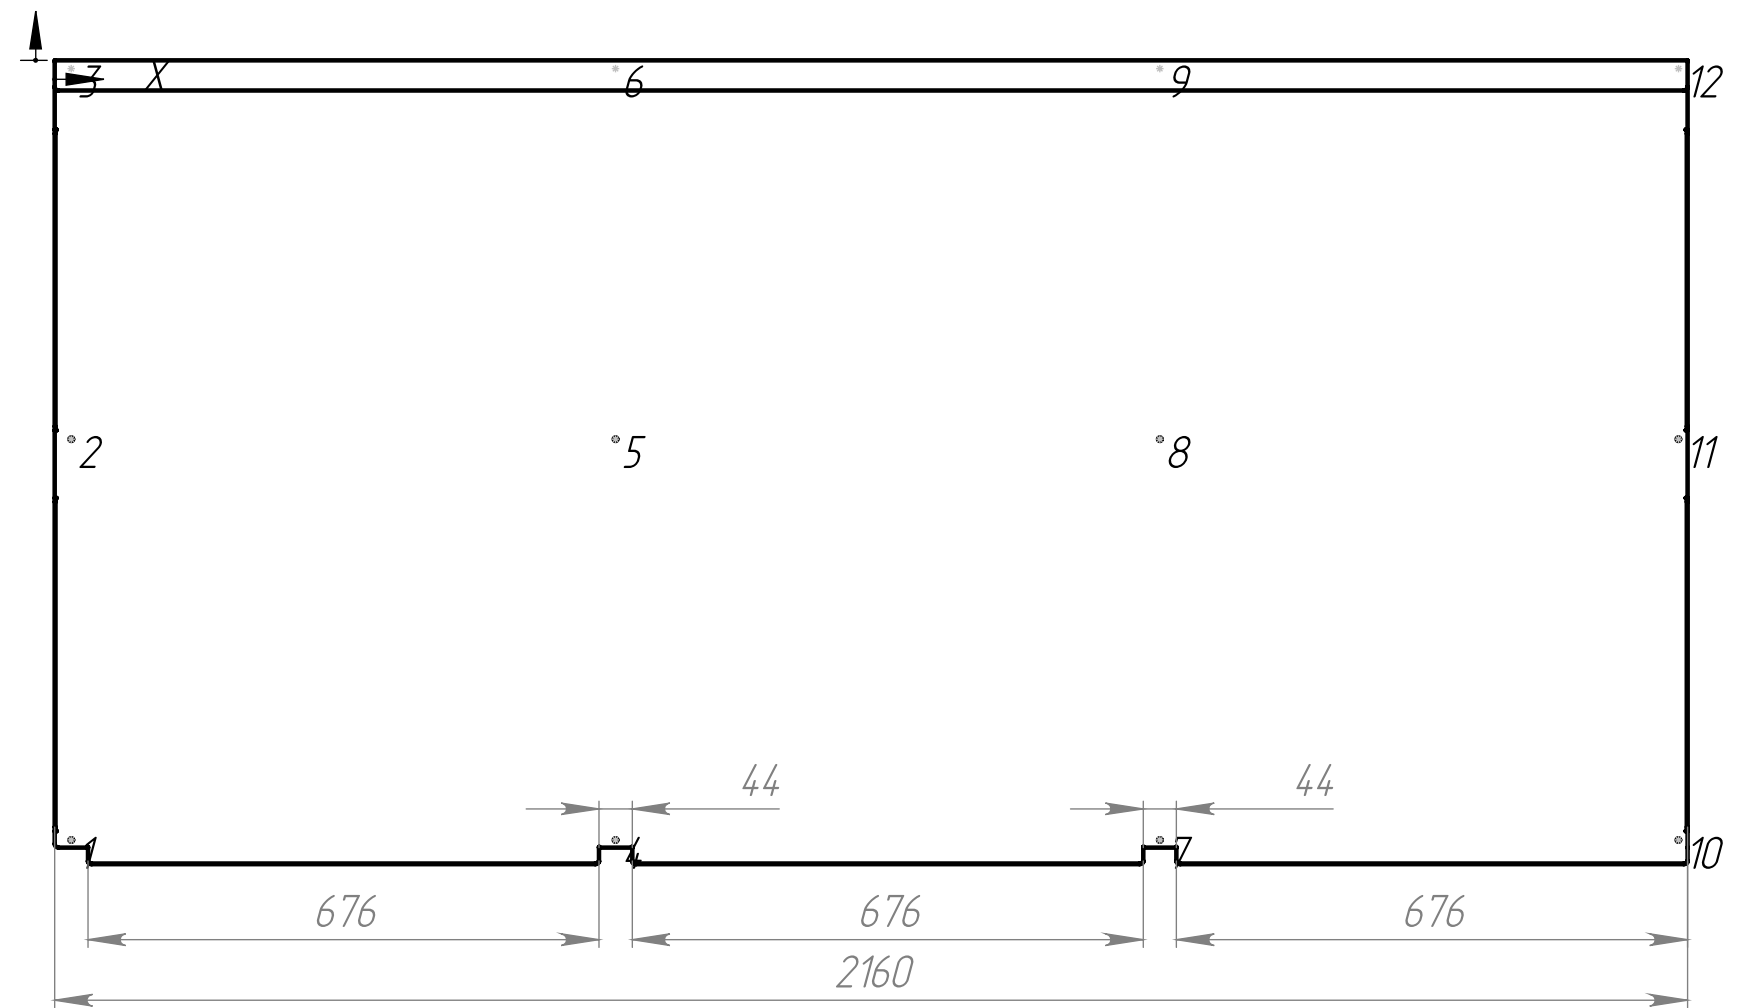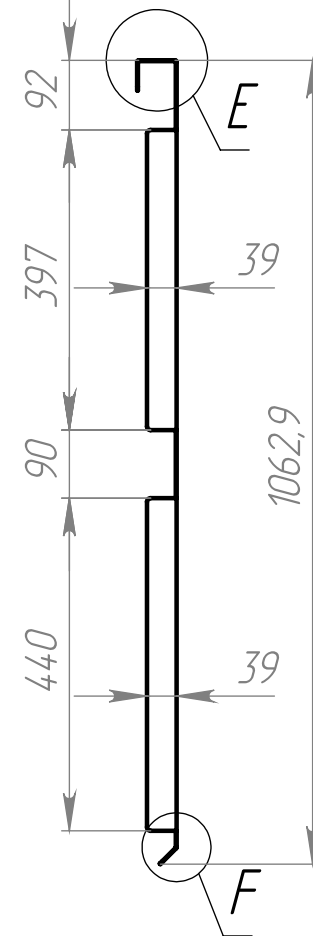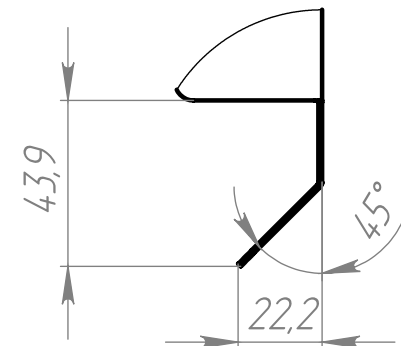
$$F(1:2)$$


МЕТКА	X	Y	ПАЗМЕР
1	22	-1031	Ø 4,8 НАСКВОЗЬ
2	22	-501	Ø 4,8 НАСКВОЗЬ
3	22	-11	Ø 4,8 НАСКВОЗЬ
4	742	-1031	Ø 4,8 НАСКВОЗЬ
5	742	-501	Ø 4,8 НАСКВОЗЬ
6	742	-11	Ø 4,8 НАСКВОЗЬ
7	1462	-1031	Ø 4,8 НАСКВОЗЬ
8	1462	-501	Ø 4,8 НАСКВОЗЬ
9	1462	-11	Ø 4,8 НАСКВОЗЬ
10	2148	-1031	Ø 4,8 НАСКВОЗЬ
11	2148	-501	Ø 4,8 НАСКВОЗЬ
12	2148	-11	Ø 4,8 НАСКВОЗЬ

					ВРХИ.ВМ03.01.00.32						
					Облицовочный щит (Исп.2 прав.)	Лит.			Масса	Масштаб	
Изм.	Лист	№ докум.	Подп.	Дата					20.51	1:10	
Разраб.											
Пров.											
Т. контр.						Лист 3			Листов 11		
					Лист <u>AISI 304</u>						
Н. контр.											
Утв.											

ВРХИ.ВМ04.01.00.32

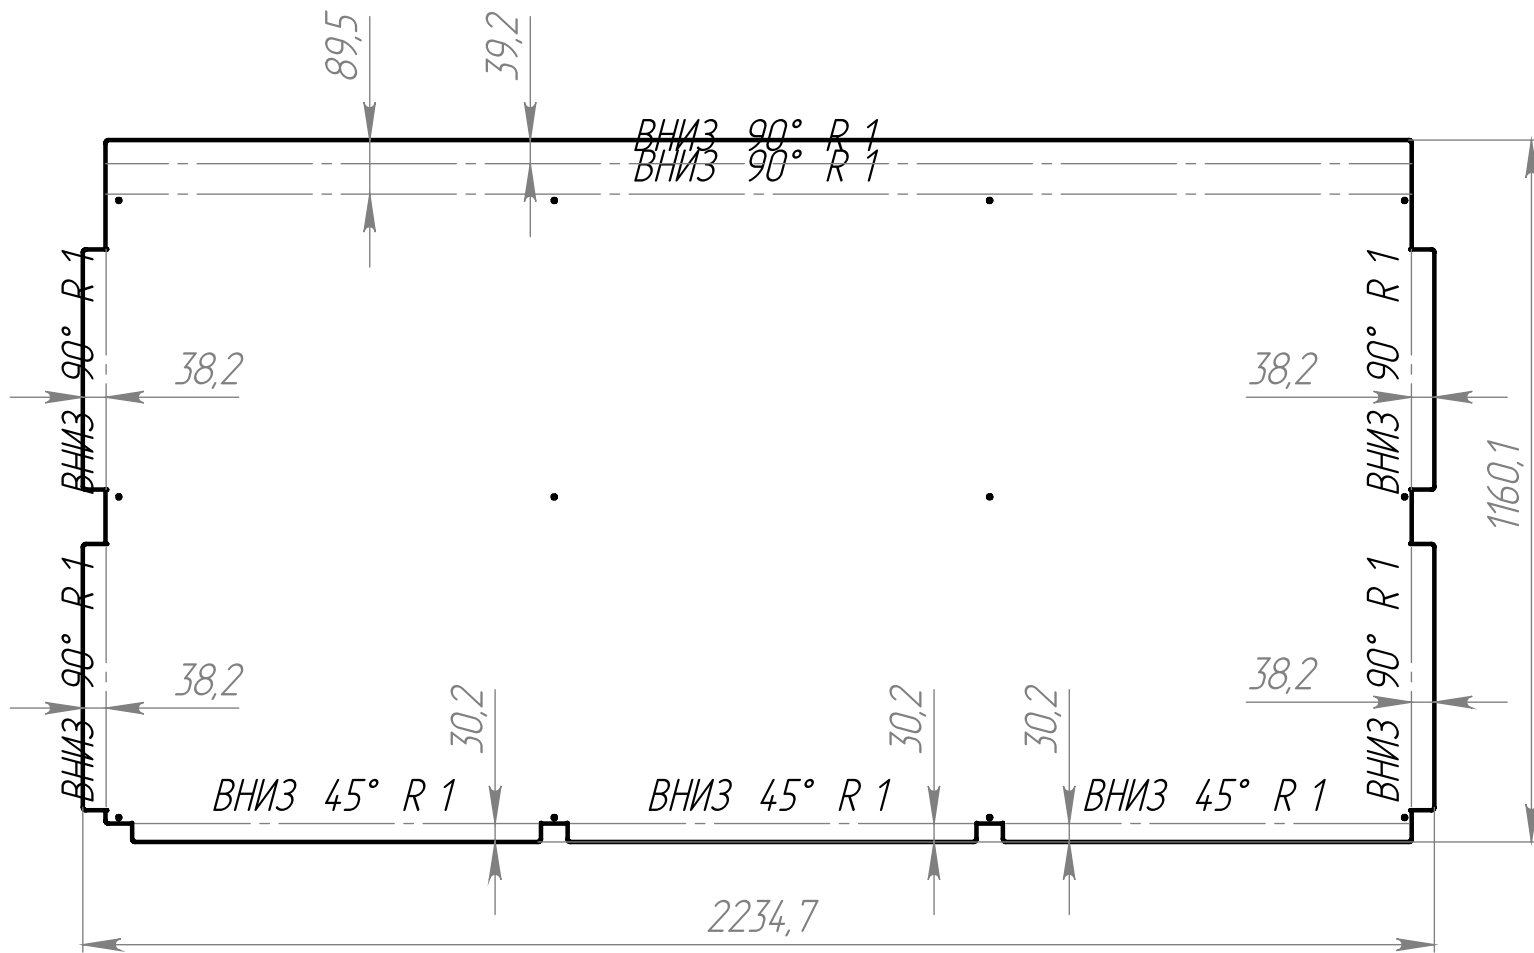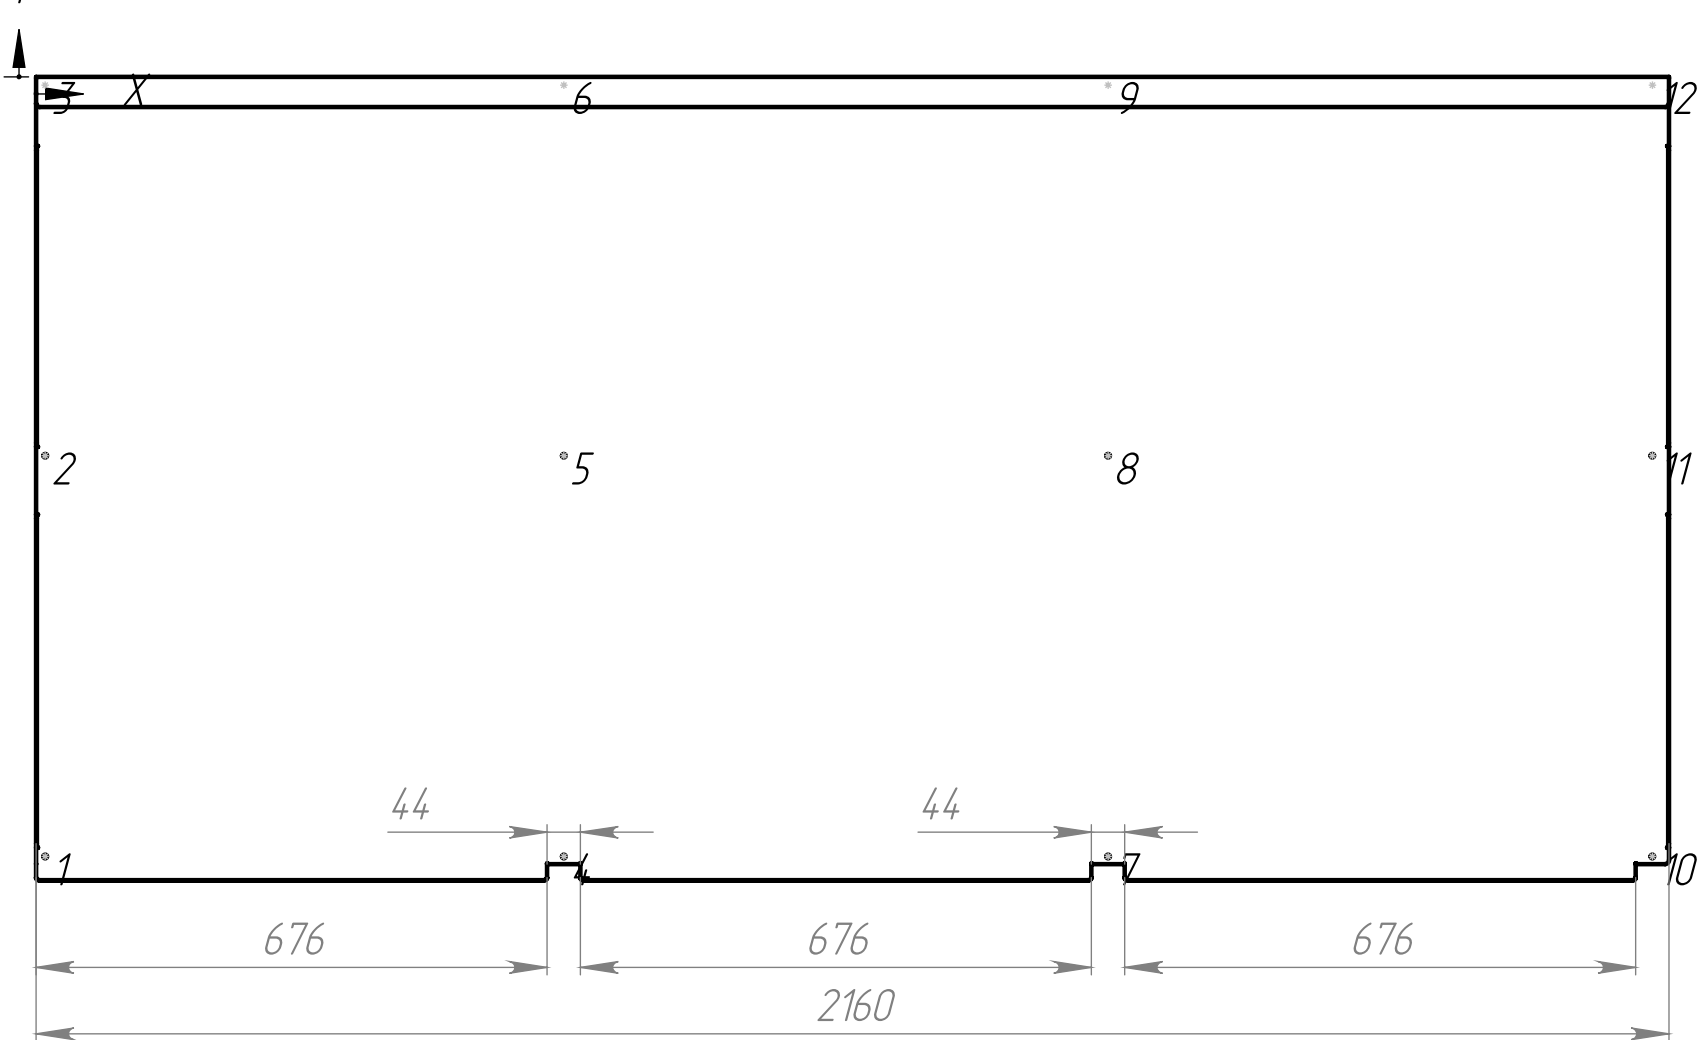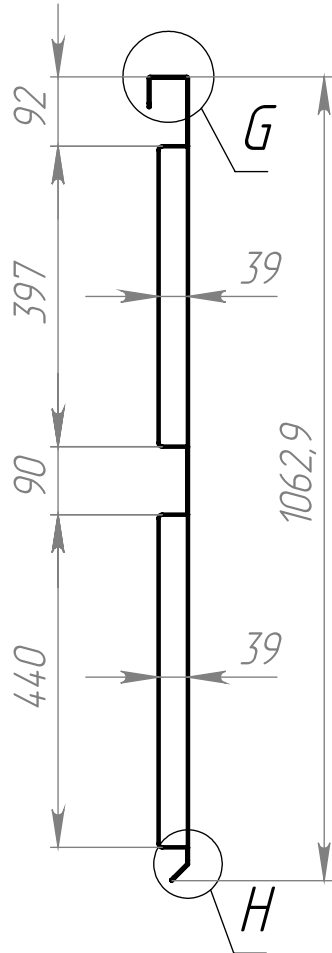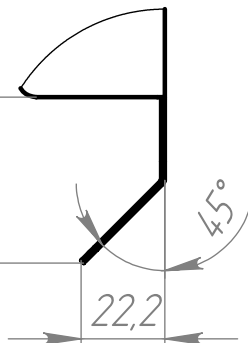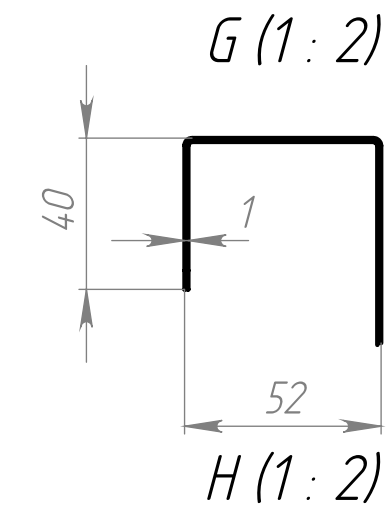

МЕТКА	X	Y	РАЗМЕР
1	12	-1031	Φ 4,8 НАСКВОЗЬ
2	12	-501	Φ 4,8 НАСКВОЗЬ
3	12	-11	Φ 4,8 НАСКВОЗЬ
4	698	-1031	Φ 4,8 НАСКВОЗЬ
5	698	-501	Φ 4,8 НАСКВОЗЬ
6	698	-11	Φ 4,8 НАСКВОЗЬ
7	1418	-1031	Φ 4,8 НАСКВОЗЬ
8	1418	-501	Φ 4,8 НАСКВОЗЬ
9	1418	-11	Φ 4,8 НАСКВОЗЬ
10	2138	-1031	Φ 4,8 НАСКВОЗЬ
11	2138	-501	Φ 4,8 НАСКВОЗЬ
12	2138	-11	Φ 4,8 НАСКВОЗЬ

Изм.

Лист

№ докум.

Подп.

Дата

Разраб.

Пров.

Т. контр.

Н. контр.

Утв.

ВРХИ.ВМ04.01.00.32

Облицовочный щит (Исп.2 лев.)

Лист AISI 304

Лит.

Масса

Масштаб






Лист 4

Листов 11

Формат А3

Перв. примен.		Справ. №		Подп. и дата		Инв. № дубл.		Взам. инв. №		Подп. и дата		Инв. № подл.	




ВРХИ.ВМ05.01.00.32

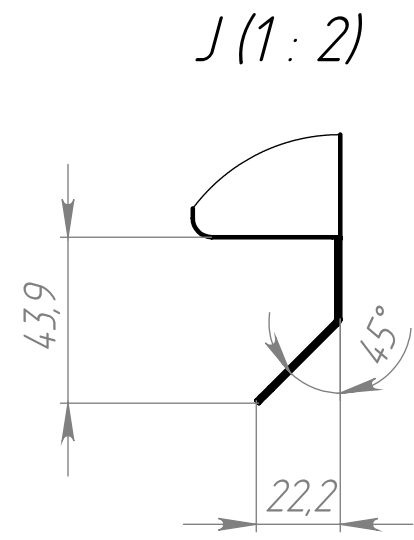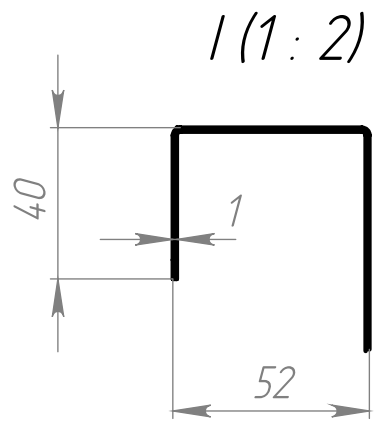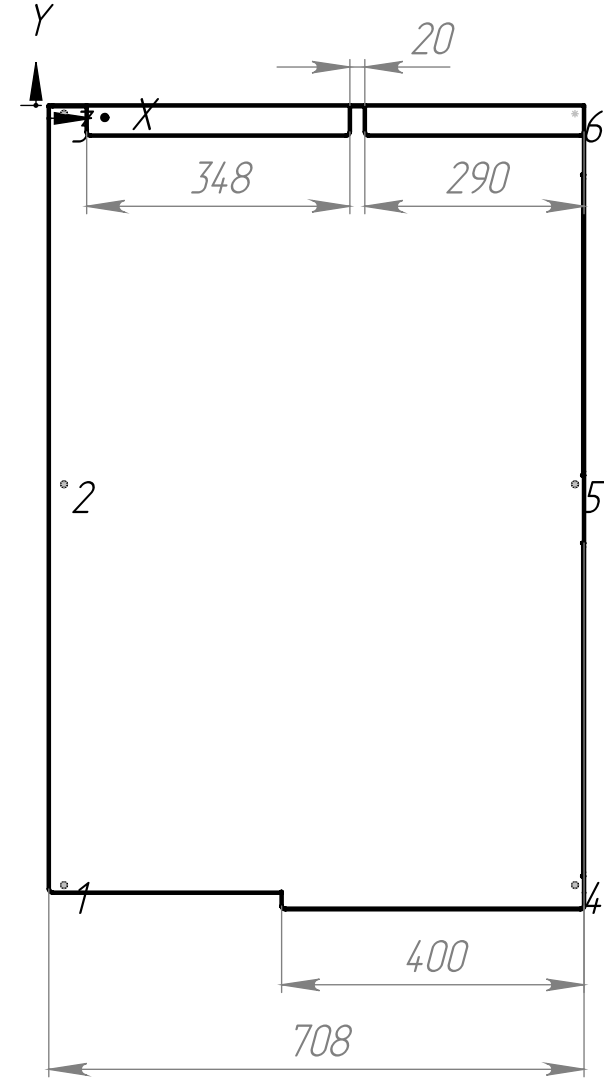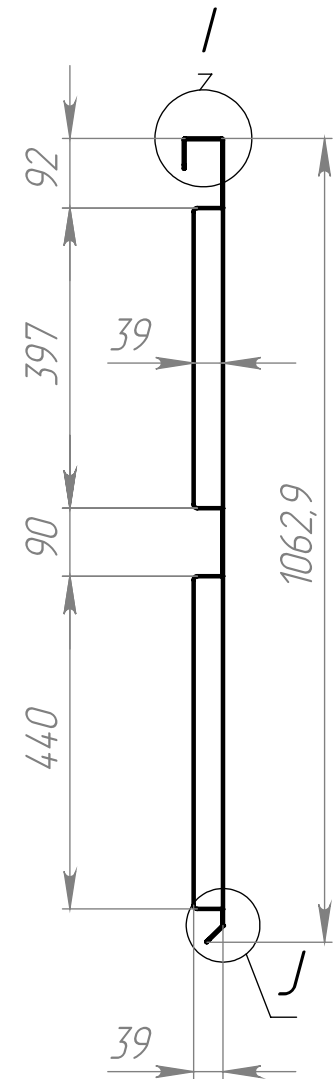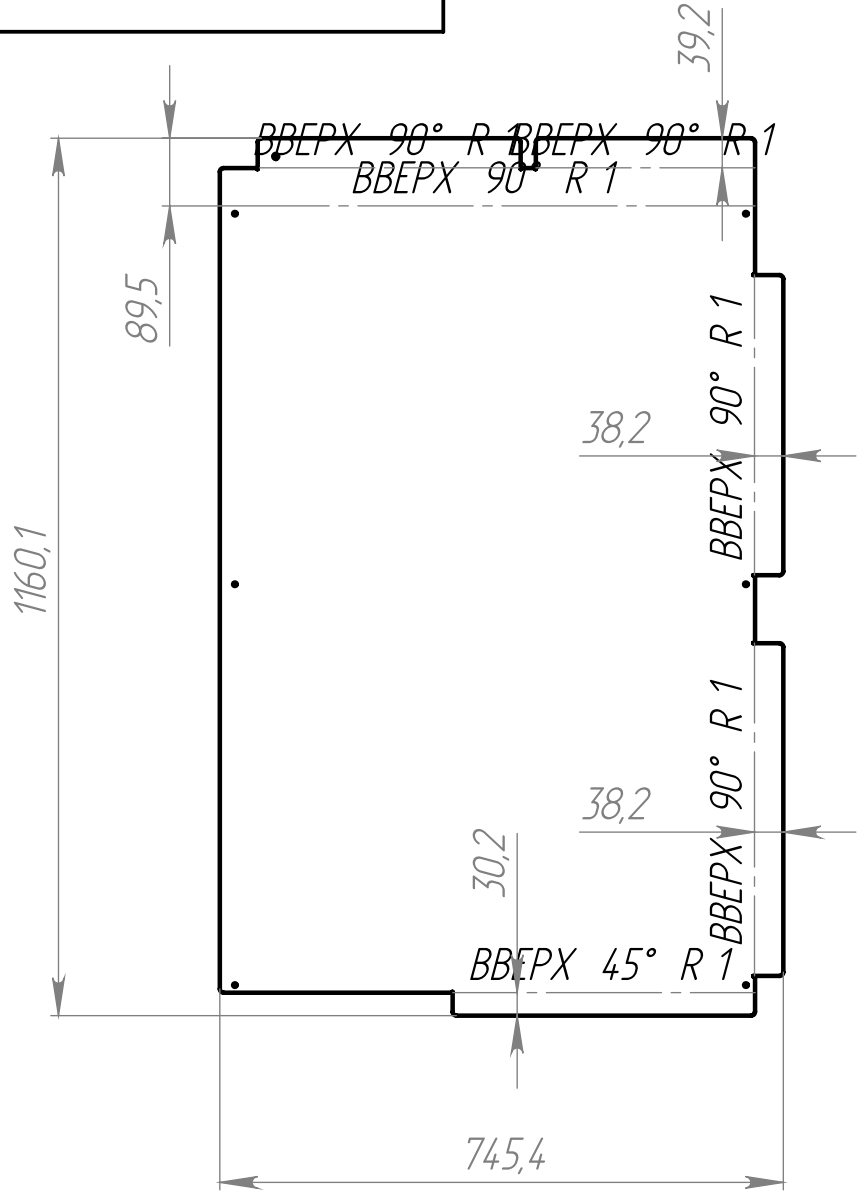



МЕТКА	X	Y	РАЗМЕР
1	20	-1031	Φ 4,8 НАСКВОЗЬ
2	20	-501	Φ 4,8 НАСКВОЗЬ
3	20	-11	Φ 4,8 НАСКВОЗЬ
4	696	-1031	Φ 4,8 НАСКВОЗЬ
5	696	-501	Φ 4,8 НАСКВОЗЬ
6	696	-11	Φ 4,8 НАСКВОЗЬ

					ВРХИ.ВМ05.01.00.32						
					Облицовочный щит (Исп.3 прав.)	Лит.			Масса	Масштаб	
Изм.	Лист	№ докум.	Подп.	Дата					6.72	1:10	
Разраб.											
Пров.											
Т. контр.											
						Лист 5			Листов 11		
Н. контр.					Лист AISI 304						
Утв.											

ВРХИ.ВМ06.01.00.32



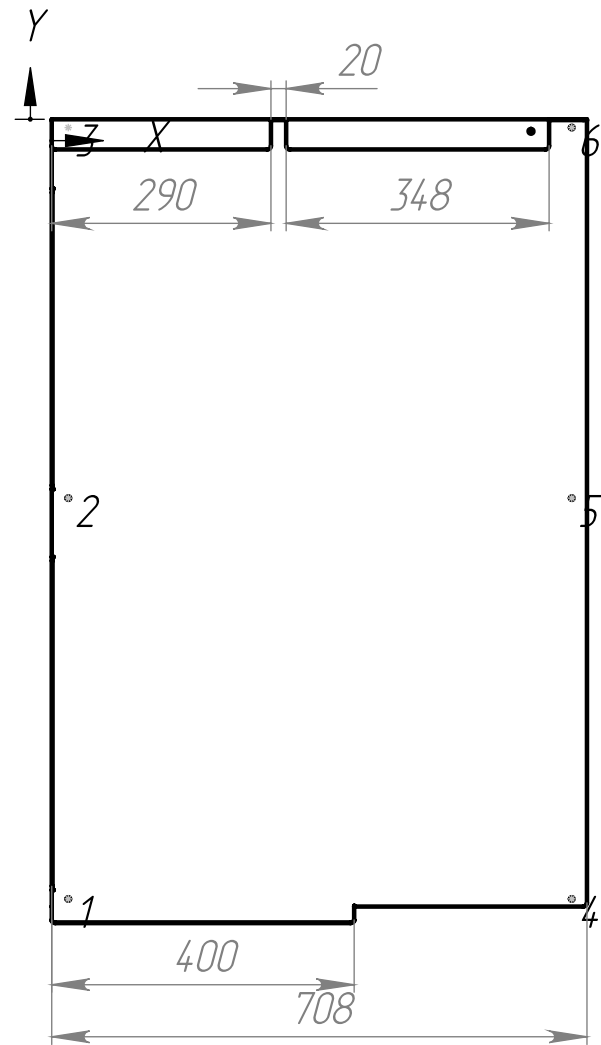
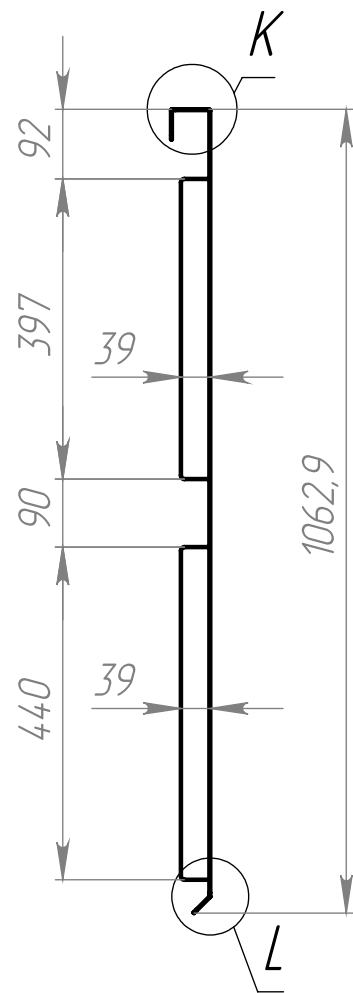
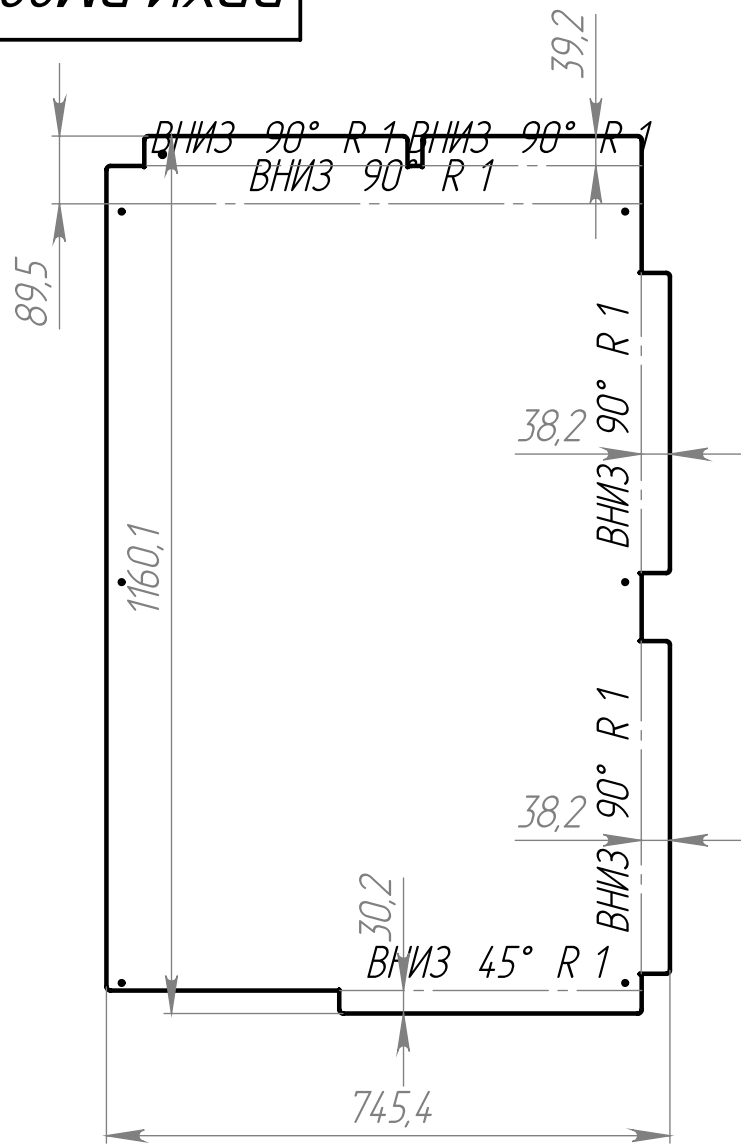


МЕТКА	X	Y	РАЗМЕР
1	22	-1031	Φ 4,8 НАКВОЗЬ
2	22	-501	Φ 4,8 НАКВОЗЬ
3	22	-11	Φ 4,8 НАКВОЗЬ
4	688	-1031	Φ 4,8 НАКВОЗЬ
5	688	-501	Φ 4,8 НАКВОЗЬ
6	688	-11	Φ 4,8 НАКВОЗЬ

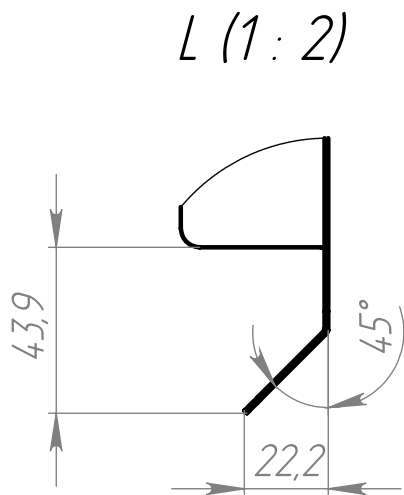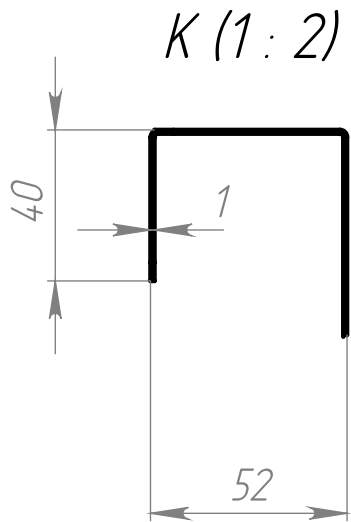

					ВРХИ.ВМ06.01.00.32											
					Облицовочный щит (Исп.3 лев.)						Лит.		Масса	Масштаб		
															6.72	1:10
Изм.	Лист	№ докум.	Подп.	Дата							Лист 6		Листов 11			
Разраб.																
Пров.																
Т. контр.																
Н. контр.																
Утв.																


BPXI.BM07.01.00.32

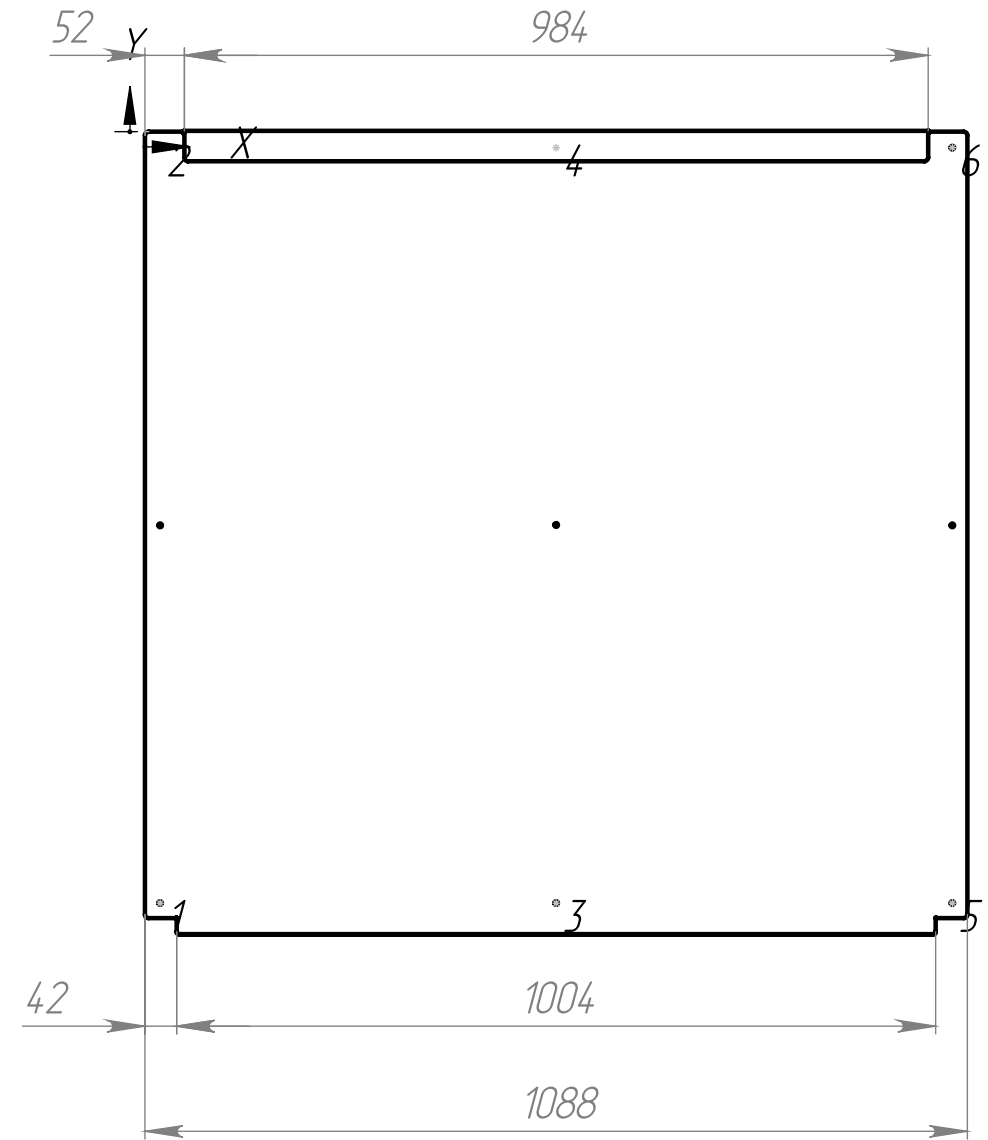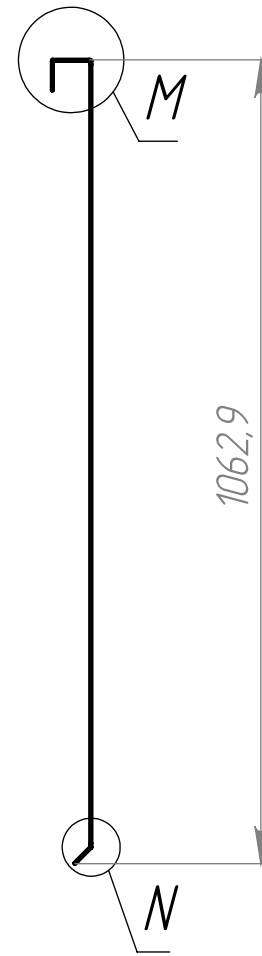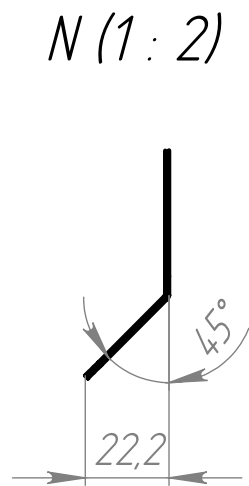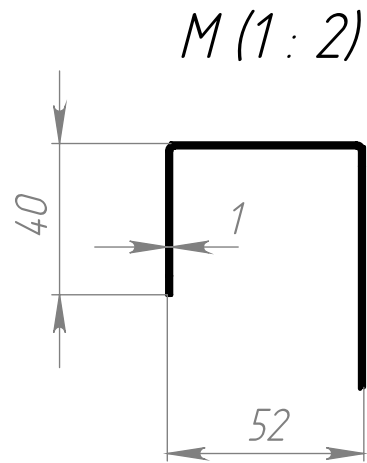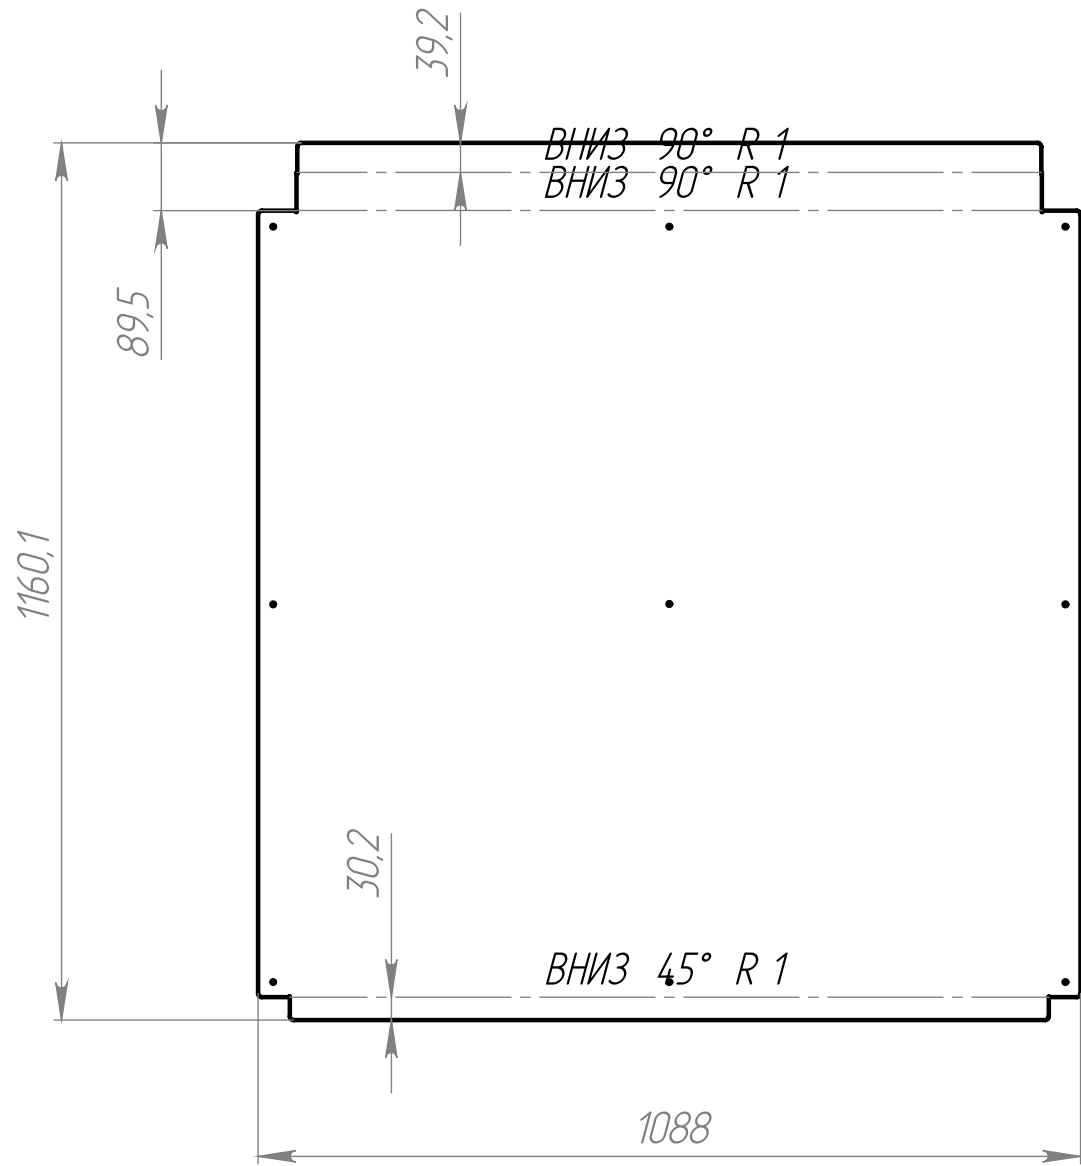

МЕТКА	X	Y	РАЗМЕР
1	20	-1020	Ø 4,8 НАКВ03б
2	20	-21	Ø 4,8 НАКВ03б
3	544	-1020	Ø 4,8 НАКВ03б
4	544	-21	Ø 4,8 НАКВ03б
5	1068	-1020	Ø 4,8 НАКВ03б
6	1068	-21	Ø 4,8 НАКВ03б

					ВРХИ.ВМ07.01.00.32								
					Торец				Лит.		Масса	Масштаб	
Изм.	Лист	№ докум.	Подп.	Дата								10.00	1:10
Разраб.													
Пров.													
Т. контр.									Лист 7		Листов 11		
					Лист <u>AISI 304</u>								
Н. контр.													
Утв.													


ВРХИ.ВМ.93.01.00.32 СБ

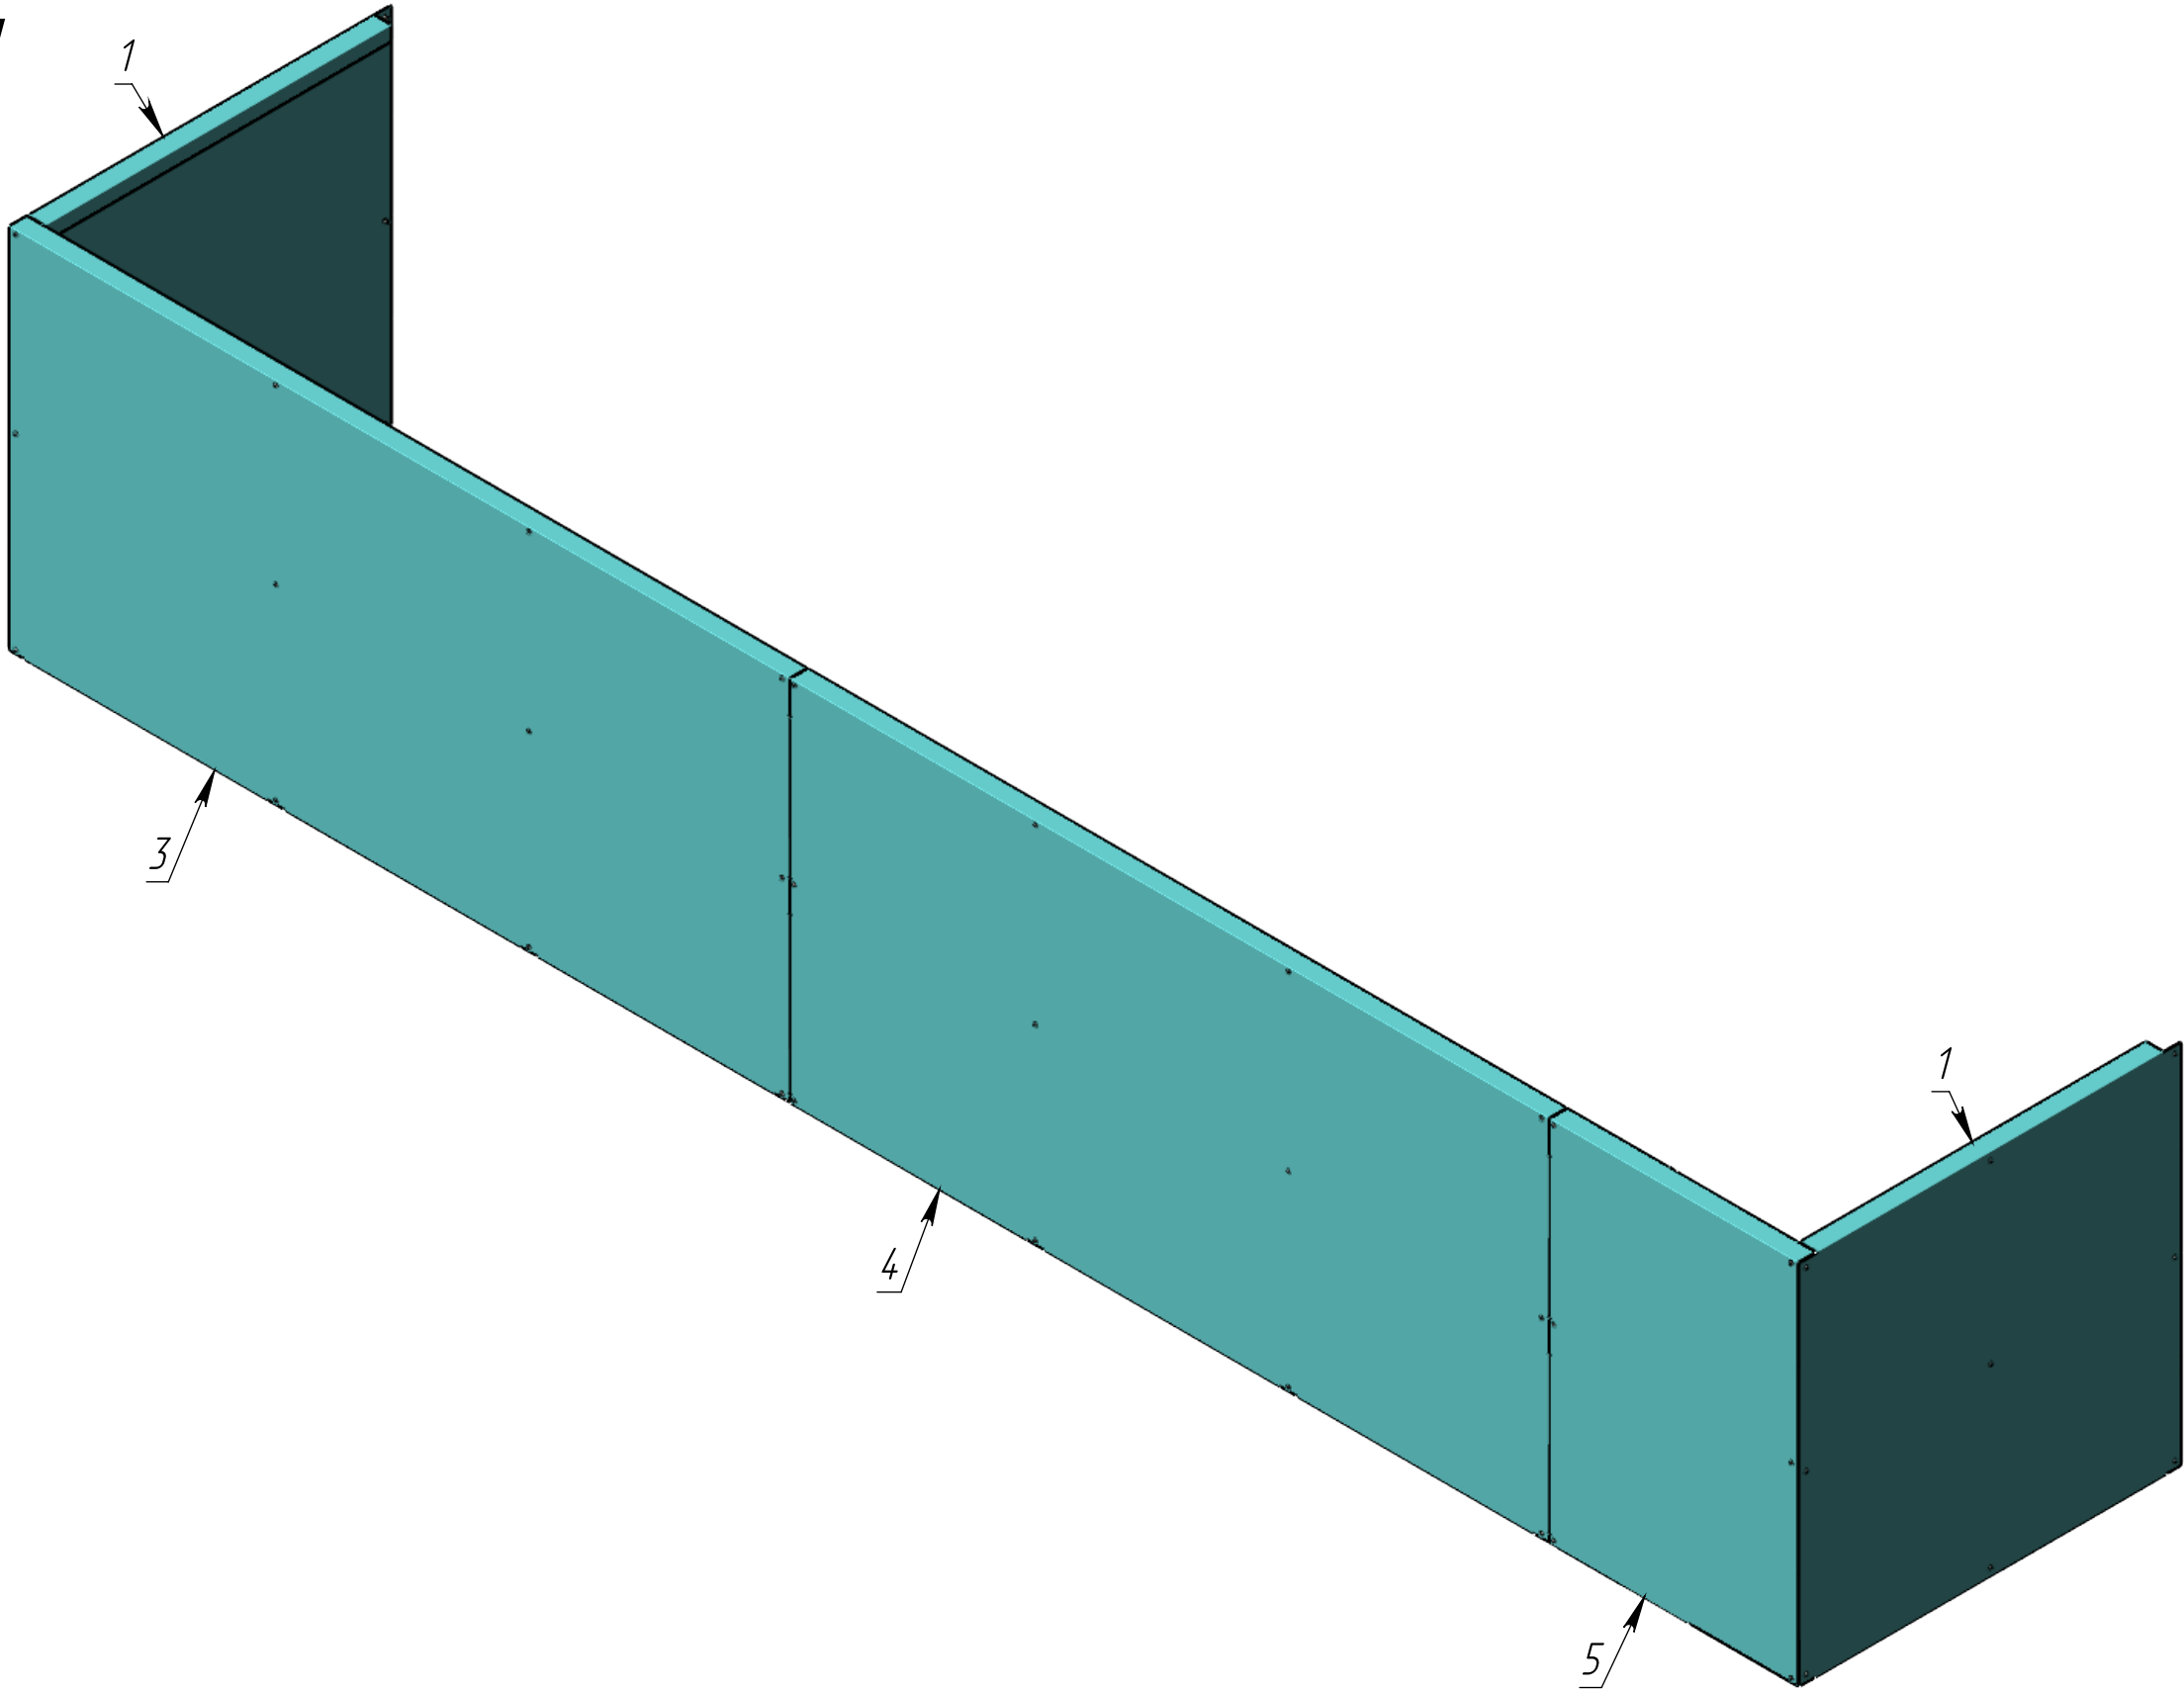

Поз.	ОБОЗНАЧЕНИЕ	ОПИСАНИЕ	К-ВО
1	Торец	ВРХИ.ВМ07.01.00.32	2
2	Заклепка 4,8х10 AISI304	Стандартное изделие	48
3	Облицовочный щит (Исп.1 прав.)	ВРХИ.ВМ01.01.00.32	1
4	Облицовочный щит (Исп.2 прав.)	ВРХИ.ВМ03.01.00.32	1
5	Облицовочный щит (Исп.3 прав.)	ВРХИ.ВМ05.01.00.32	1

					ВРХИ.ВМ.93.01.00.32 СБ						
					Облицовка (прав.)	Лит.			Масса	Масштаб	
Изм.	Лист	№ докум.	Подп.	Дата					68.14	1:15	
Разраб.											
Пров.											
Т. контр.											
						Лист 8			Листов 11		
					Сборочная единица						
Н. контр.											
Утв.											

ВРХИ.ВМ.93.02.00.32 СБ



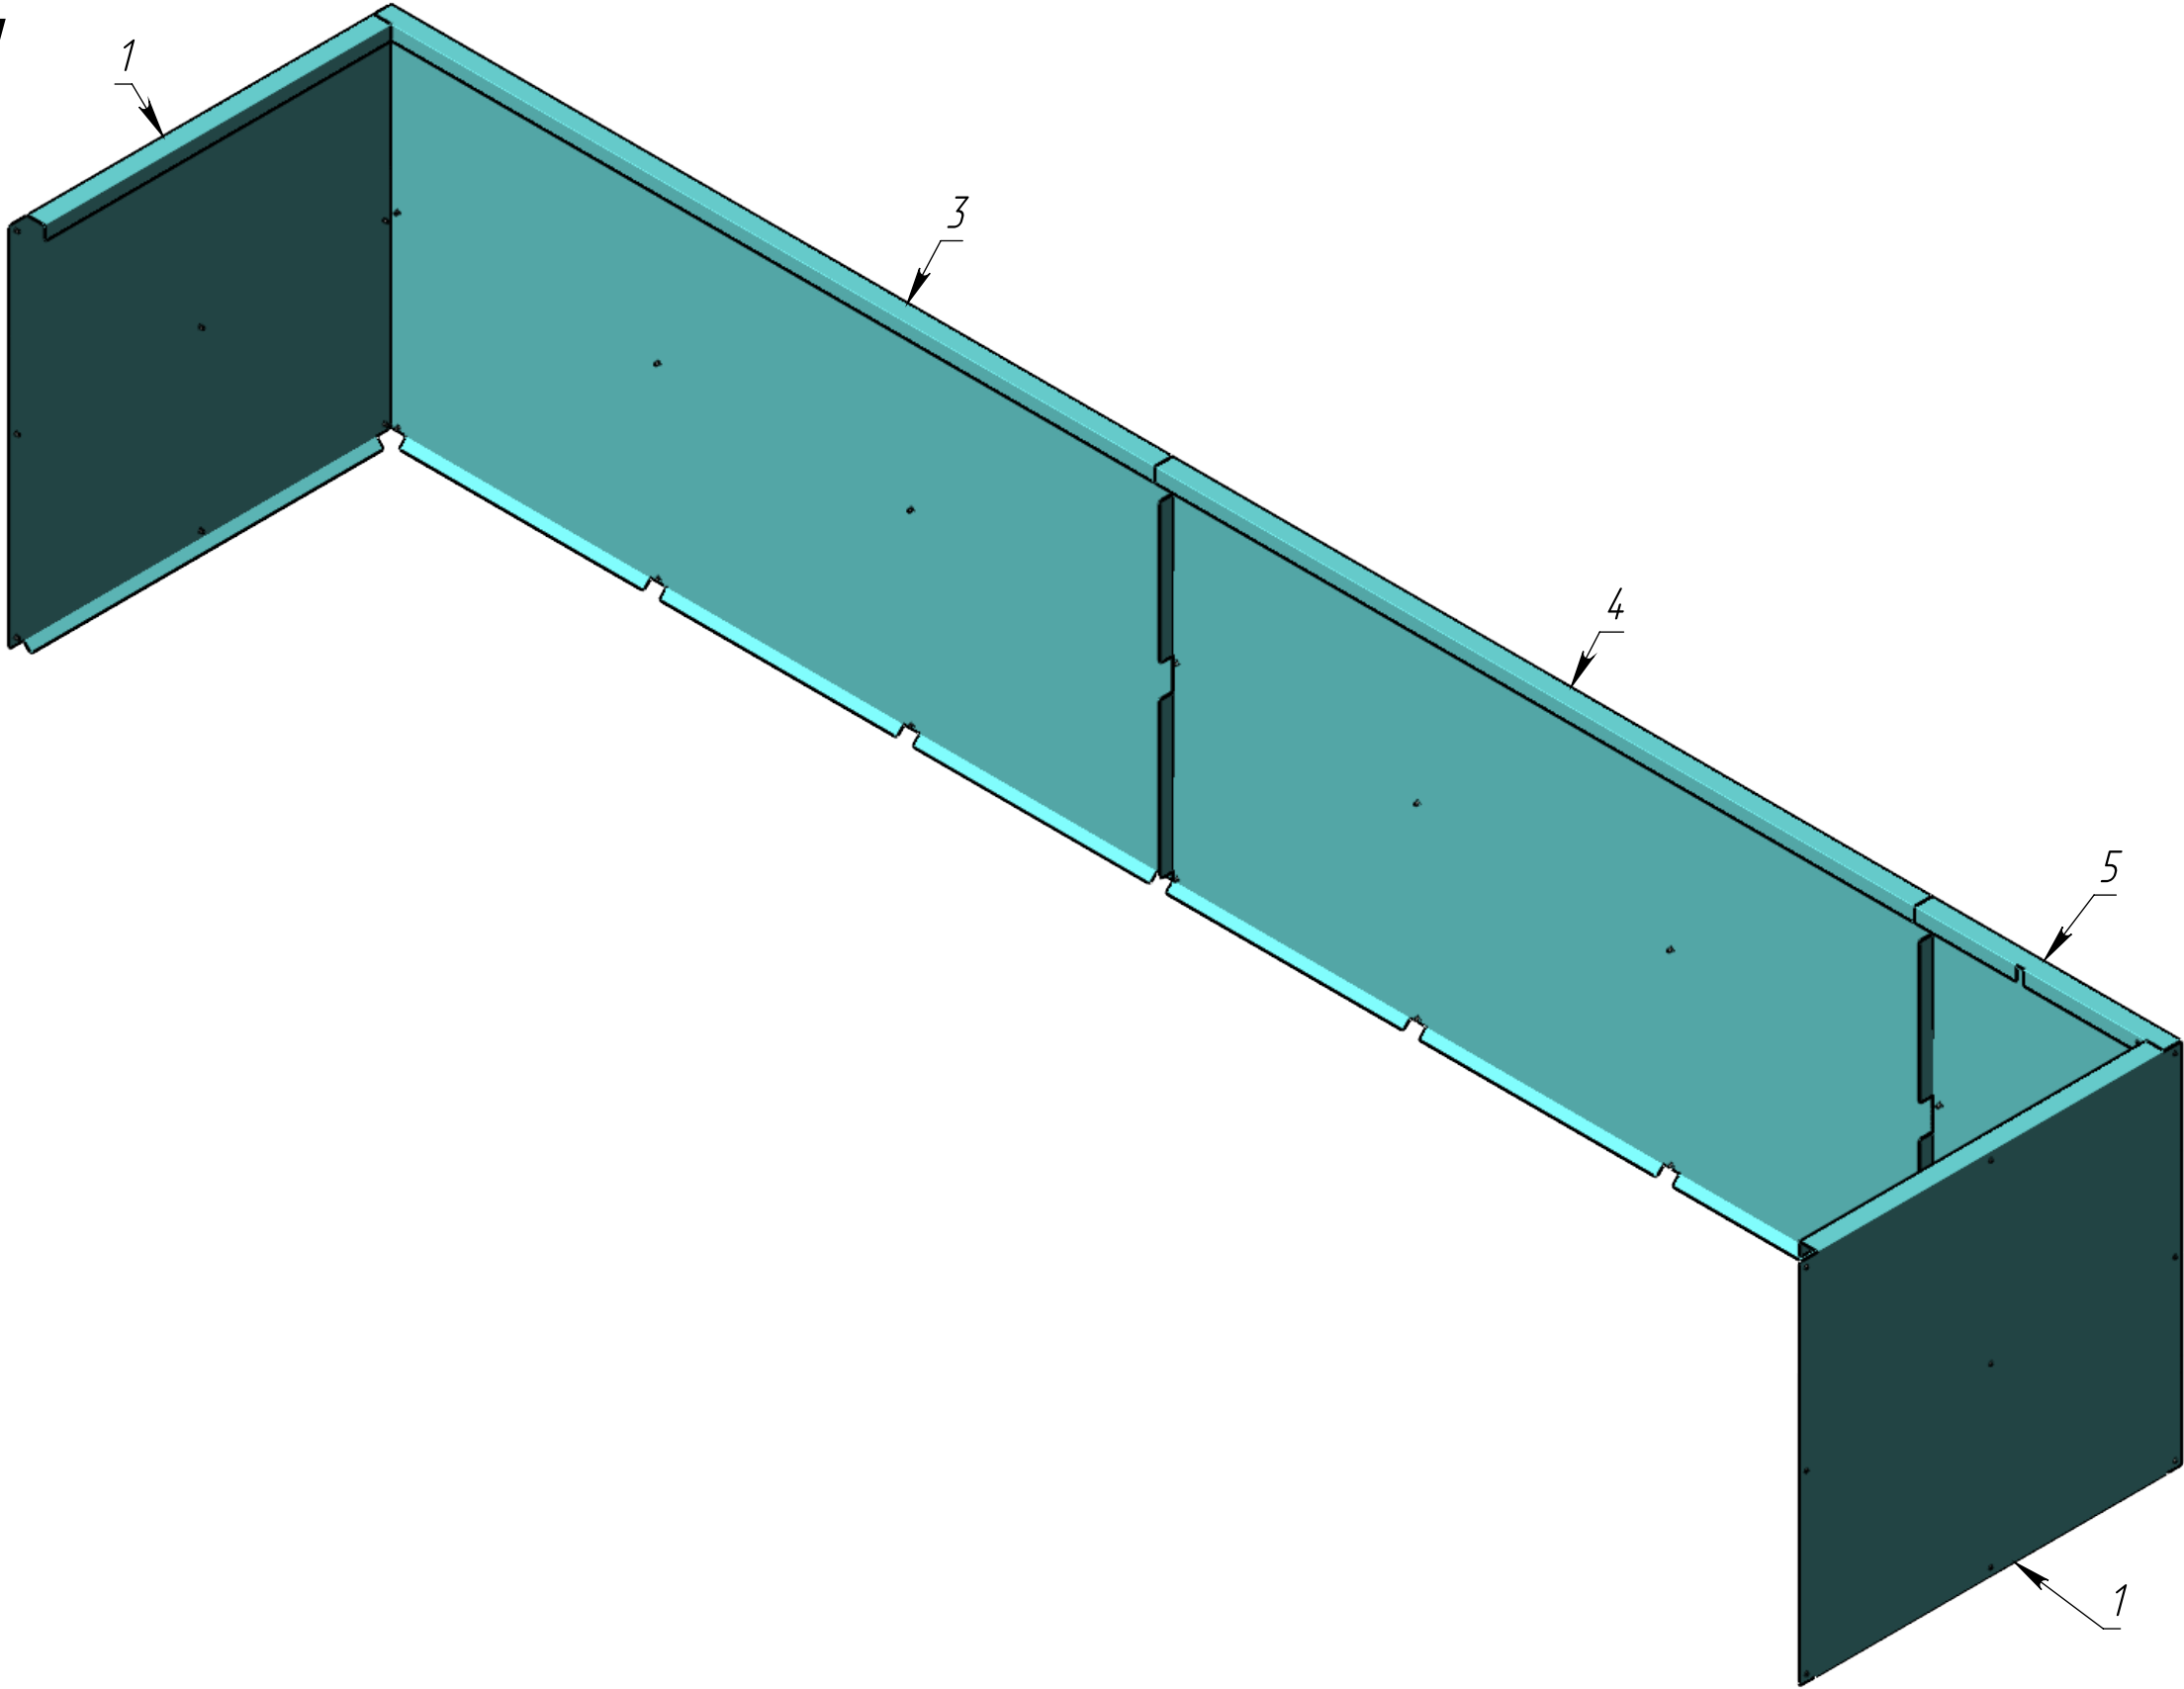


Поз.	ОБОЗНАЧЕНИЕ	ОПИСАНИЕ	К-ВО
1	Торец	ВРХИ.ВМ07.01.00.32	2
2	Заклепка 4,8х10 AISI304	Стандартное изделие	48
3	Облицовочный щит (Исп.1 лев.)	ВРХИ.ВМ02.01.00.32	1
4	Облицовочный щит (Исп.2 лев.)	ВРХИ.ВМ04.01.00.32	1
5	Облицовочный щит (Исп.3 лев.)	ВРХИ.ВМ06.01.00.32	1

					ВРХИ.ВМ.93.02.00.32 СБ			
Изм.	Лист	№ докум.	Подп.	Дата	Облицовка (лев.)	Лит.	Масса	Масштаб
							68.14	1:15
						Лист 9 Листов 11		
					Сборочная единица			

Инв. № подл.	Подп. и дата	Взам. инв. №	Инв. № дубл.	Подп. и дата

BPXI.BM99.01.00.32

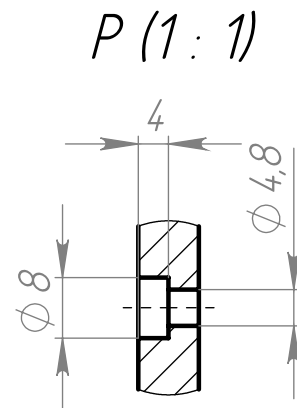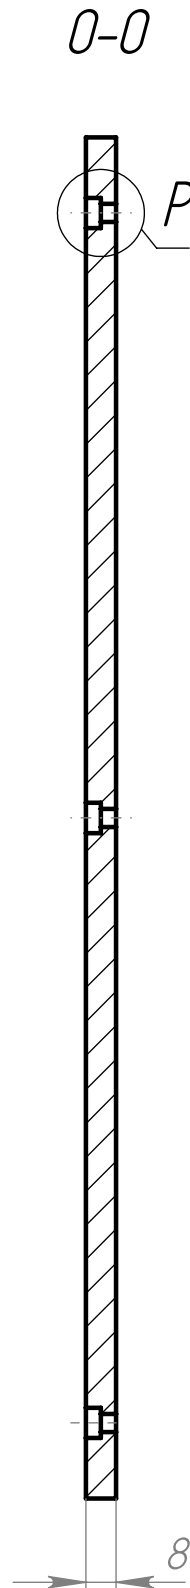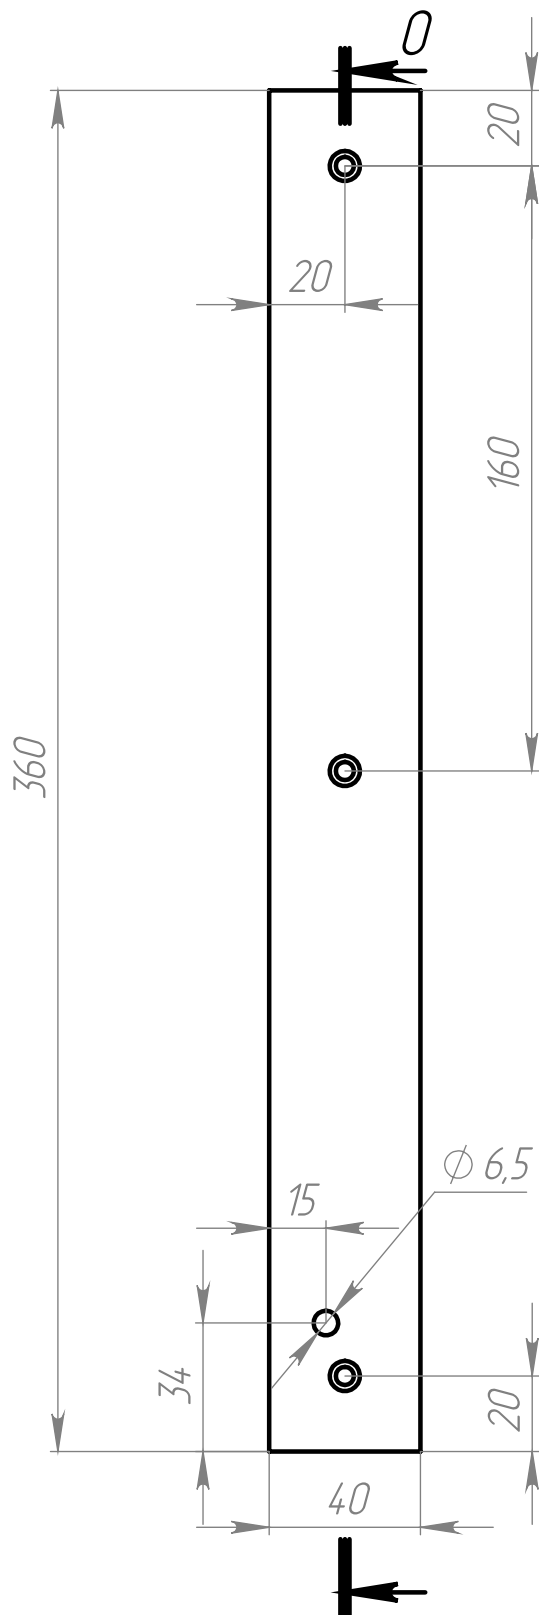

ВРХИ.ВМ99.01.00.32

Проставка боковая

Лист Полипропилен ГОСТ 26996-86

Лит.			Масса	Масштаб
			0.10	1:2
Лист 10			Листов 11	

Справ. №		Перв. примен.	
Инв. № подл.		Подп. и дата	
Взам. инв. №		Инв. № дубл.	
Подп. и дата		Инв. инв. №	
Инв. № подл.		Подп. и дата	
Изм.		Лист	
Разраб.		№ докум.	
Пров.		Подп.	
Т. контр.		Дата	
Н. контр.			
Утв.			

ВРХИ.ВМ98.01.00.32

992

40

Q

20

20

476

20

Q

Q-Q

R

R (1:1)

4

4,8

8

ВРХИ.ВМ98.01.00.32

Проставка торцевая

Лит. Масса Масштаб

Лист 11

Листов 11

Лист Полипропилен ГОСТ 26996-86