


Подп. и дата	Инв. № дубл.	Взам. инв. №	Подп. и дата	Инв. № подл.



Позиция	Количество	Наименование	ДЛИНА
1	2	Труба 40 X 40 X 3 ГОСТ8639-82	1088
2	1	Труба 40 X 40 X 3 ГОСТ8639-82	5090
3	16	Труба 40 X 40 X 3 ГОСТ8639-82	1240
4	4	Труба 40 X 20 X 2 ГОСТ8645-68	670
5	8	Труба 40 X 20 X 2 ГОСТ8645-68	700.08
6	2	Труба 40 X 20 X 2 ГОСТ8645-68	1008
7	4	Труба 40 X 20 X 2 ГОСТ8645-68	494
8	2	Труба 40 X 20 X 2 ГОСТ8645-68	4261.04
9	5	Труба 40 X 20 X 2 ГОСТ8645-68	968
10	2	Труба 40 X 20 X 2 ГОСТ8645-68	1088
11	1	Труба 40 X 20 X 2 ГОСТ8645-68	690.07
12	1	Труба 40 X 20 X 2 ГОСТ8645-68	670.66
13	1	Труба 40 X 20 X 2 ГОСТ8645-68	980
14	1	Труба 40 X 20 X 2 ГОСТ8645-68	860
15	18	Труба 40 X 20 X 2 ГОСТ8645-68	680
16	2	Труба 40 X 20 X 2 ГОСТ8645-68	400
17	1	Труба 40 X 20 X 2 ГОСТ8645-68	450
18	3	Уголок 35x35x3 ГОСТ 8509-86	1008
19	1	Труба 40 X 20 X 2 ГОСТ8645-68	338
20	1	Труба 40 X 40 X 3 ГОСТ8639-82	5090

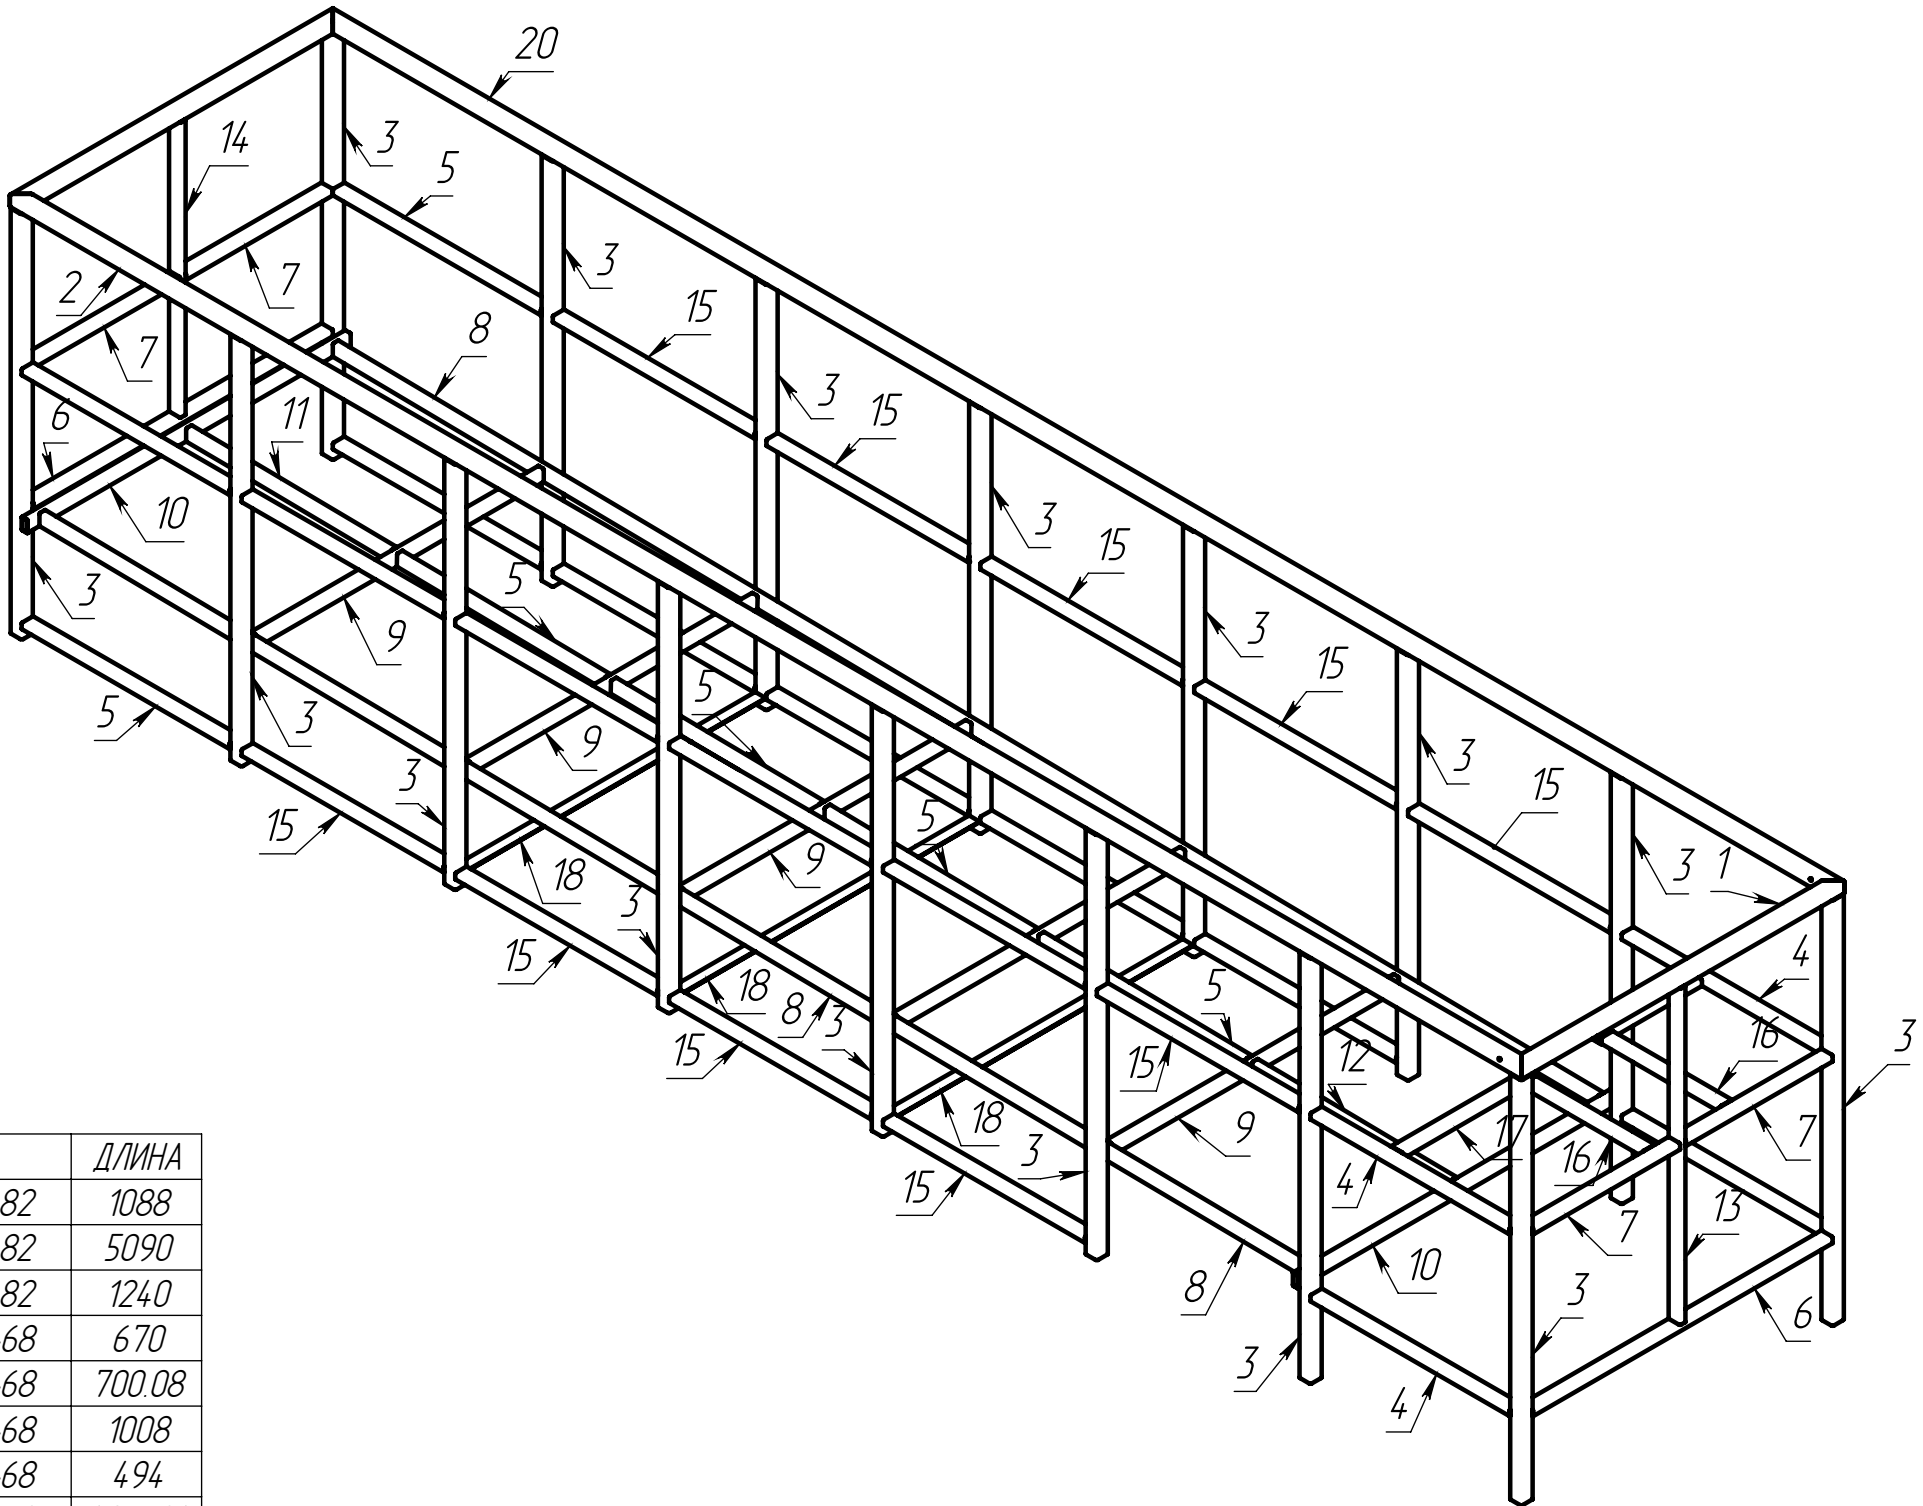

					ВРХИ.ВМ01.01.00.32					
					Рама (прав.)	Лит.		Масса	Масштаб	
Изм.	Лист	№ докум.	Подп.	Дата					192.66	1:18
Разраб.										
Пров.										
Т. контр.						Лист 1		Листов 10		
					Сварная конструкция <u>AISI 304</u>					
Н. контр.										
Утв.										

Перв. примен.		Справ. №		Подп. и дата		Инв. № дубл.		Взам. инв. №		Подп. и дата		Инв. № подл.	

ВРХИ.ВМ01.01.00.32

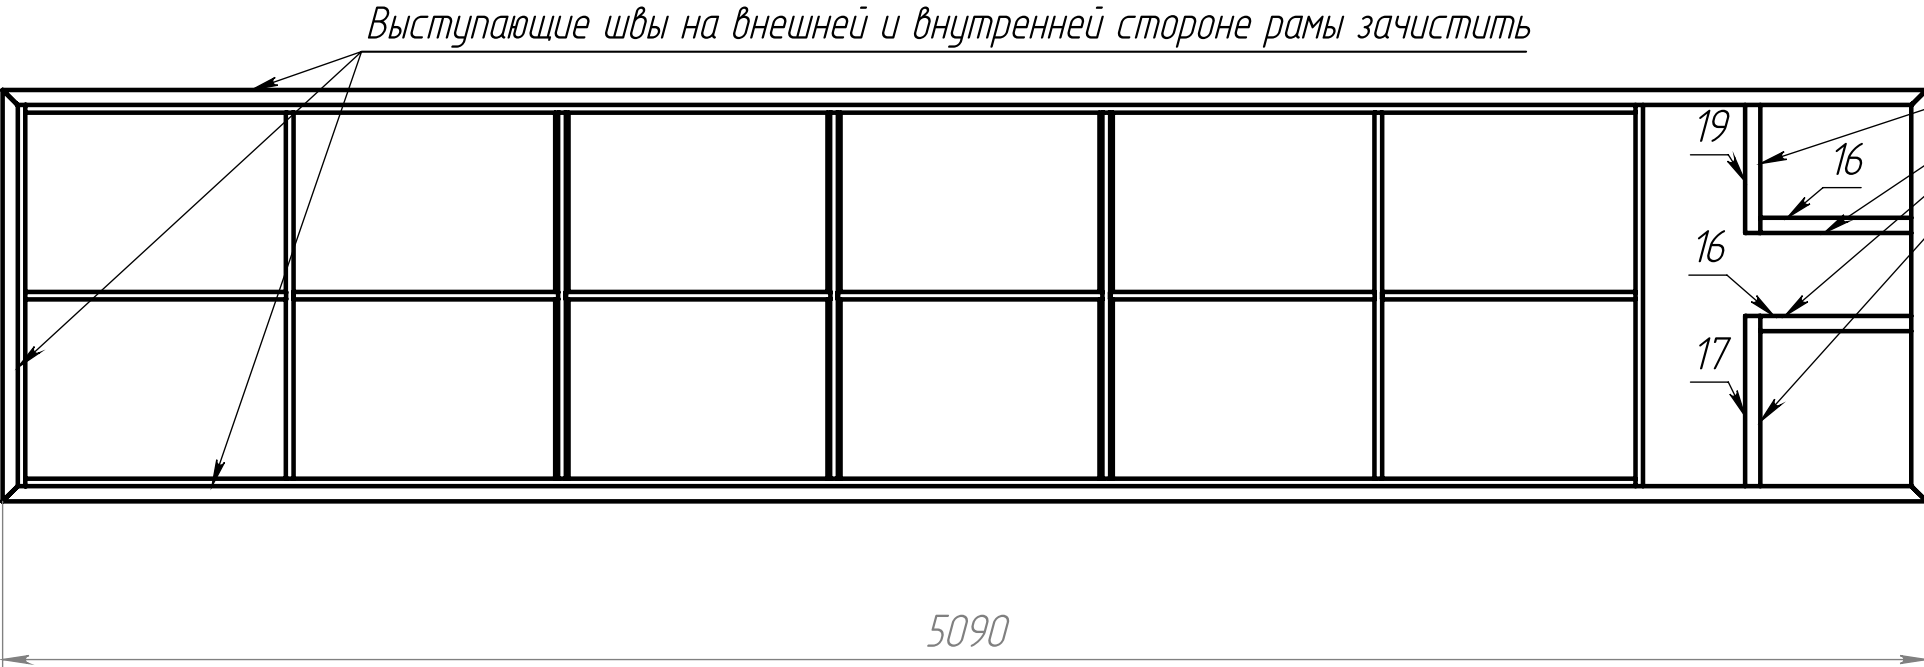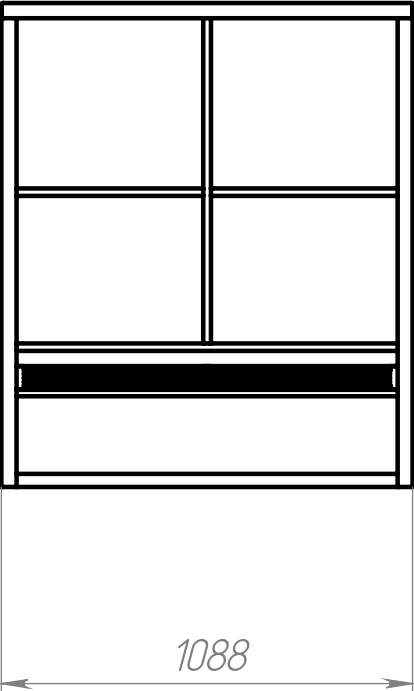


Привариваются после изготовления вкладыша

					ВРХИ.ВМ01.01.00.32						
					Рама (прав.)	Лит.			Масса	Масштаб	
Изм.	Лист	№ докум.	Подп.	Дата					192.66	1:20	
Разраб.											
Пров.											
Т. контр.											
						Лист 2			Листов 10		
					Сварная конструкция AISI 304						
Н. контр.											
Утв.											

Перв. примен.	
Справ. №	
Подп. и дата	Инв. № дубл.
Взам. инв. №	Инв. № подл.

ВРХИ.ВМ01.01.00.32

Расположение элементов длинных сторон рамы

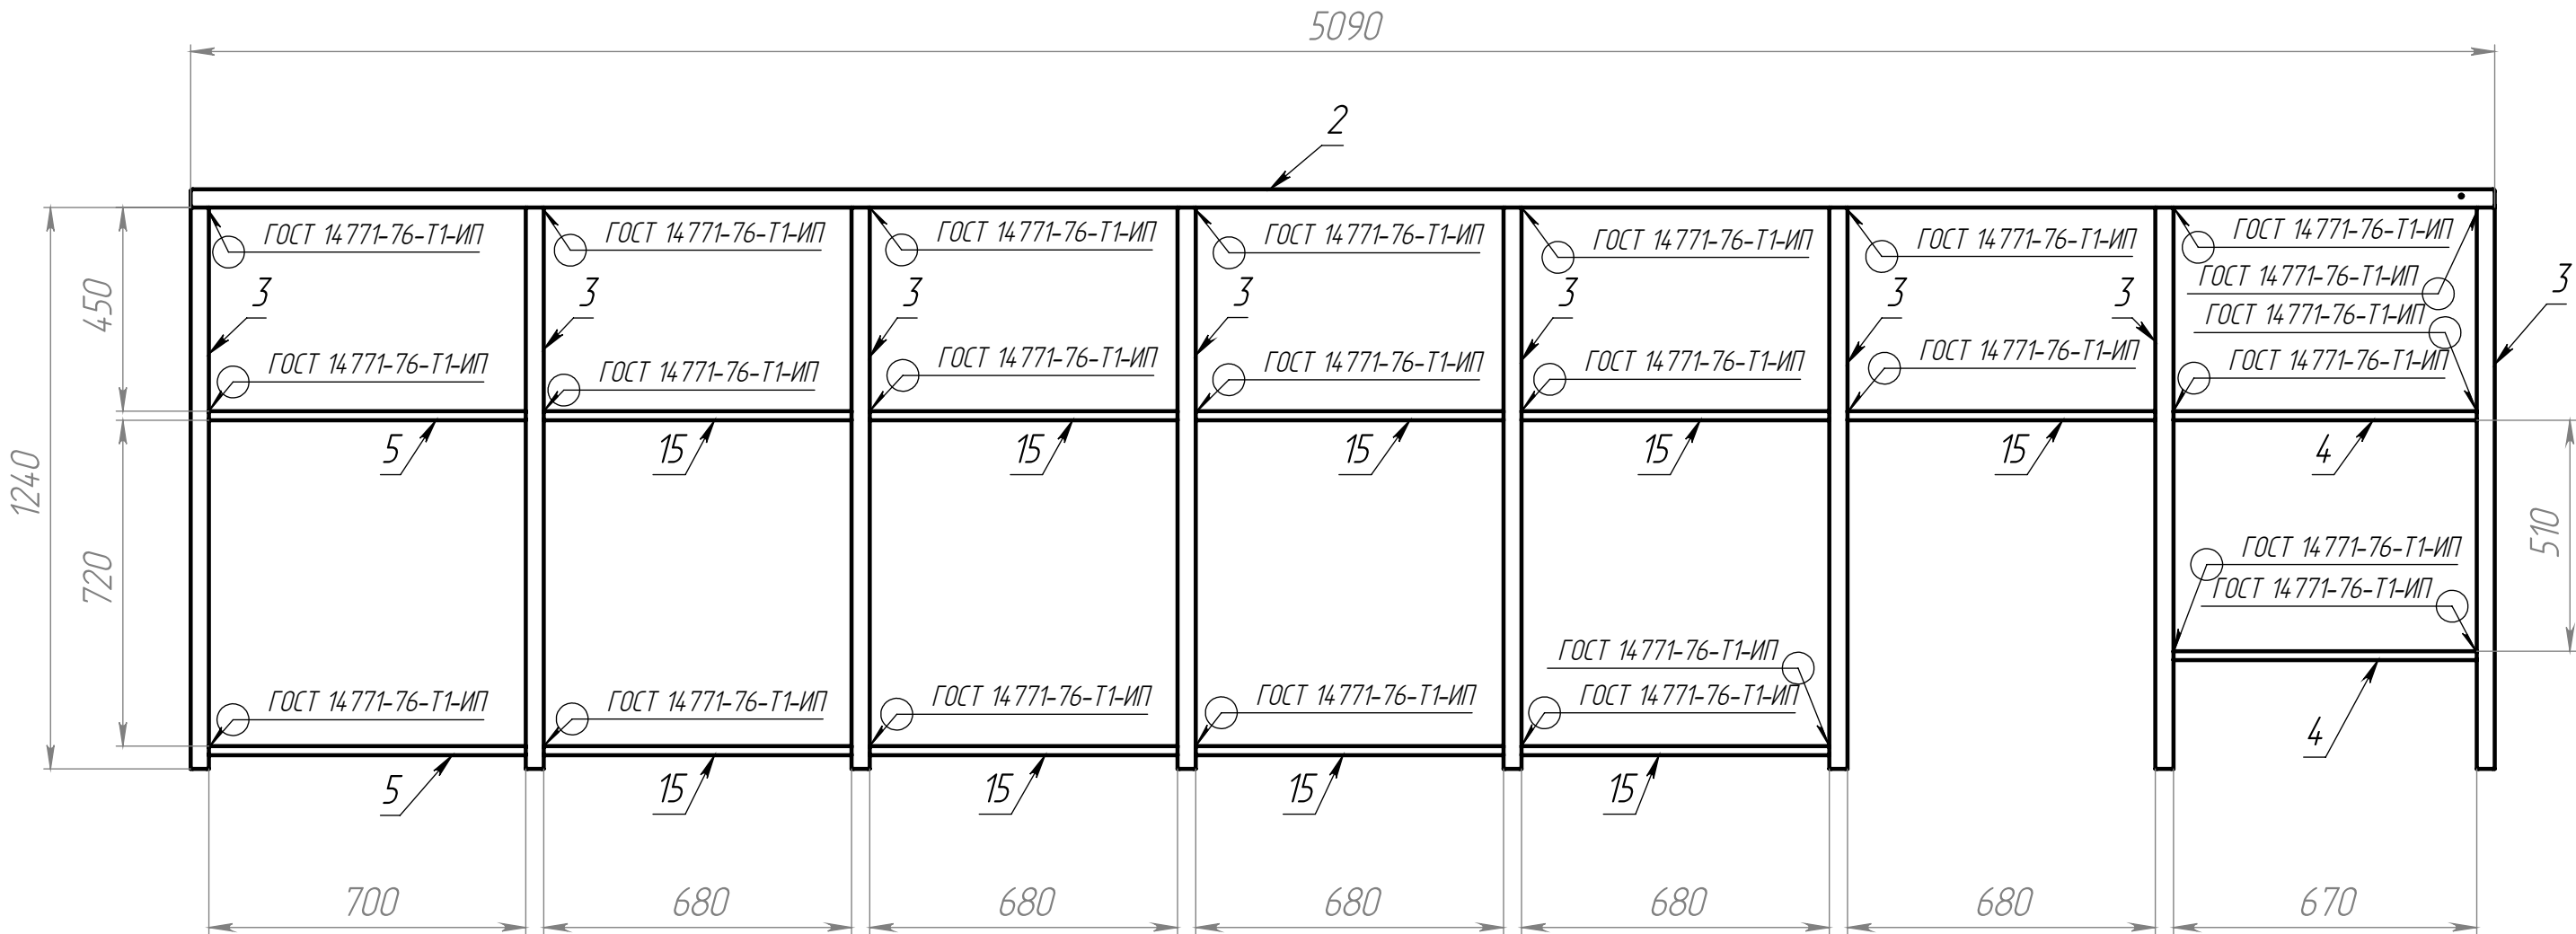


					ВРХИ.ВМ01.01.00.32				
					Рама (прав.)	Лит.		Масса	Масштаб
Изм.	Лист	№ докум.	Подп.	Дата				192.66	1:15
Разраб.									
Пров.									
Т. контр.						Лист 3		Листов 10	
					Сварная конструкция AISI 304				
Н. контр.									
Утв.									

Перв. примен.		Справ. №		Подп. и дата		Инв. № дубл.		Взам. инв. №		Подп. и дата		Инв. № подл.	

ВРХИ.ВМ01.01.00.32


Вид слева

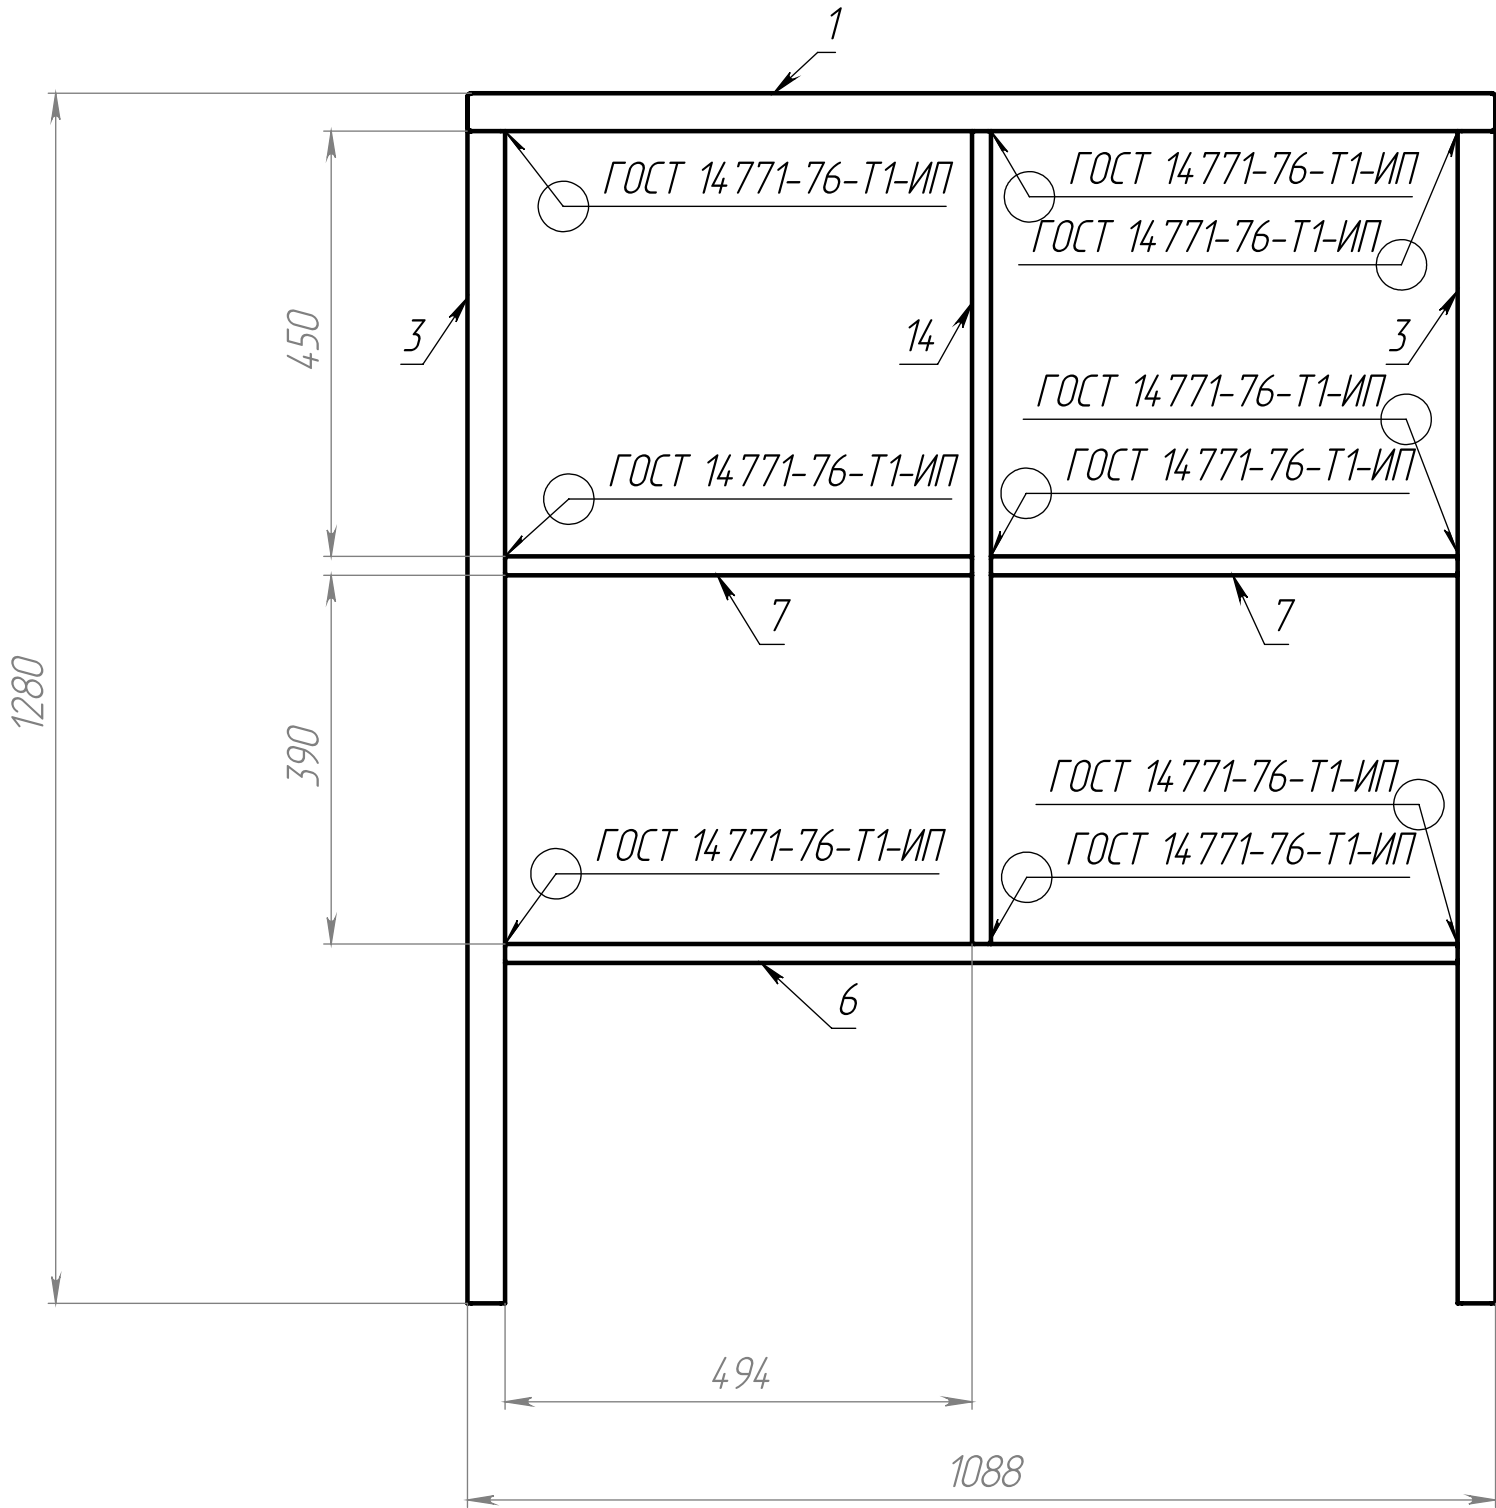

					ВРХИ.ВМ01.01.00.32				
					Рама (прав.)	Лит.		Масса	Масштаб
Изм.	Лист	№ докум.	Подп.	Дата				192.66	1:8
Разраб.									
Пров.									
Т. контр.						Лист 4		Листов 10	
					Сварная конструкция AISI 304				
Н. контр.									
Утв.									

Инв. № подл.	Подп. и дата	Взам. инв. №	Инв. № дубл.	Подп. и дата	Справ. №	Перв. примен.

ВРХИ.ВМ01.01.00.32

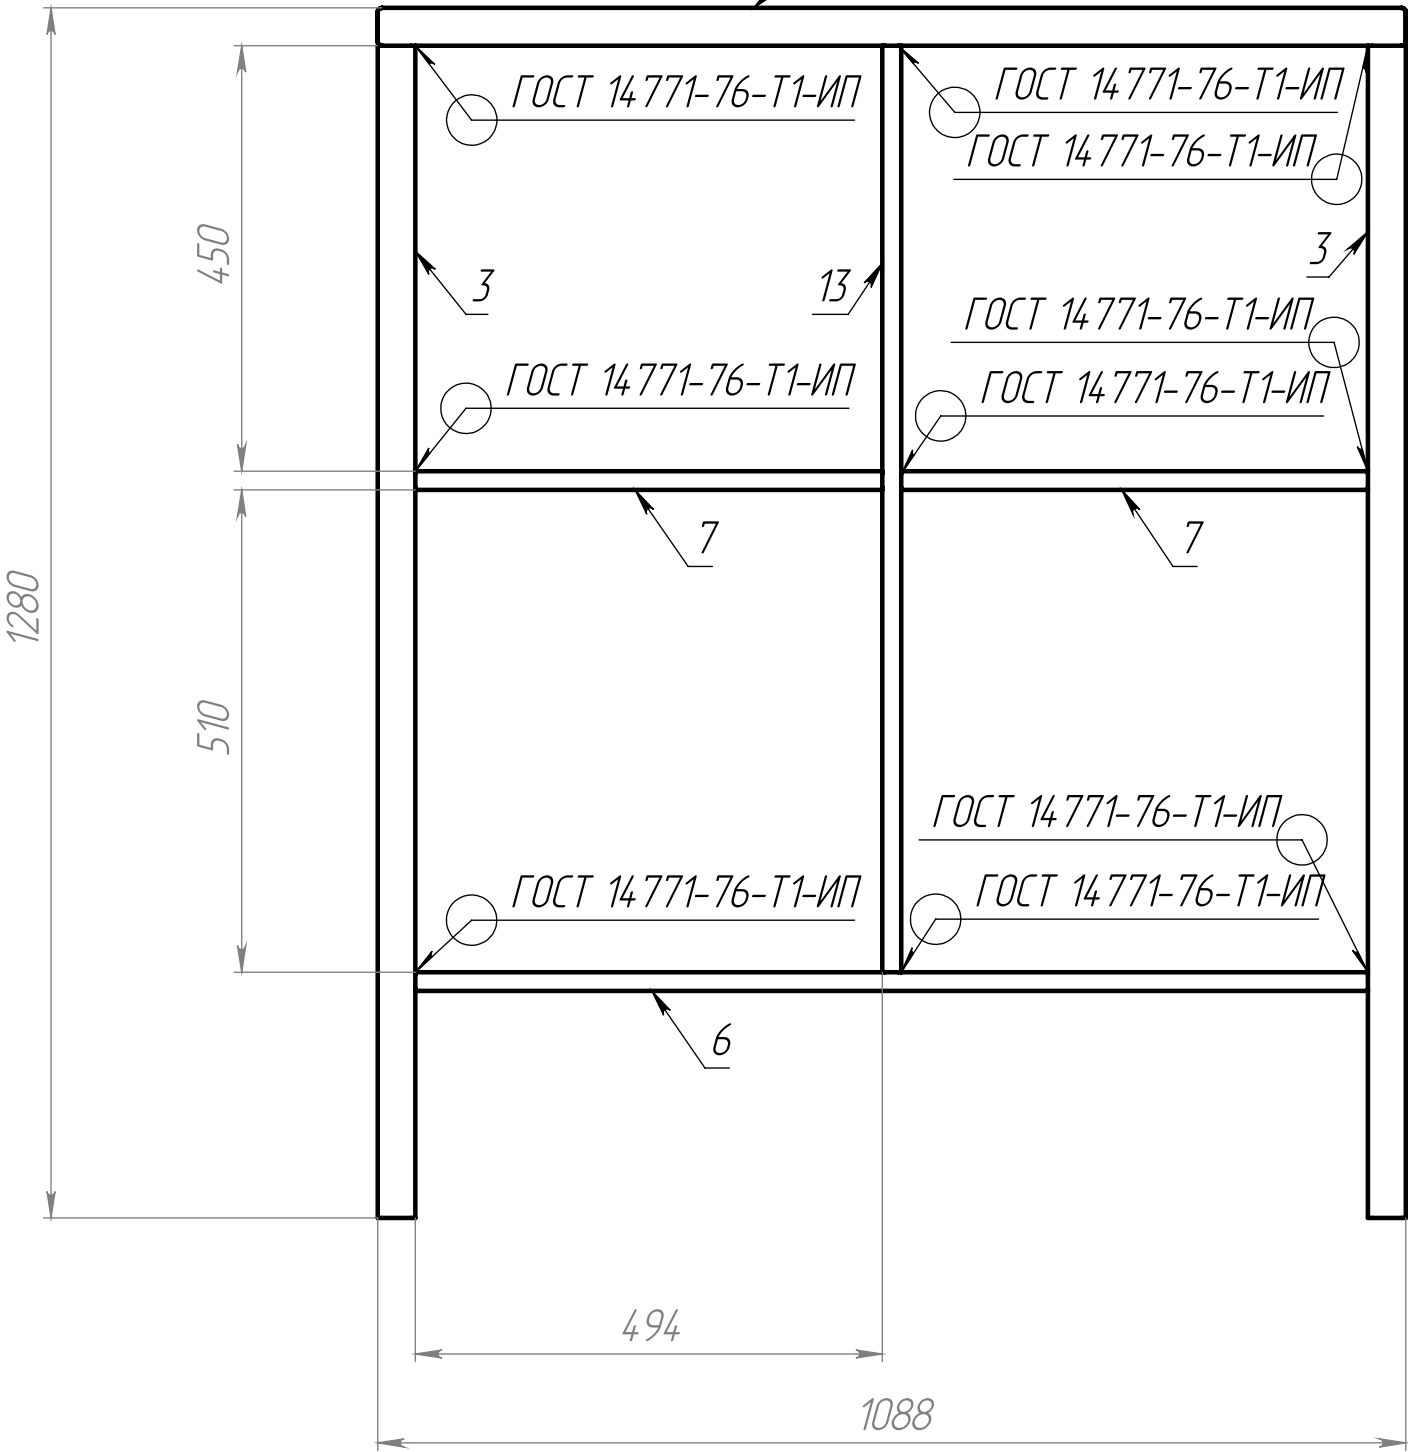





					ВРХИ.ВМ01.01.00.32				
					Рама (прав.)	Лит.		Масса	Масштаб
Изм.	Лист	№ докум.	Подп.	Дата					
Разраб.								192.66	1:8
Пров.									
Т. контр.						Лист 5		Листов 10	
Н. контр.					Сварная конструкция	АISI 304			
Утв.									

BPXN.BM01.01.00.32



Расположение элементов дна

$A(1:10)$


B (1 : 10)

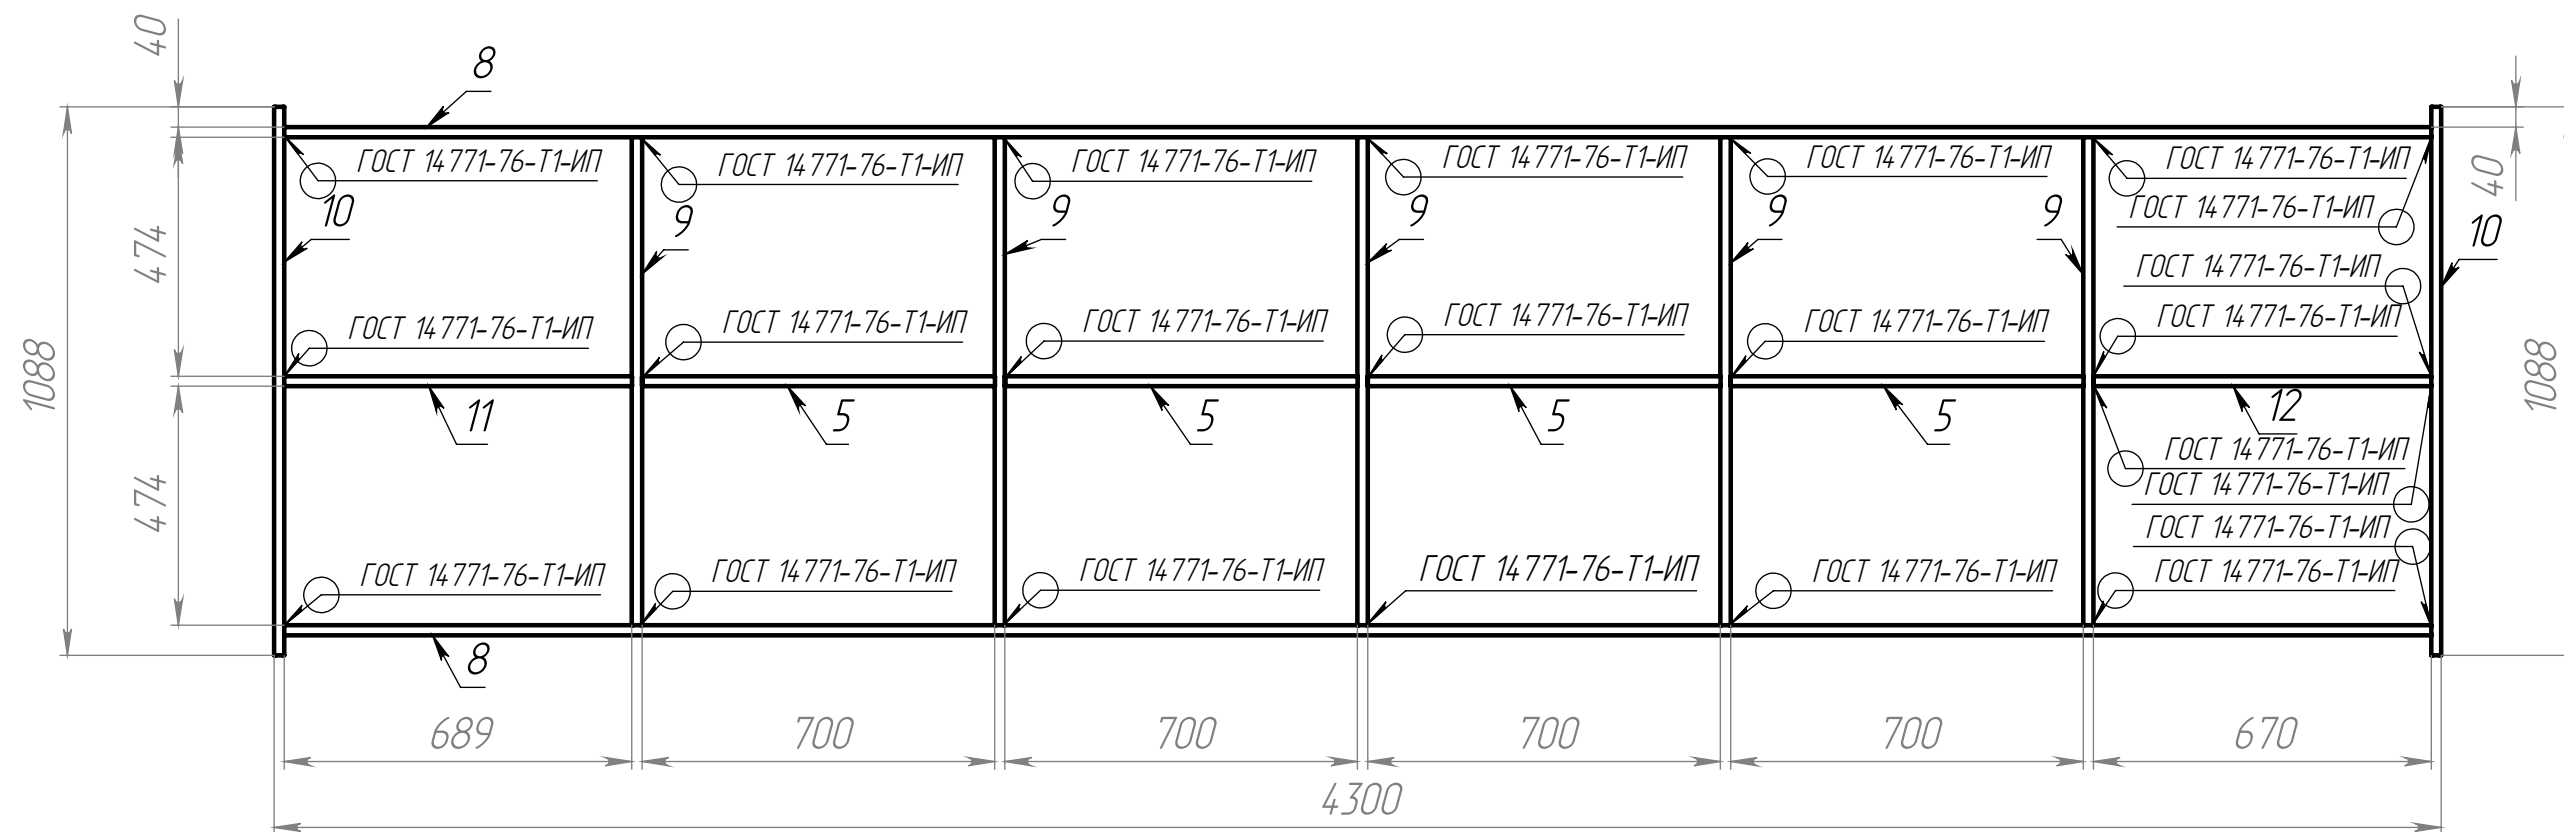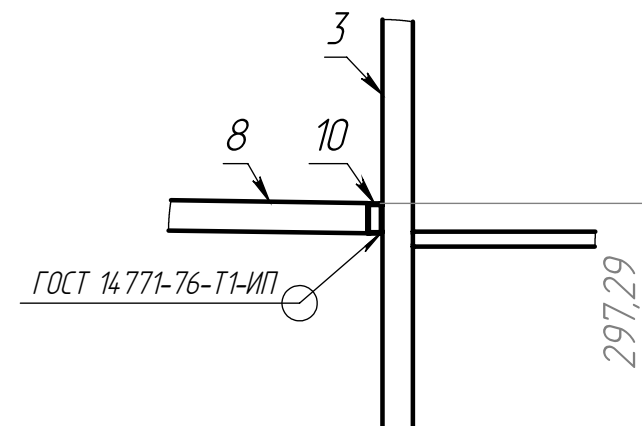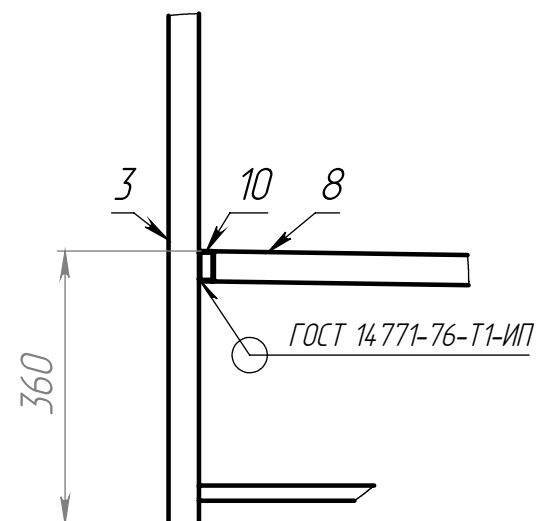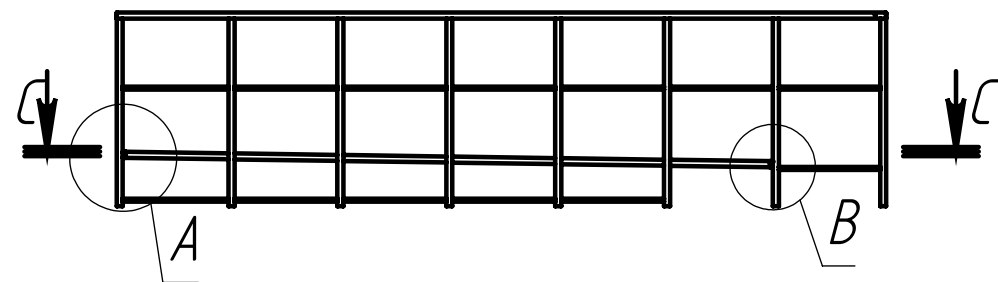


$D (1 : 10)$

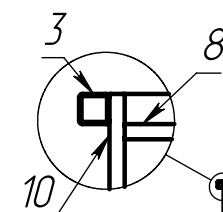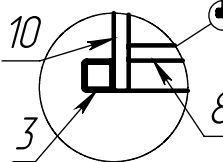 $E(1:10)$ 

C-C (1:50)

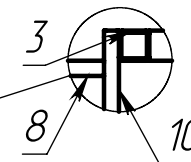 $F(1:10)$ 


G (1 : 10)

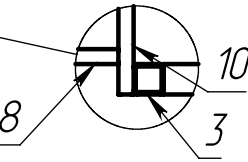



					ВРХИ.ВМ01.01.00.32											
					Рама (прав.)					Лит.		Масса	Масштаб			
															192.66	1:15
Изм.	Лист	№ докум.	Подп.	Дата												
Разраб.																
Пров.																
Т. контр.										Лист 6		Листов 10				
					Сварная конструкция AISI 304											
Н. контр.																
Утв.																

Перв. примен.	
Справ. №	
Подп. и дата	
Инв. № дубл.	
Взам. инв. №	
Подп. и дата	
Инв. № подл.	

ВРХИ.ВМ01.01.00.32

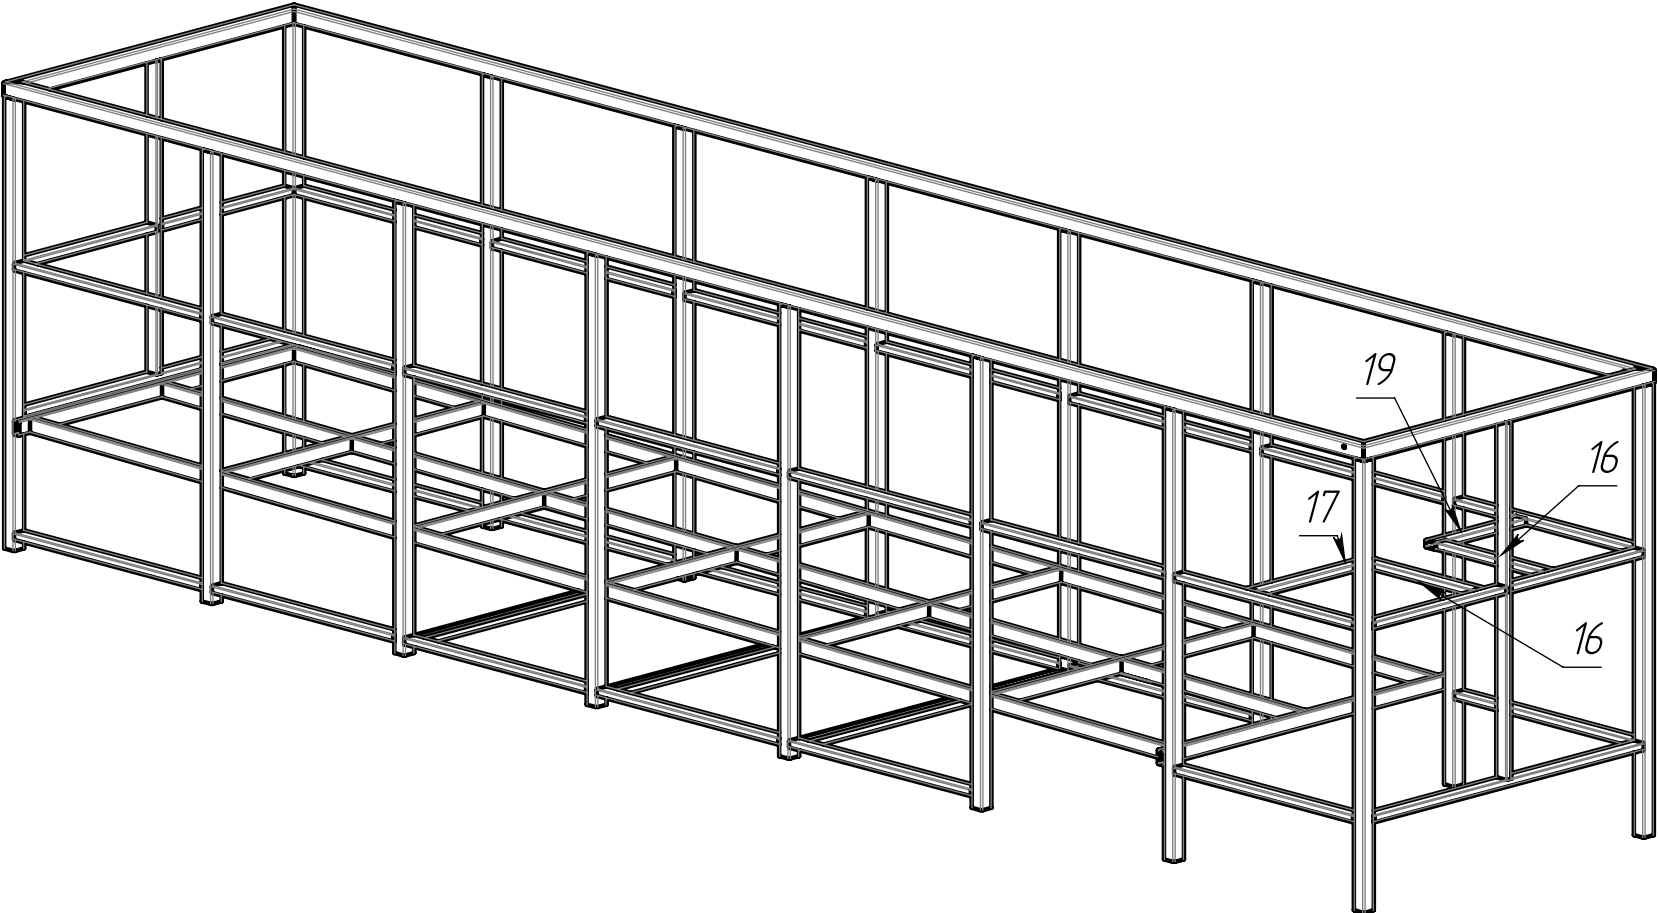

Вид сверху

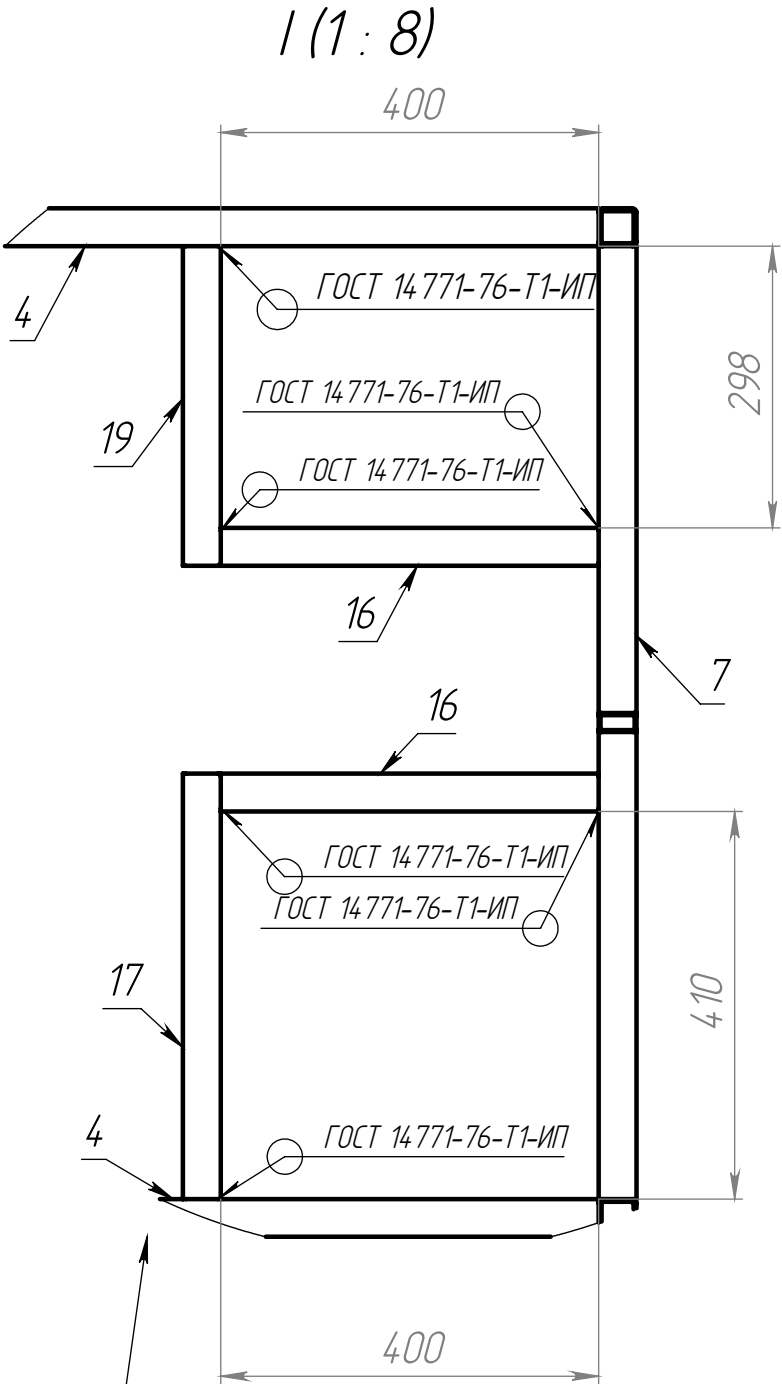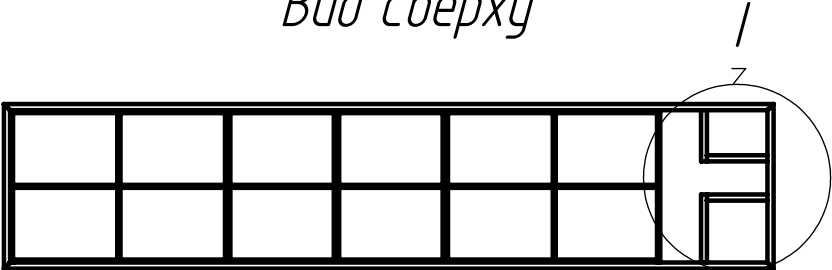

Верхний пояс из проф. трубы 40х40 не отображен

Поз.16 и поз.17 привариваются после установки вкладыша

					ВРХИ.ВМ01.01.00.32						
					Рама (прав.)	Лит.			Масса	Масштаб	
Изм.	Лист	№ докум.	Подп.	Дата					192.66	1:50	
Разраб.											
Пров.											
Т. контр.											
						Лист 7			Листов 10		
Н. контр.					Сварная конструкция	АISI 304					
Утв.											

