


Перв. примен.

Справ. №

ВРХИ.ВМ.01.32 СБ

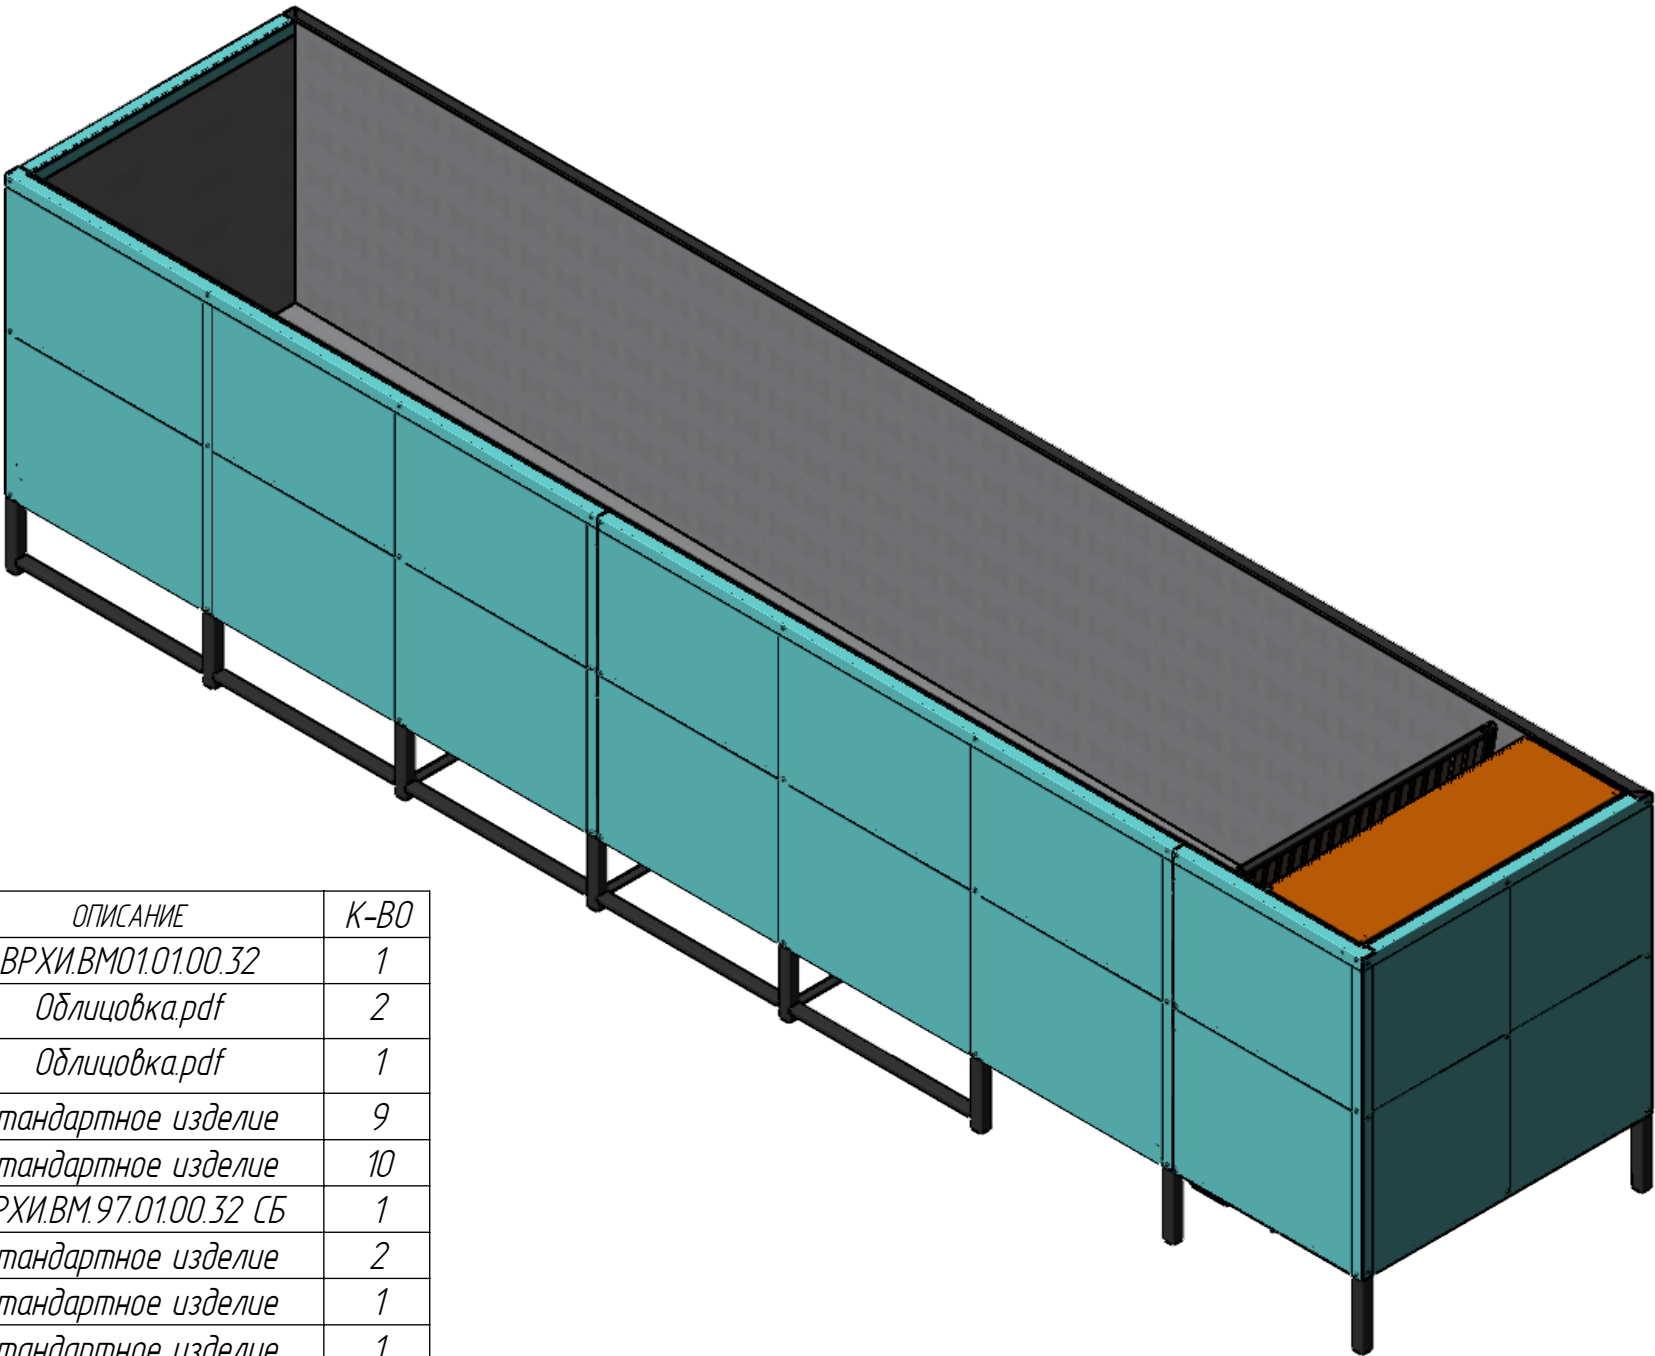

Поз.	ОБОЗНАЧЕНИЕ	ОПИСАНИЕ	К-ВО
1	Рама (прав.)	ВРХИ.ВМ01.01.00.32	1
2	Проставка боковая	Облицовка.pdf	2
3	Проставка торцевая	Облицовка.pdf	1
4	Закlepка 4,8x12 AISI304	Стандартное изделие	9
5	Закlepка 4,8x16 AISI304	Стандартное изделие	10
6	Вкладыш (прав.)	ВРХИ.ВМ.97.01.00.32 СБ	1
7	Отвод D110x45	Стандартное изделие	2
8	Вывод рыбoводный	Стандартное изделие	1
9	Труба канализационная наружная D160	Стандартное изделие	1
10	Хомут D110	Стандартное изделие	1
11	Шпилька M8	Стандартное изделие	1
12	Шайба А.8 ГОСТ 6958-78	Стандартное изделие	2
13	Гайка M8 ГОСТ 5915-70	Стандартное изделие	2
14	Отвод 160x45	Стандартное изделие	1
15	Полка малая	ВРХИ.ВМ80.01.00.32	1
16	Полка большая	ВРХИ.ВМ80.02.00.32	1
17	Удлинитель тяги шибера сварной (тип к)	ВРХИ.ВМ.94.02.00.32 СБ	1
18	Удлинитель тяги шибера сварной (тип р)	ВРХИ.ВМ.94.01.00.32 СБ	1
19	Облицовка (прав.)	Облицовка.pdf	1
20	Крышка отсека в сборе	ВРХИ.ВМ.96.01.00.32 СБ	1
21	Решетка	ВРХИ.ВМ.95.01.00.32 СБ	1
22	Шибер с раструбом	см. Шибер с трубами - рекомендации.pdf	1
23	Шибер без раструбов	см. Шибер с трубами - рекомендации.pdf	1

Подп. и дата

Инв. № дубл.

Взам. инв. №

Подп. и дата

Инв. № подл.

ВРХИ.ВМ.01.32 СБ

Ванна

Сборочная единица

Лит.

Масса

Масштаб

393.98

1:20

Лист 1

Листов 10

Изм.

Лист

№ докум.

Подп.

Дата

Разраб.

Пров.

Т. контр.

Н. контр.

Утв.

1


Копировал

Формат А3

Файл: Схема (порядок сборки)

Перв. примен.	Справ. №	Подп. и дата	Инв. № дубл.	Взам. инв. №	Подп. и дата	Инв. № подл.



ВРХИ.ВМ.01.32 СБ

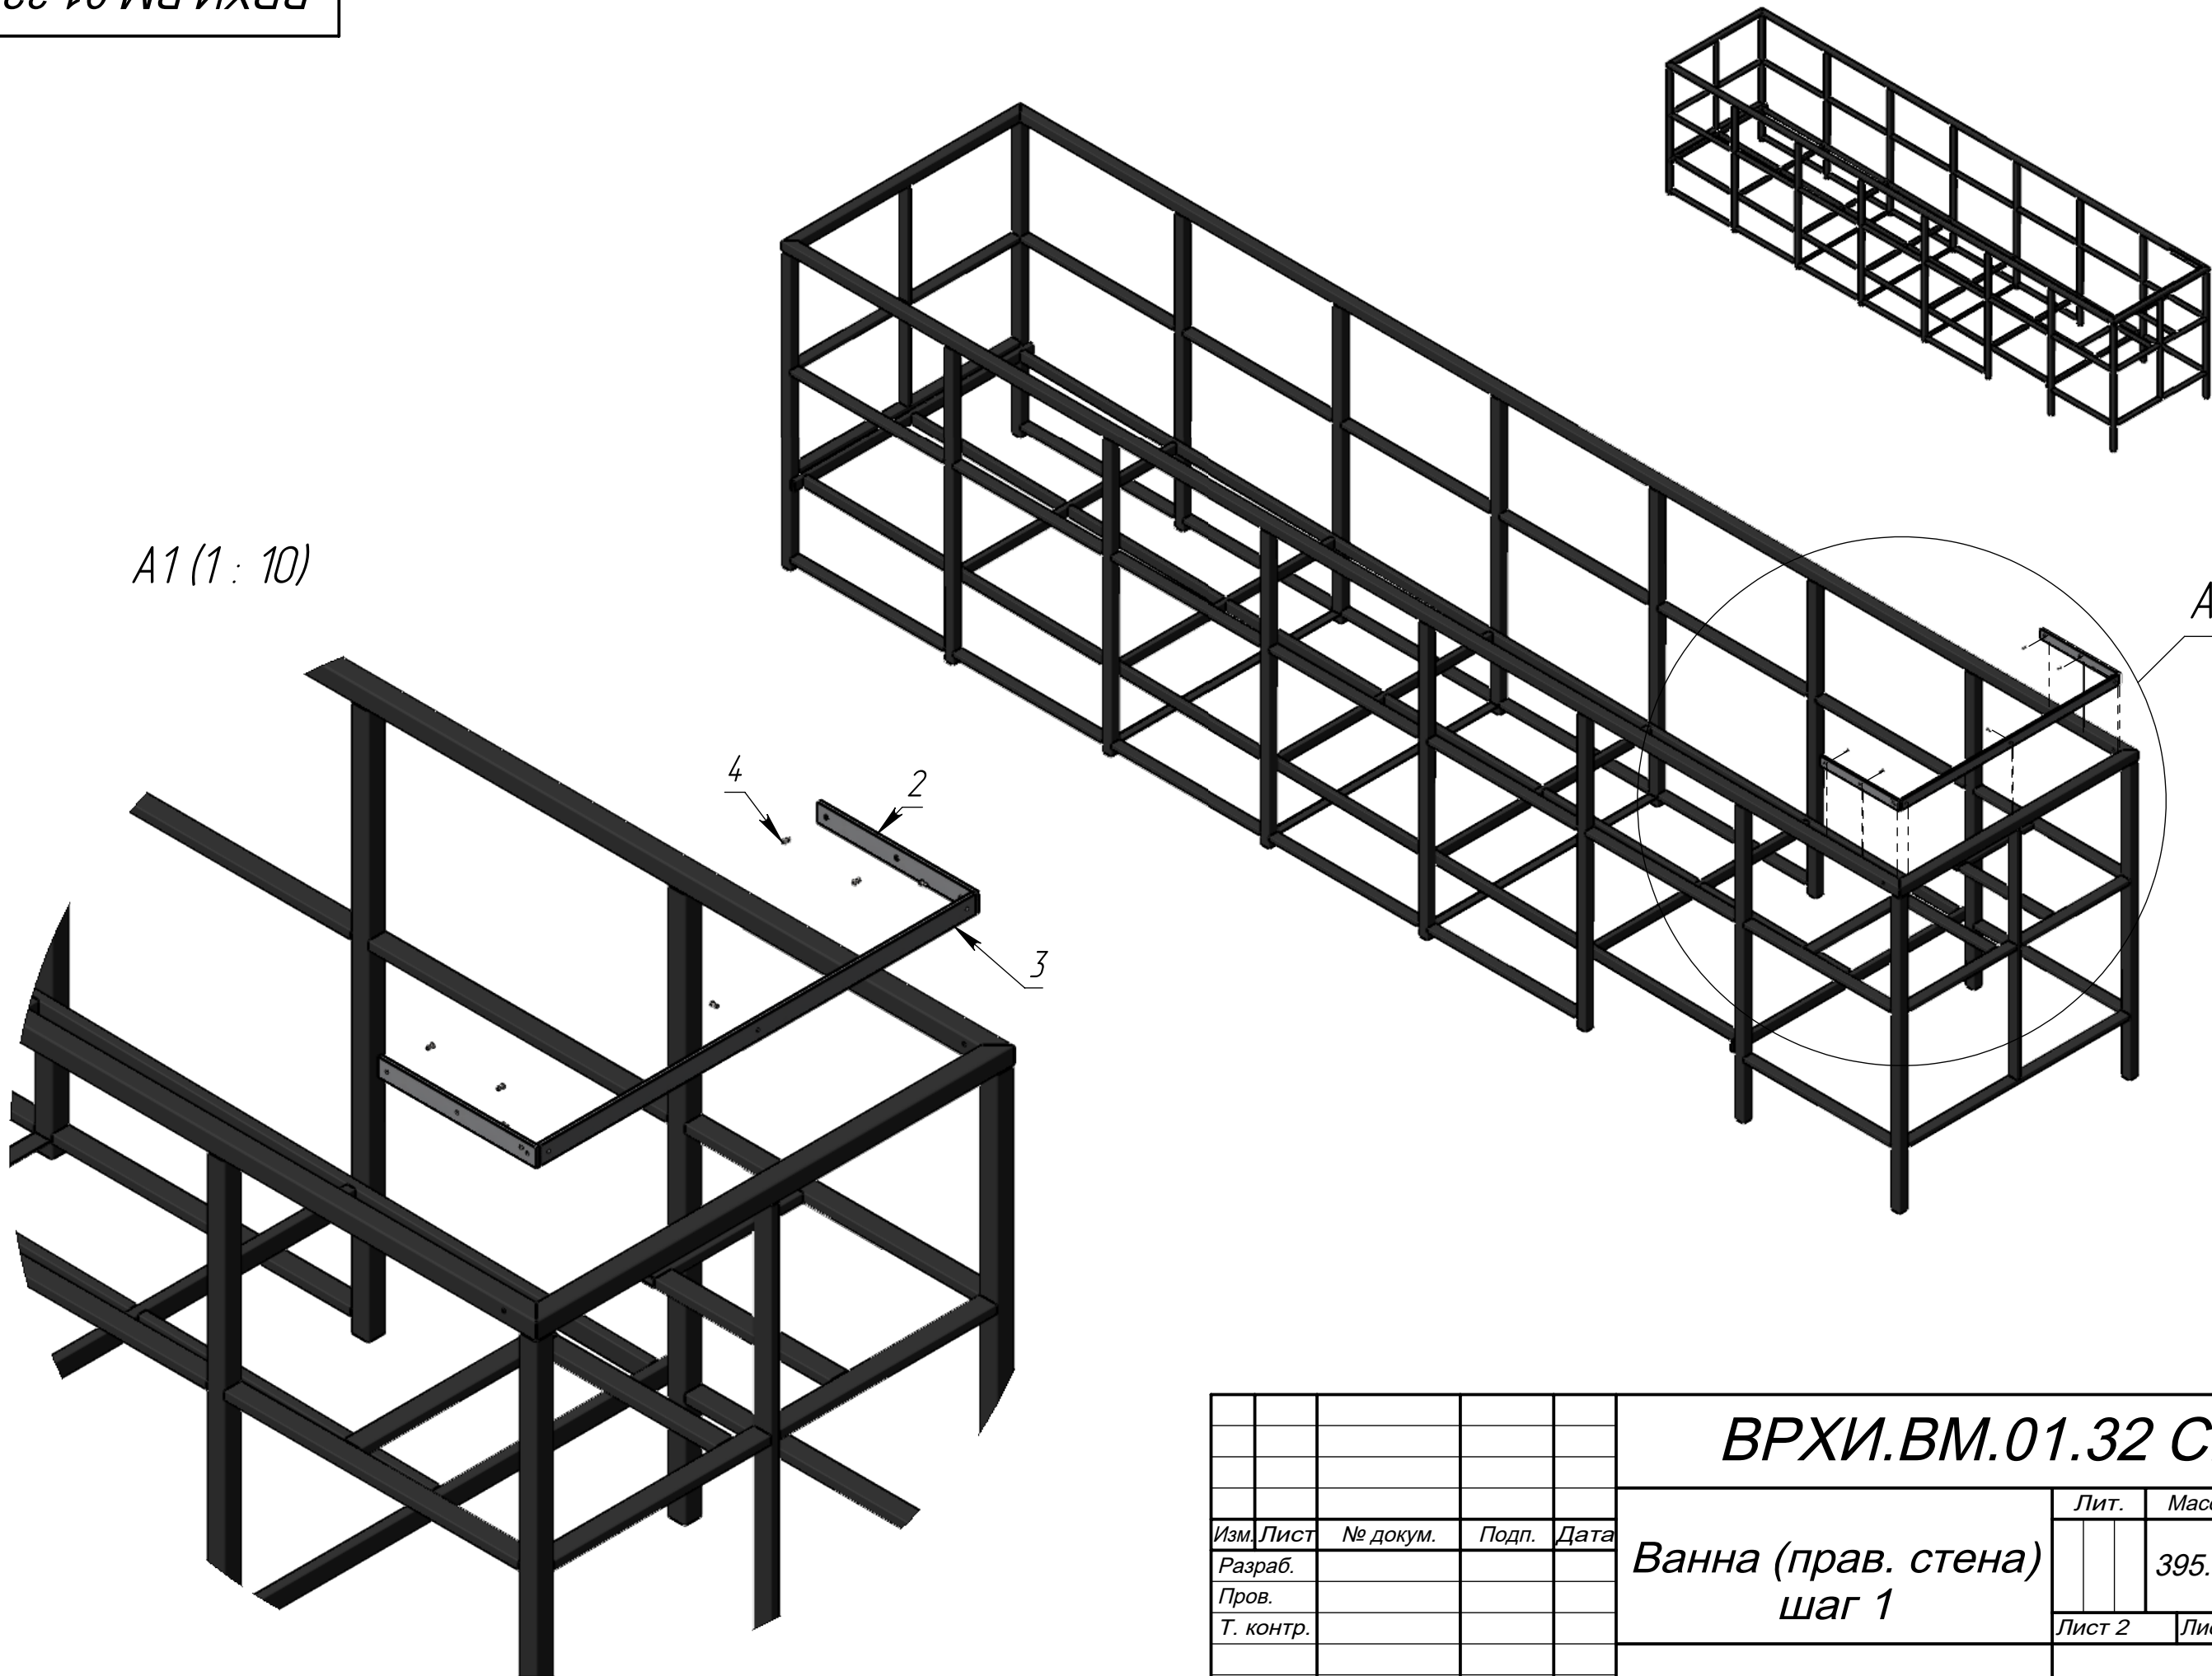


					ВРХИ.ВМ.01.32 СБ				
					Ванна (прав. стена) шаг 1	Лит.		Масса	Масштаб
Изм.	Лист	№ докум.	Подп.	Дата				395.38	1:20
Разраб.									
Пров.									
						Лист 2		Листов 10	
					Сборочная единица				
Н. контр.									
Утв.									

Перв. примен.	Справ. №	Подп. и дата	Инв. № дубл.	Взам. инв. №	Подп. и дата	Инв. № подл.

ВРХИ.ВМ.01.32 СБ

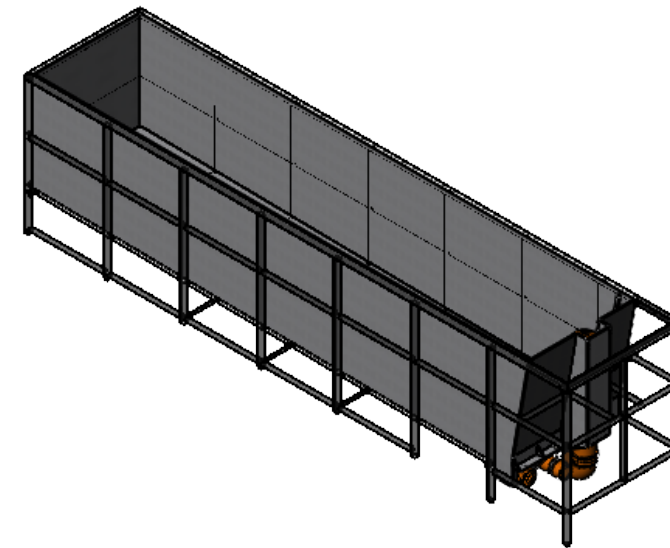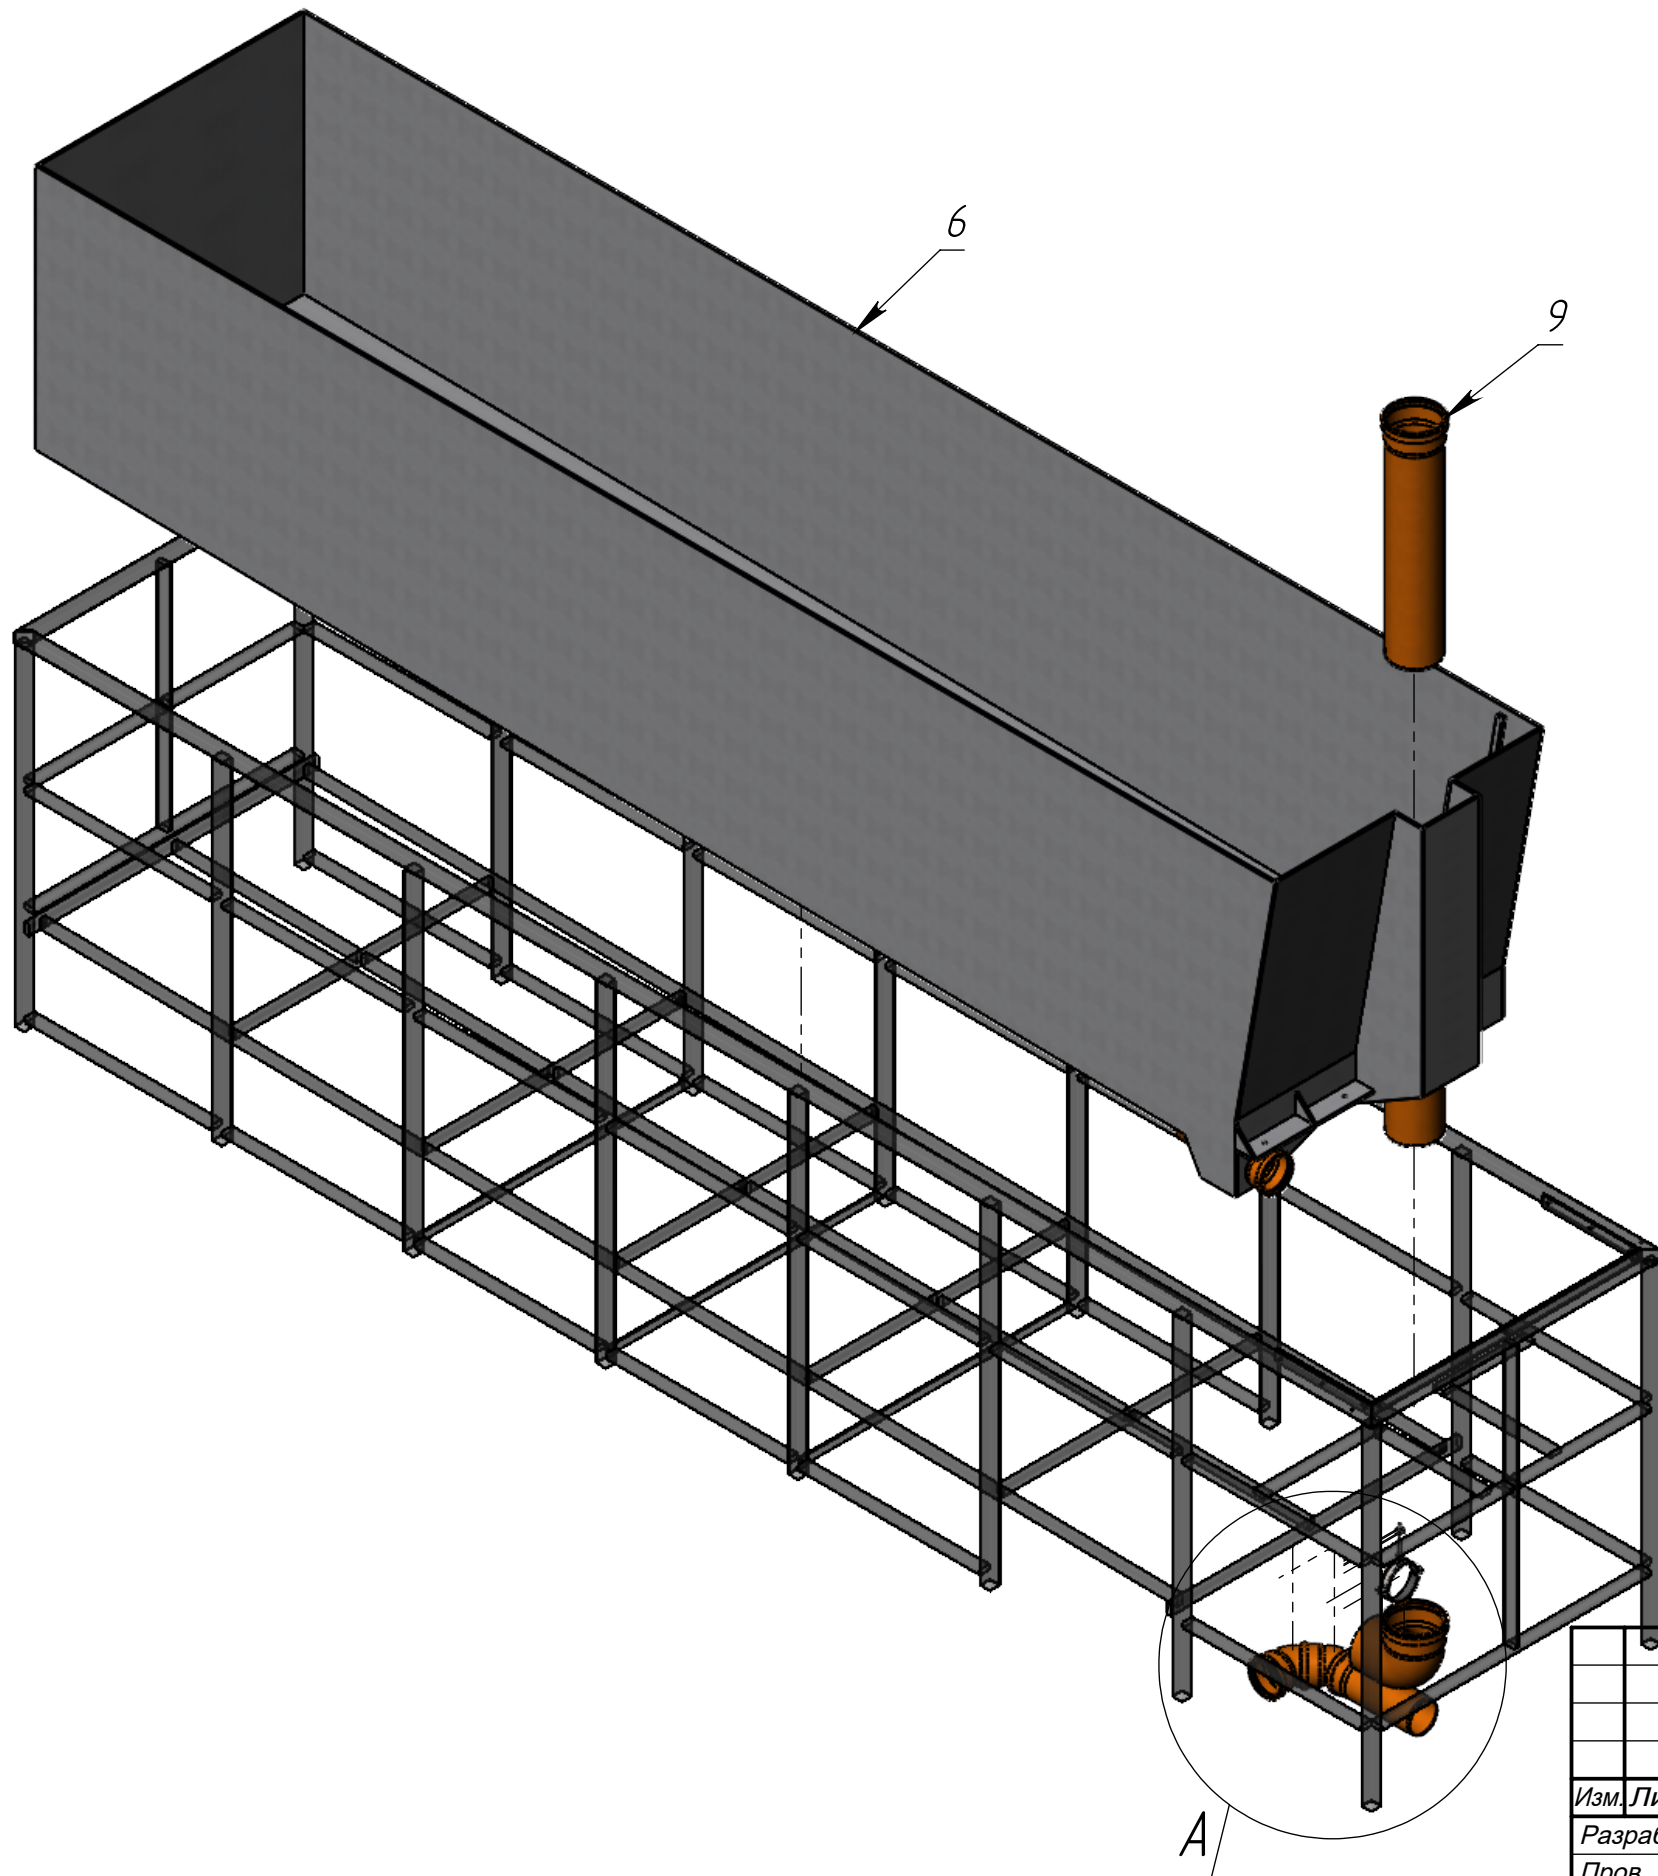



A (1 : 10)

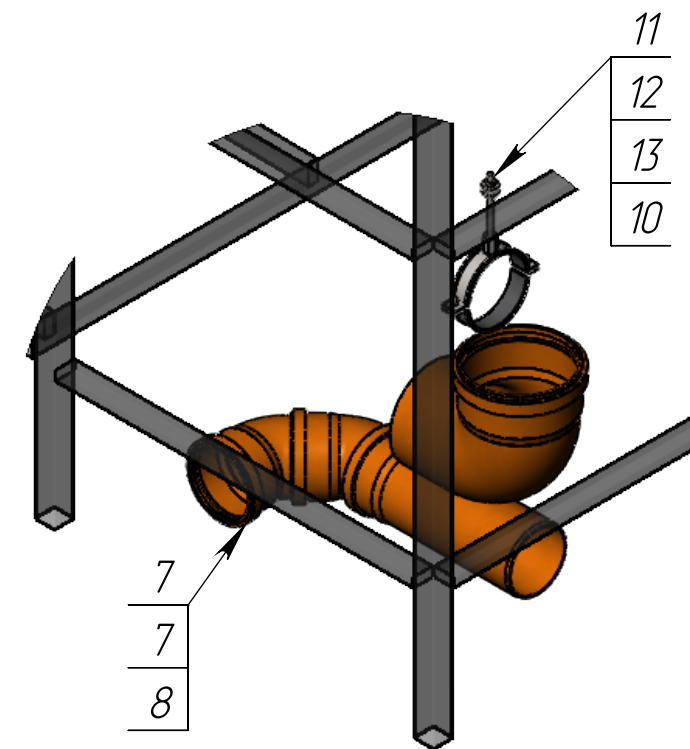


				ВРХИ.ВМ.01.32 СБ		
				Ванна (прав. стена) шаг 2		
				Лит.	Масса	Масштаб
					395.38	1:50
				Лист 3		Листов 10
				Сборочная единица		
Изм.	Лист	№ докум.	Подп.	Дата		
Разраб.						
Пров.						
Т. контр.						
Н. контр.						
Утв.						

Перв. примен.		Справ. №		Подп. и дата		Инв. № дубл.		Взам. инв. №		Подп. и дата		Инв. № подл.	

ВРХИ.ВМ.01.32 СБ

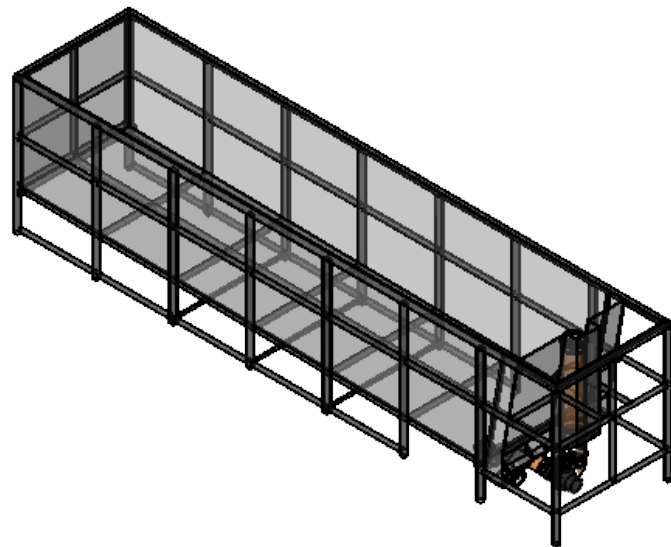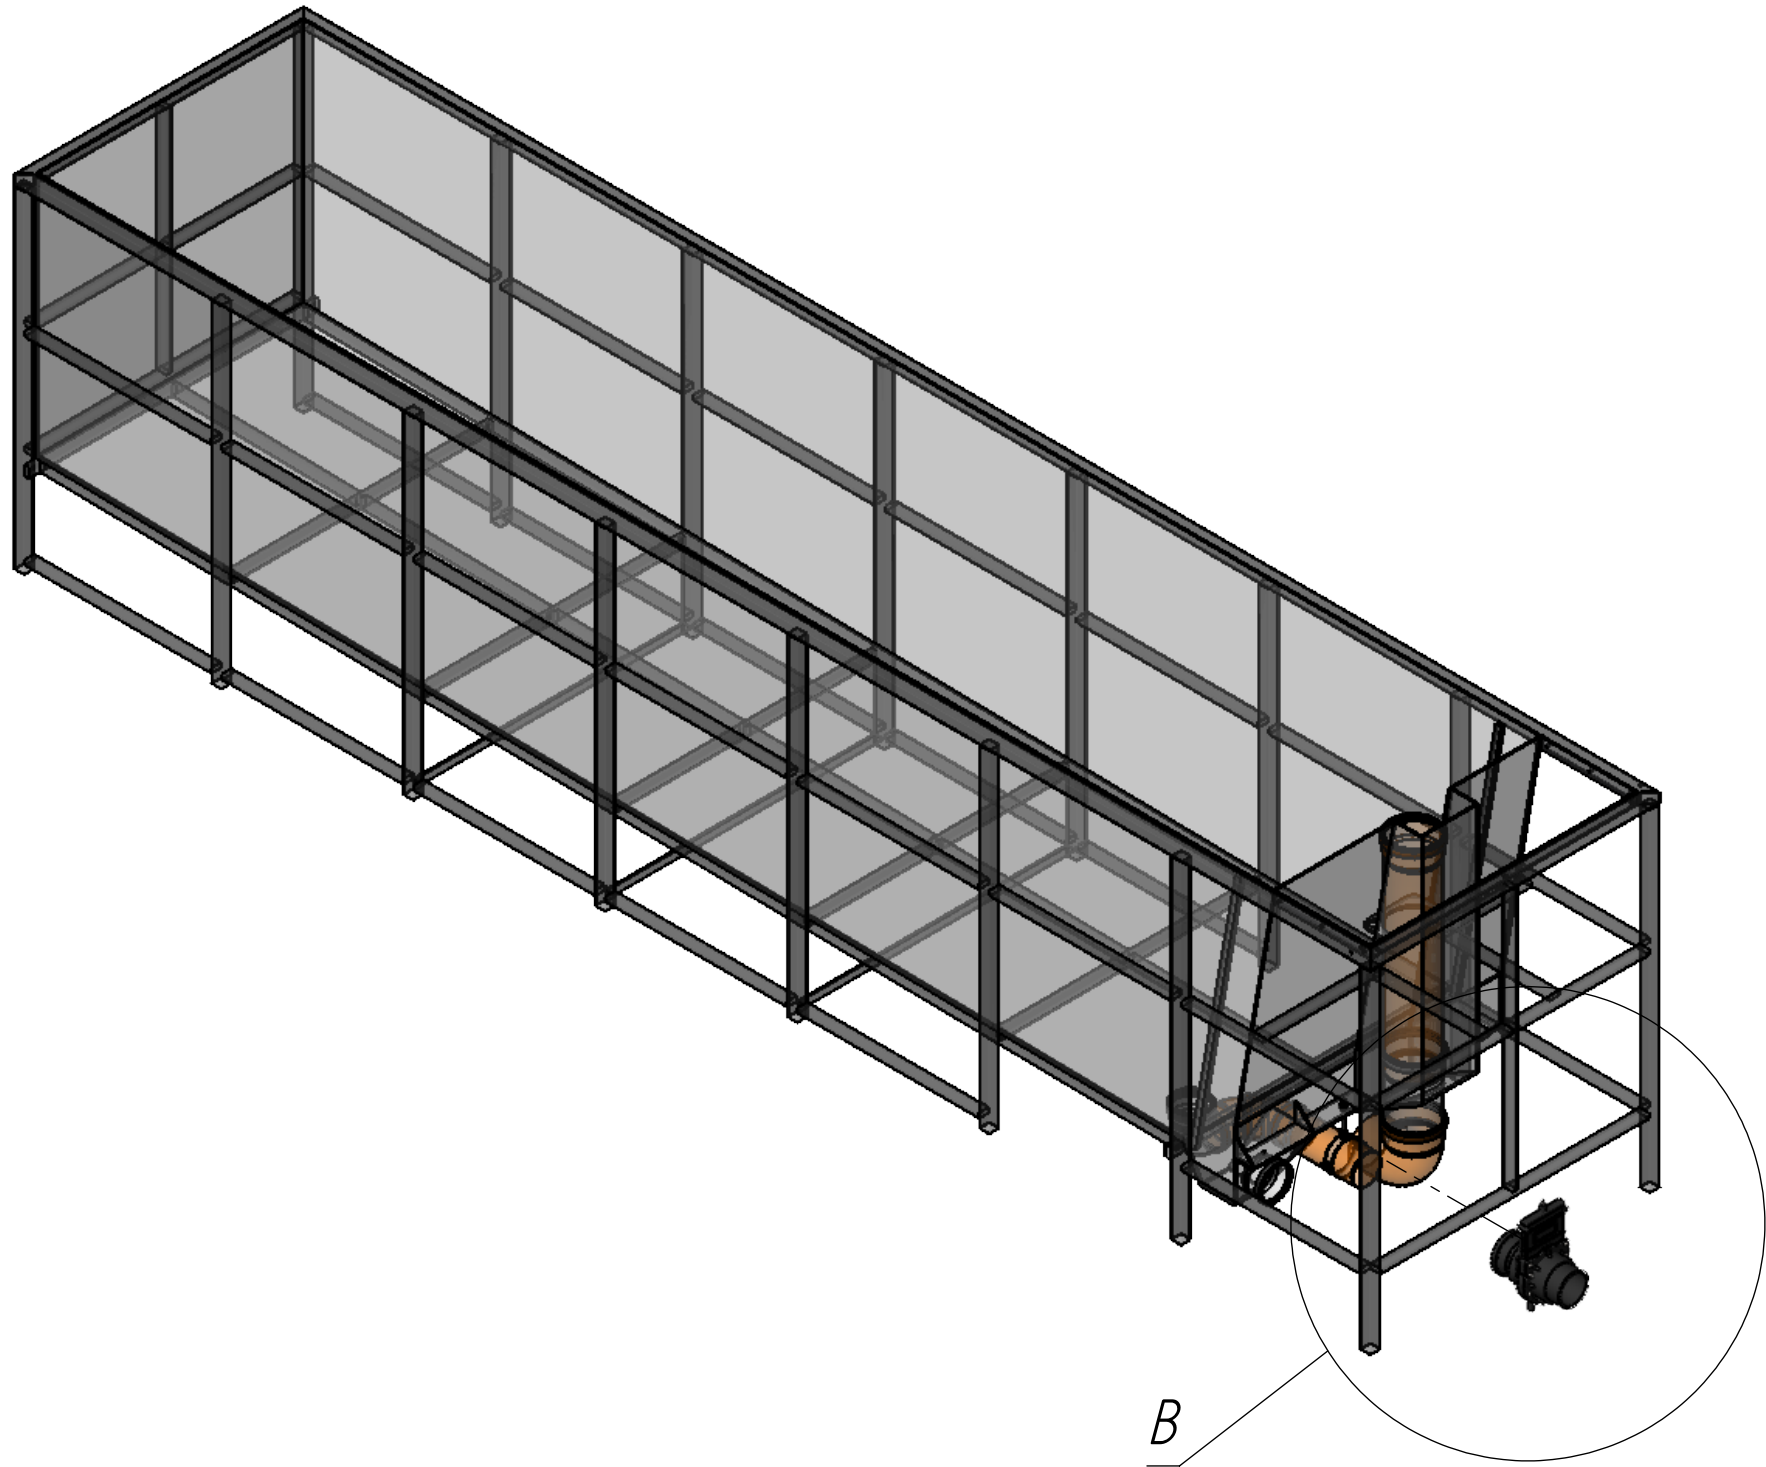



В (1 : 10)

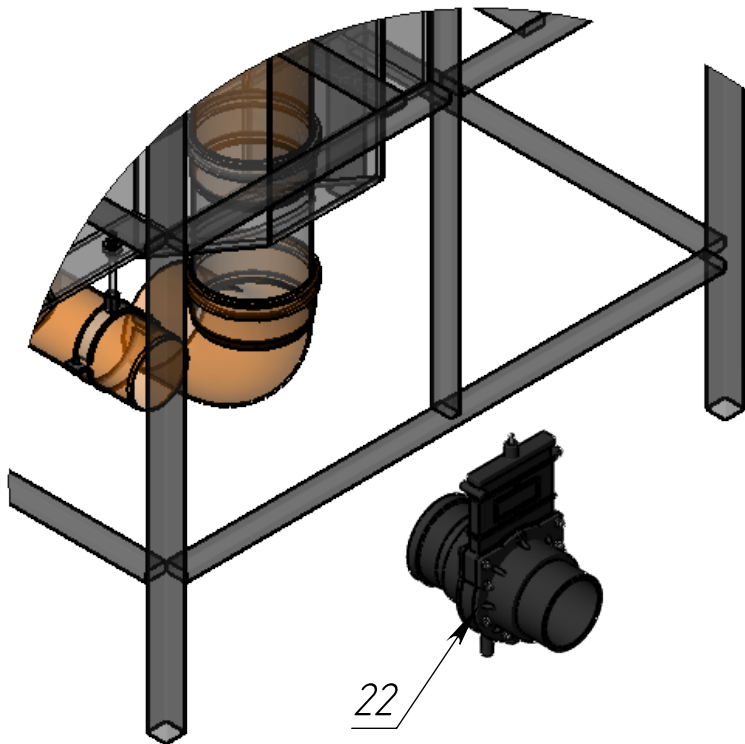


					ВРХИ.ВМ.01.32 СБ		
					Ванна (прав. стена) шаг 3		
					Лит.	Масса	Масштаб
						394.63	1:50
					Лист 4		Листов 10
					Сборочная единица		
Изм.	Лист	№ докум.	Подп.	Дата			
Разраб.							
Пров.							
Т. контр.							
Н. контр.							
Утв.							

Перв. примен.	Справ. №	Подп. и дата	Инв. № дубл.	Взам. инв. №	Подп. и дата	Инв. № подл.

ВРХИ.ВМ.01.32 СБ

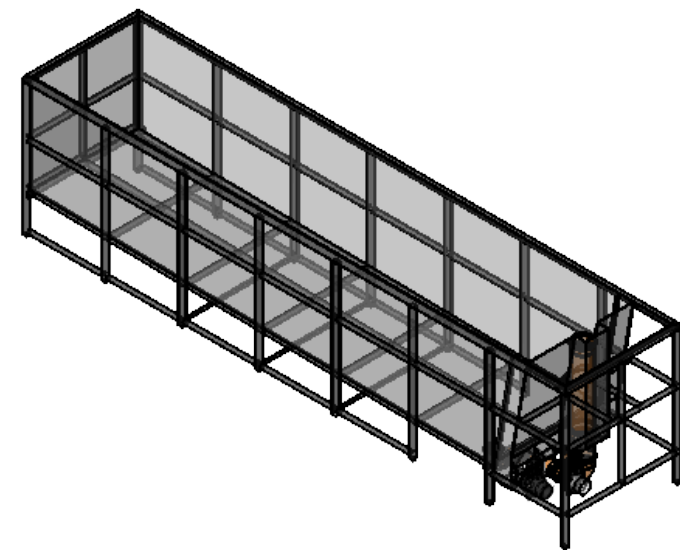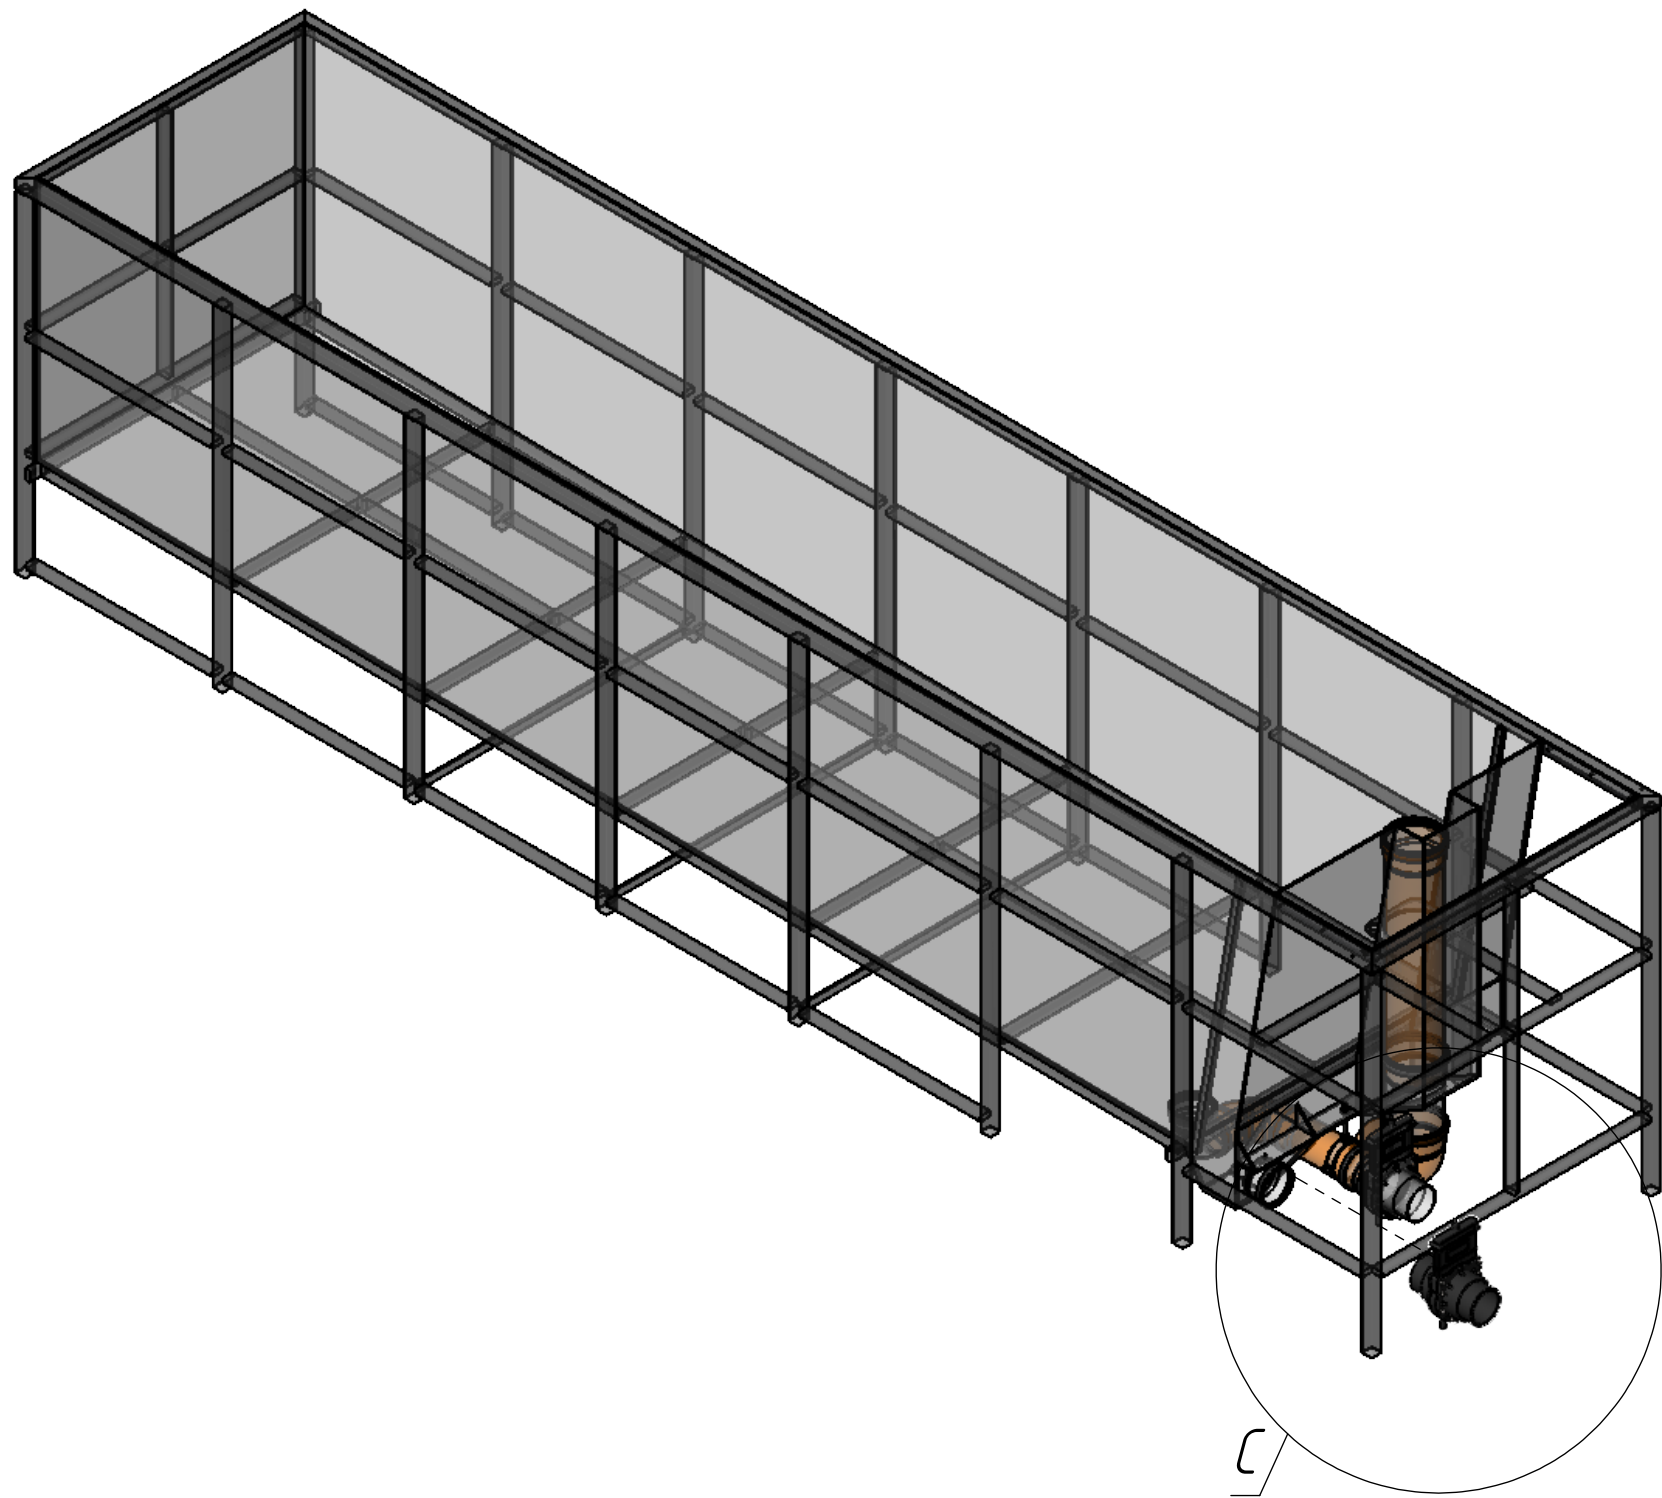



С (1 : 10)

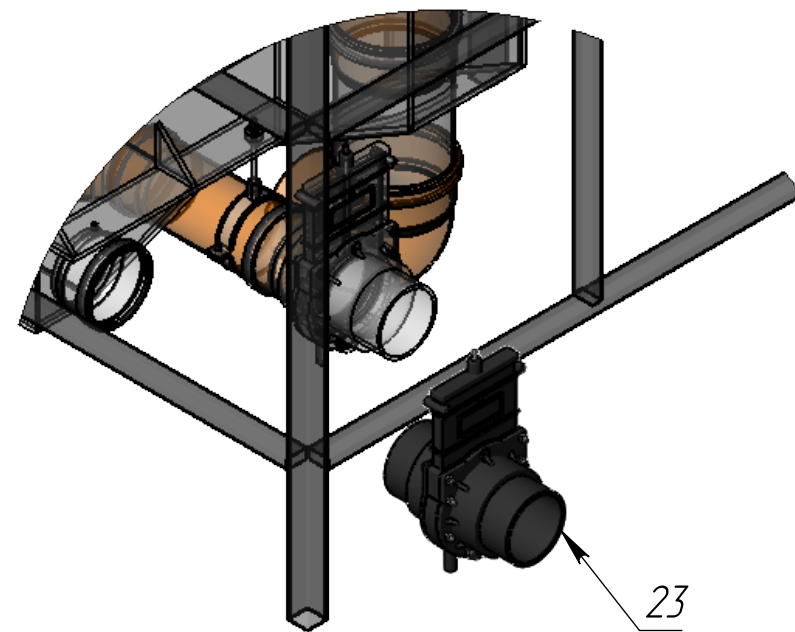

					ВРХИ.ВМ.01.32 СБ		
					Ванна (прав. стена) шаг 4		
					Лит.	Масса	Масштаб
						393.98	1:50
					Лист 5		Листов 10
					Сборочная единица		
Изм.	Лист	№ докум.	Подп.	Дата			
Разраб.							
Пров.							
Т. контр.							
Н. контр.							
Утв.							



Перв. примен.	Справ. №	Подп. и дата	Инв. № дубл.	Взам. инв. №	Подп. и дата	Инв. № подл.

ВРХИ.ВМ.01.32 СБ

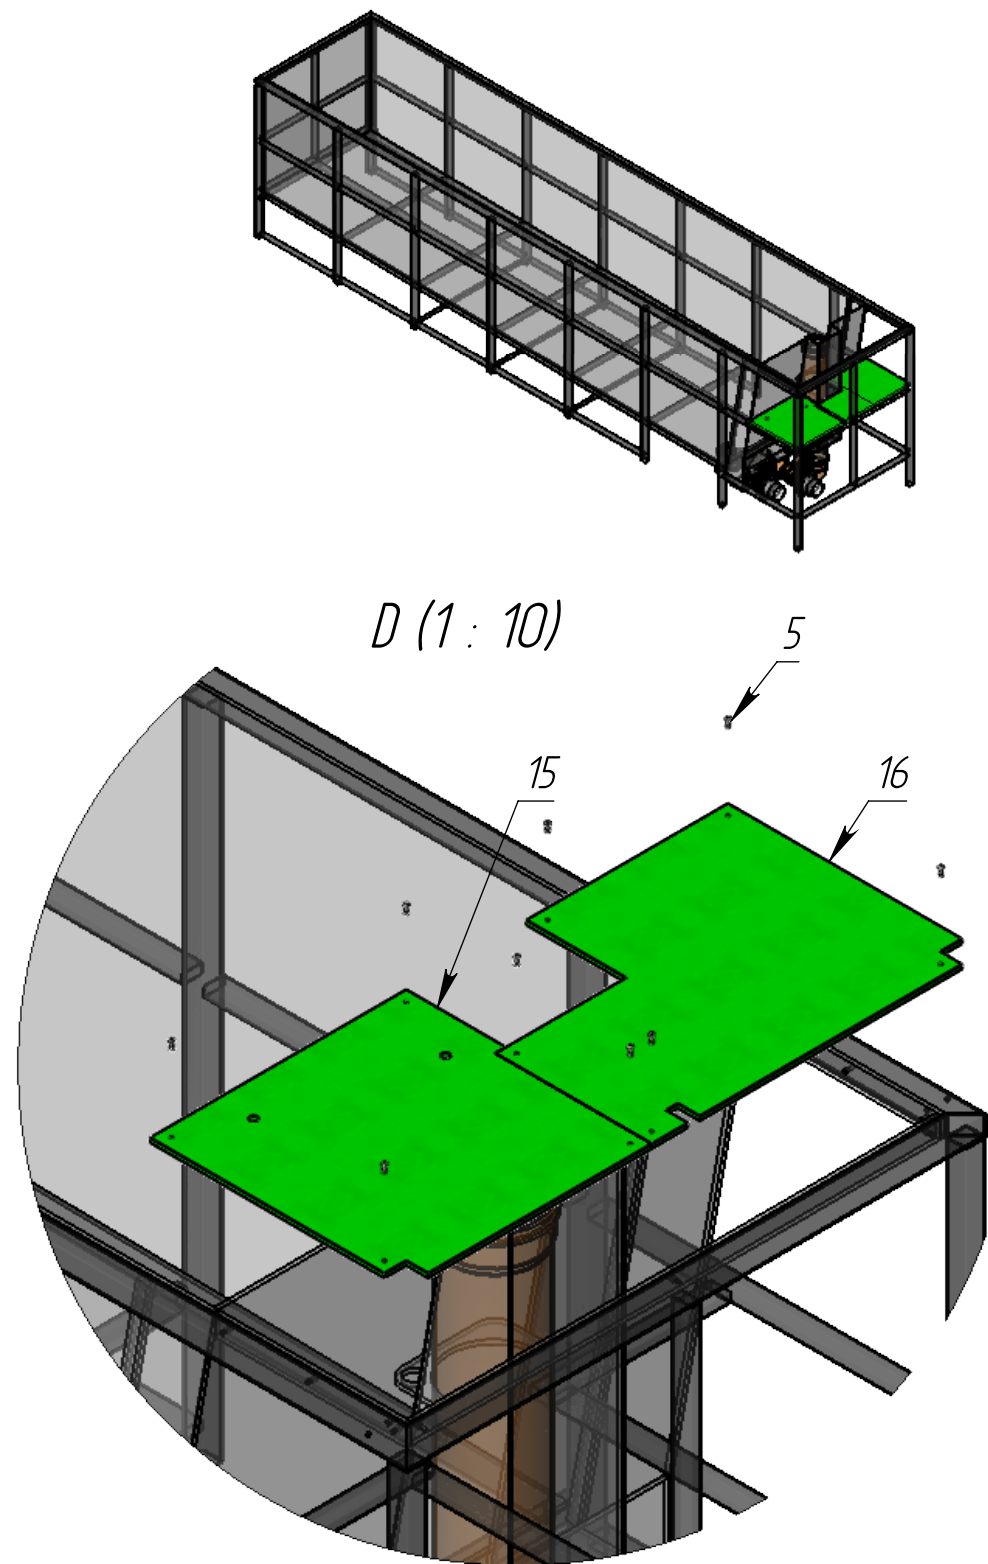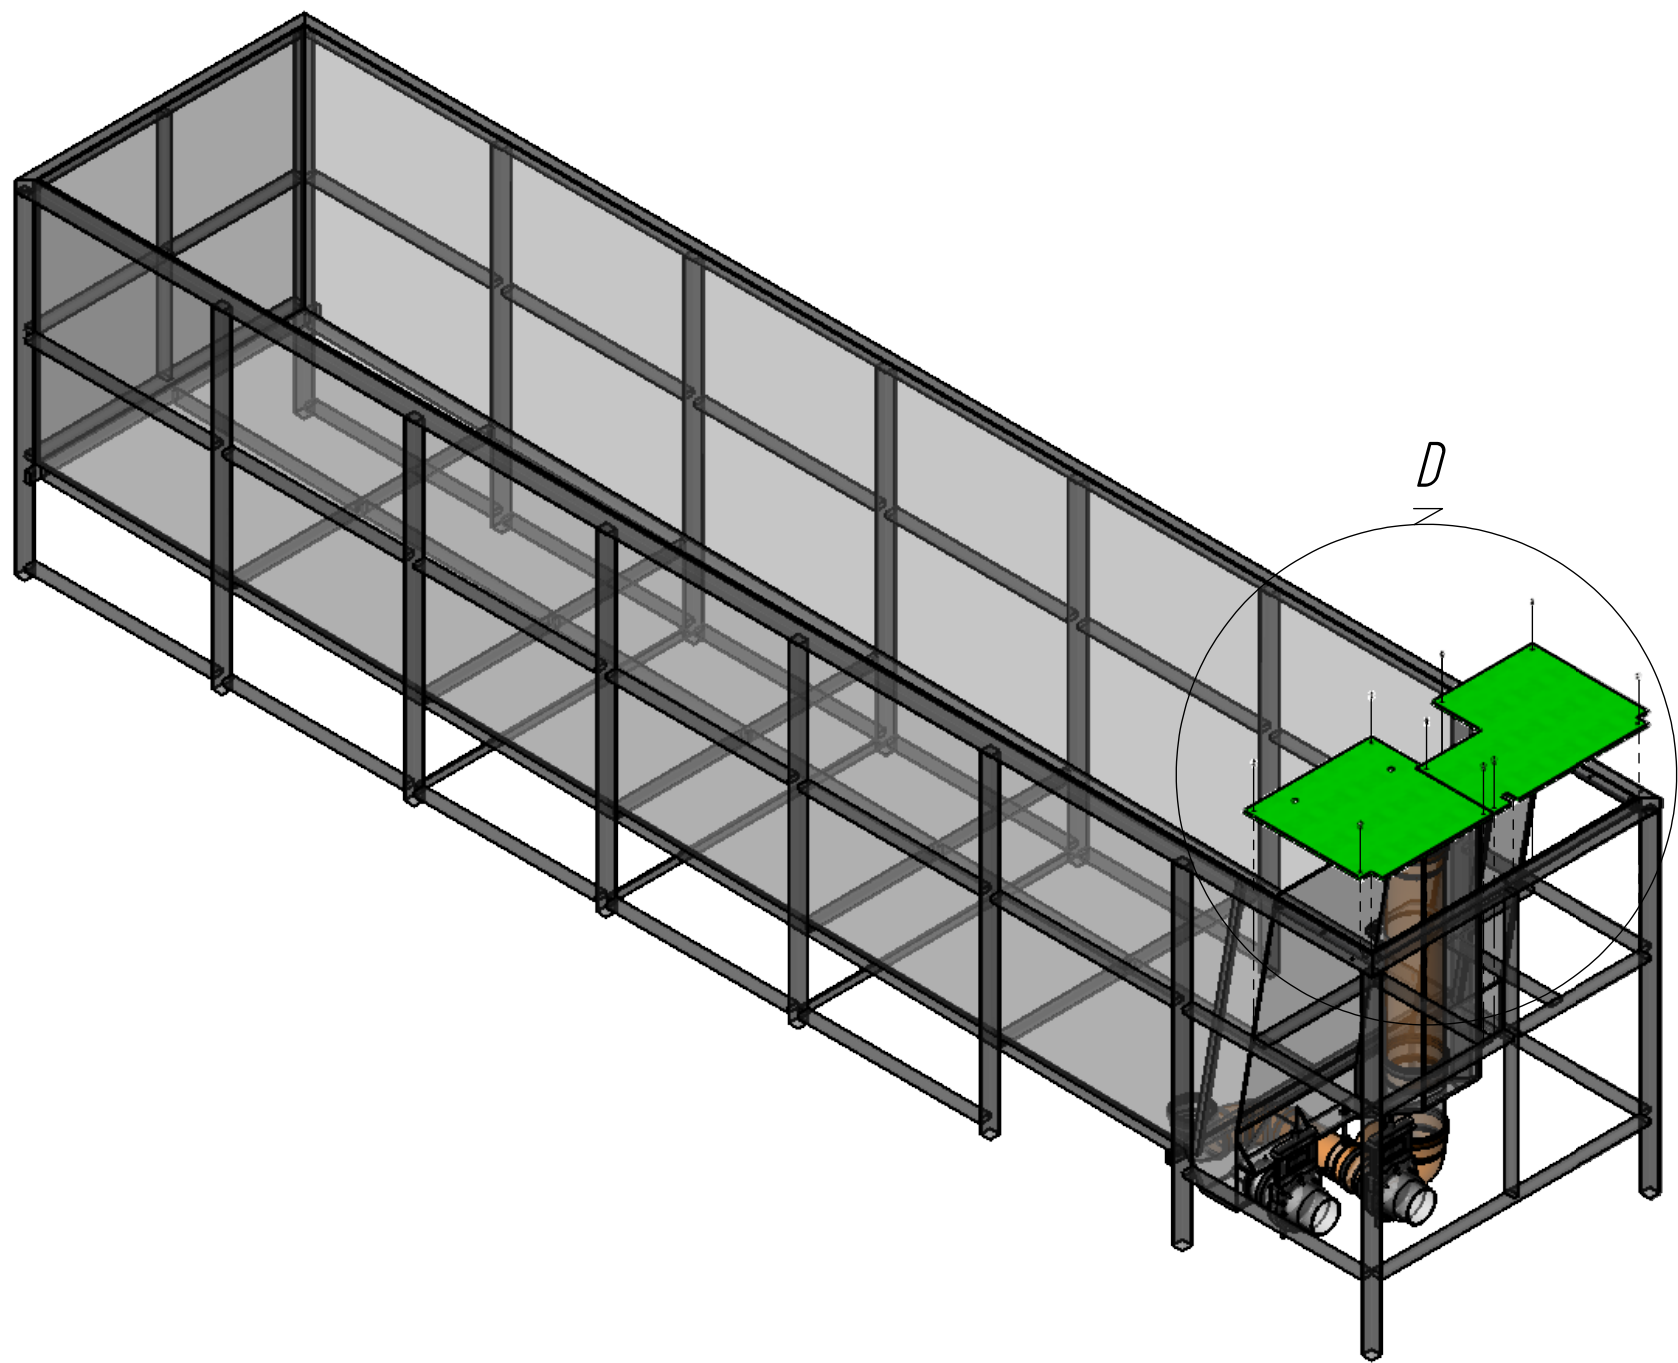

					ВРХИ.ВМ.01.32 СБ				
					Ванна (прав. стена) шаг 5	Лит.		Масса	Масштаб
Изм.	Лист	№ докум.	Подп.	Дата				393.98	1:50
Разраб.									
Пров.									
Т. контр.									
						Лист 6		Листов 10	
Н. контр.					Сборочная единица				
Утв.									


E (1 : 10)

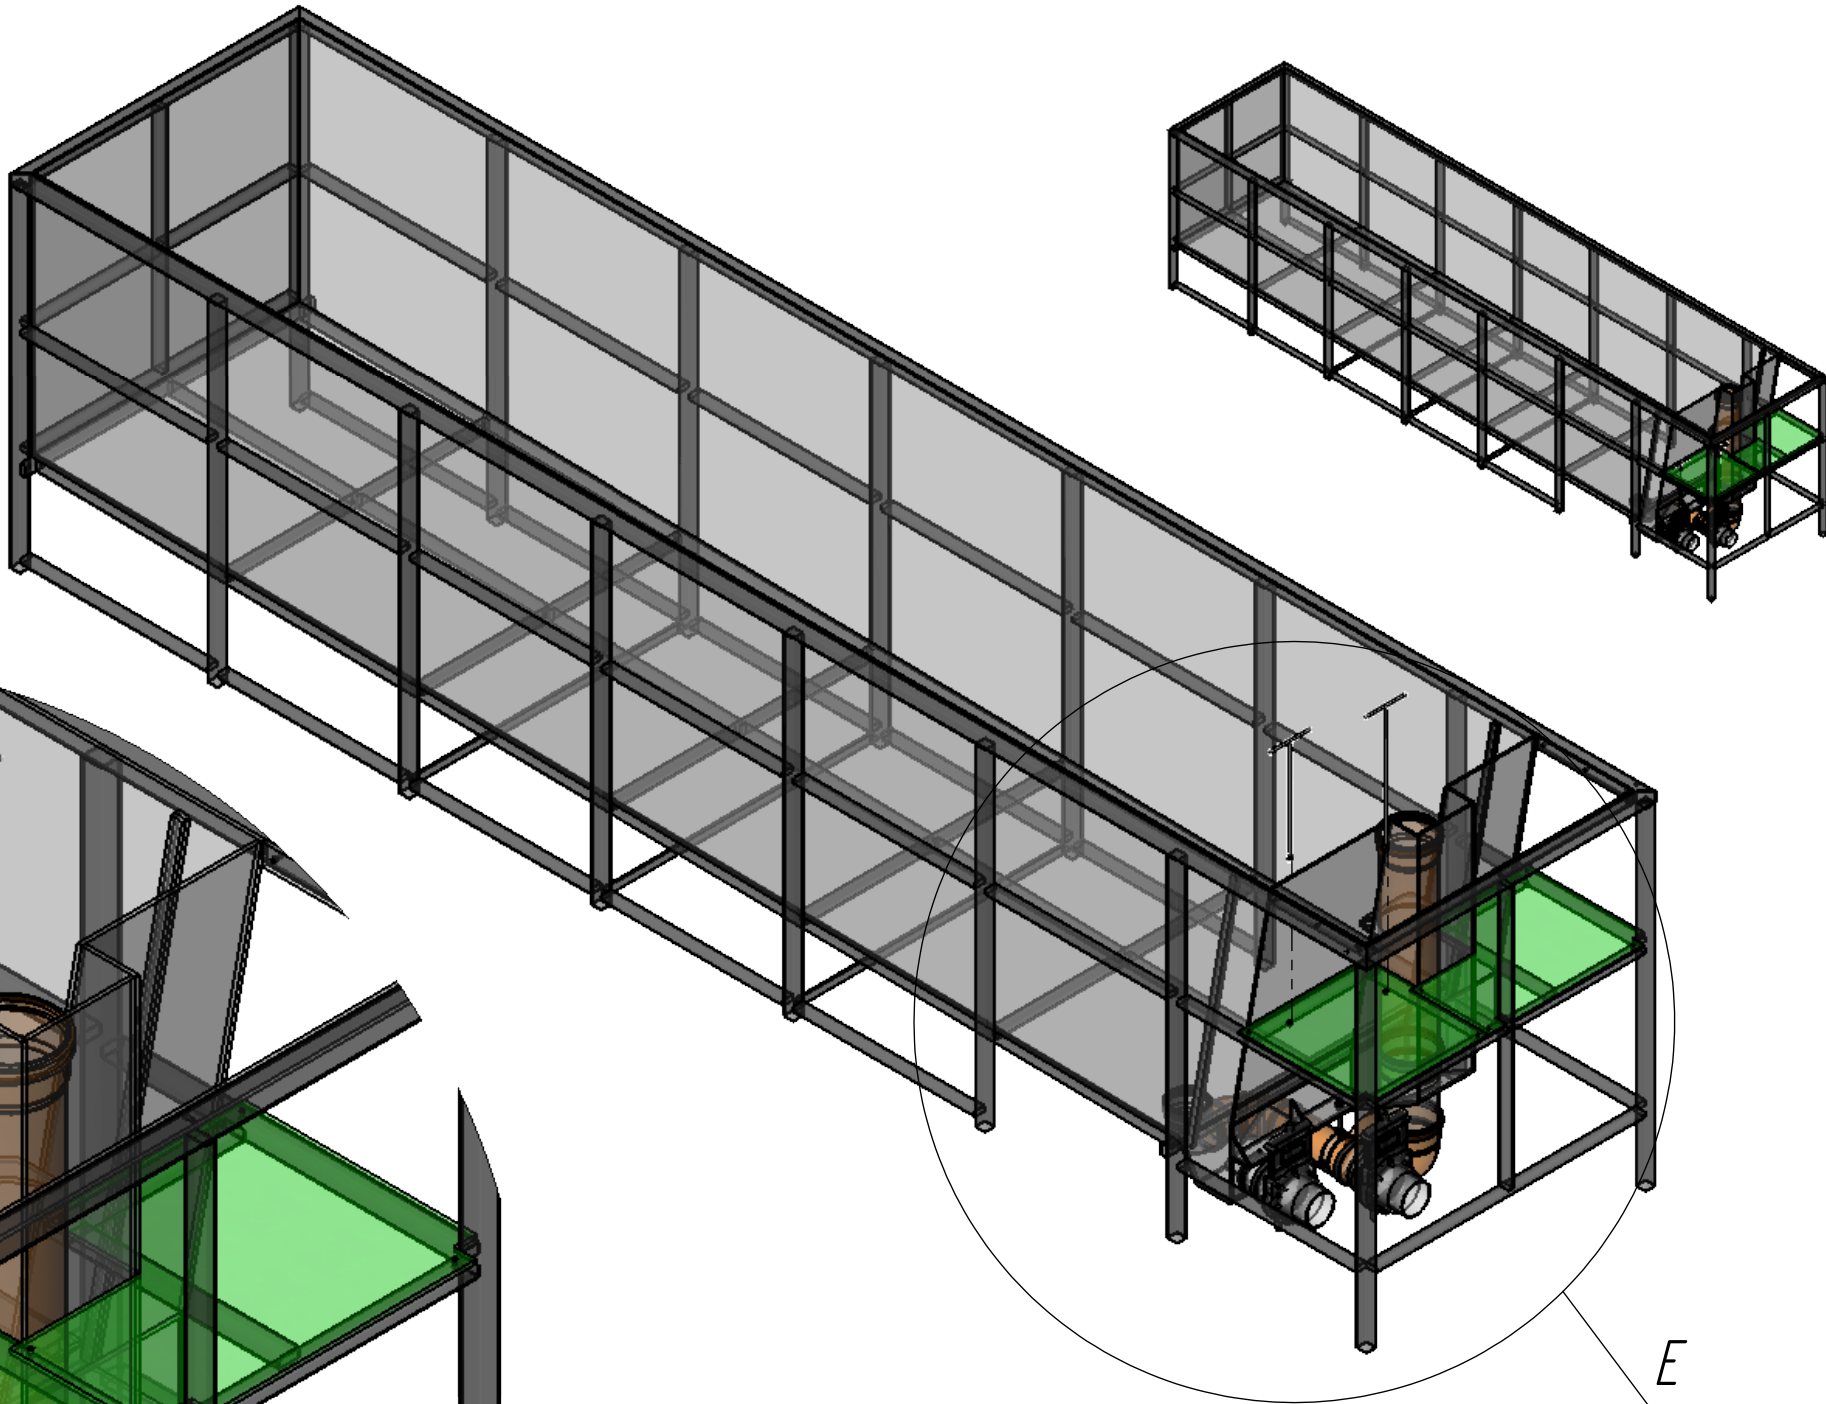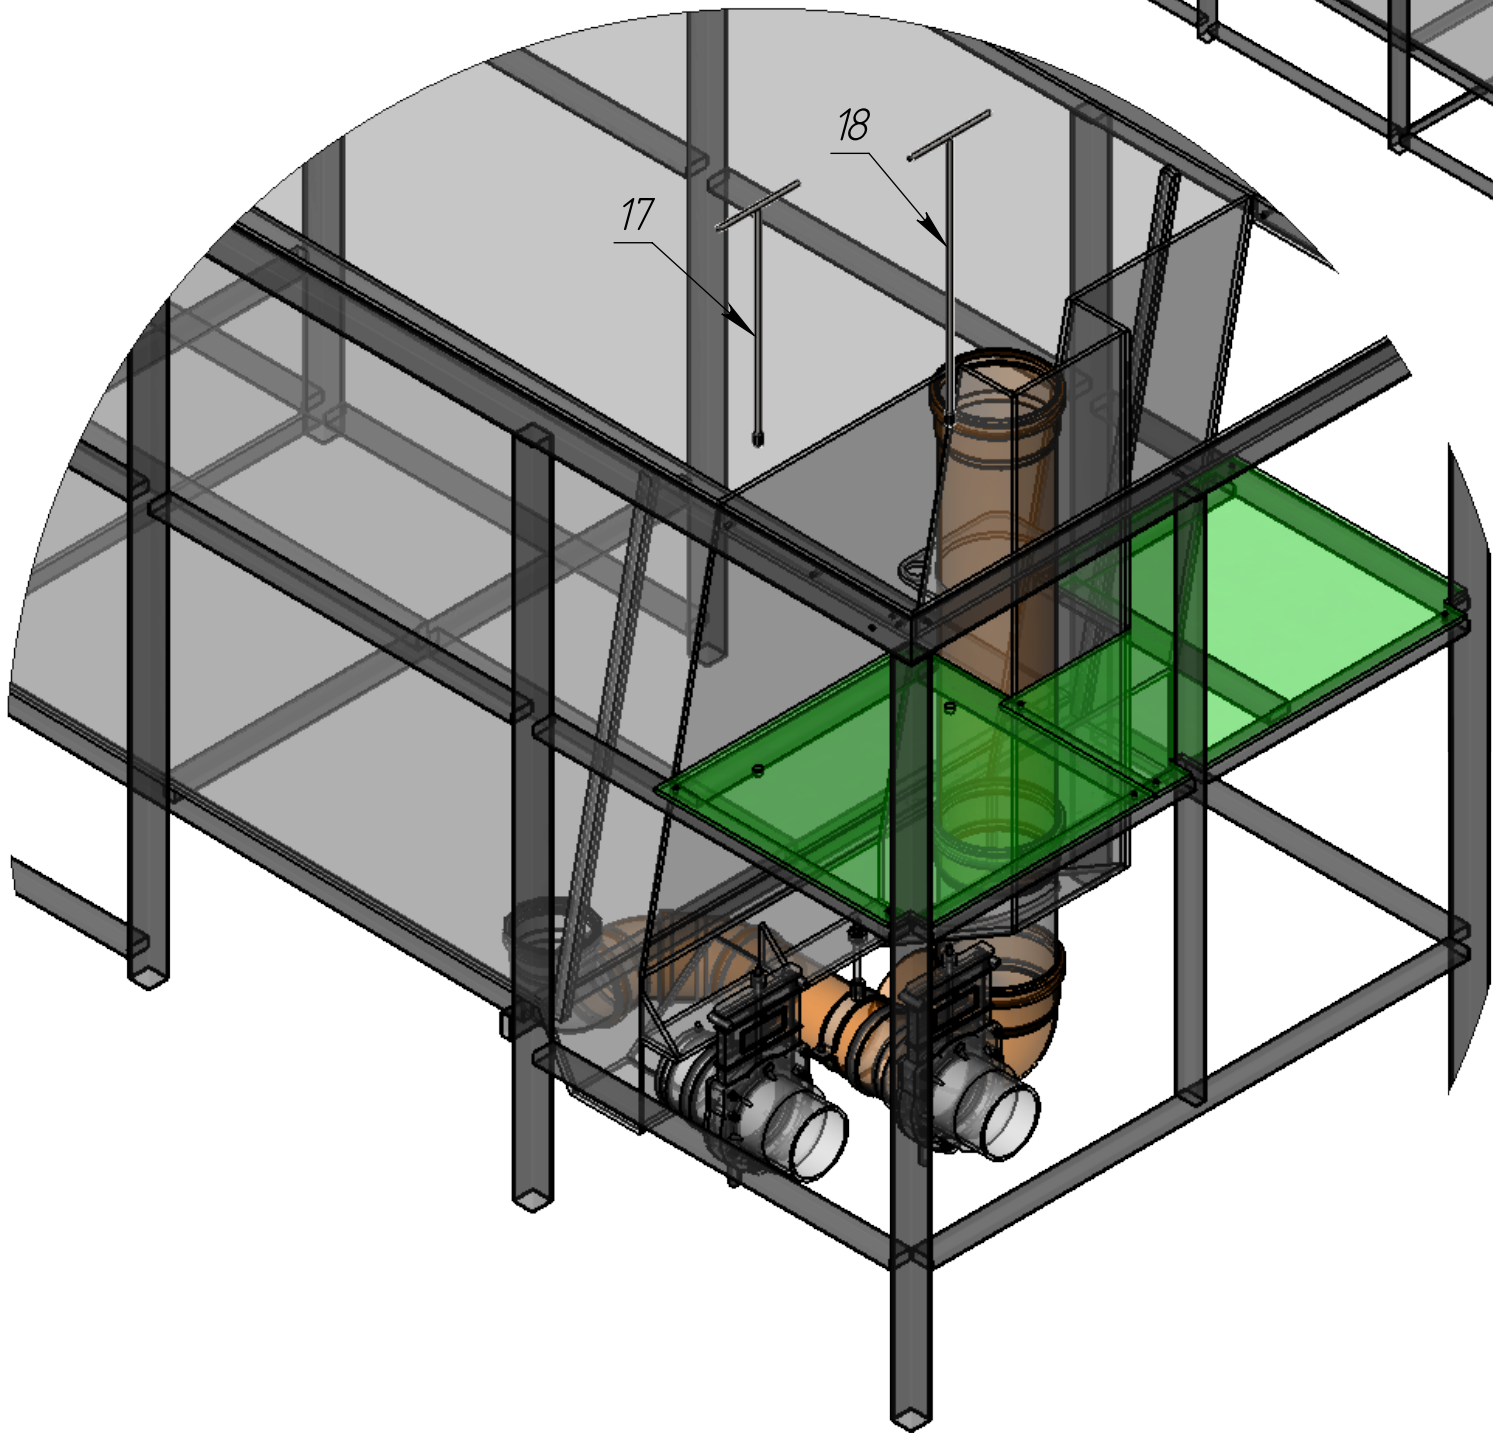



					ВРХИ.ВМ.01.32 СБ		
					Ванна (прав. стена) шаг 6		
					Лит.	Масса	Масштаб
						393.98	1:50
					Лист 7		Листов 10
					Сборочная единица		
Изм.	Лист	№ докум.	Подп.	Дата			
Разраб.							
Пров.							
Т. контр.							
Н. контр.							
Утв.							

Перв. примен.		Справ. №		Подп. и дата		Инв. № дубл.		Взам. инв. №		Подп. и дата		Инв. № подл.	

ВРХИ.ВМ.01.32 СБ

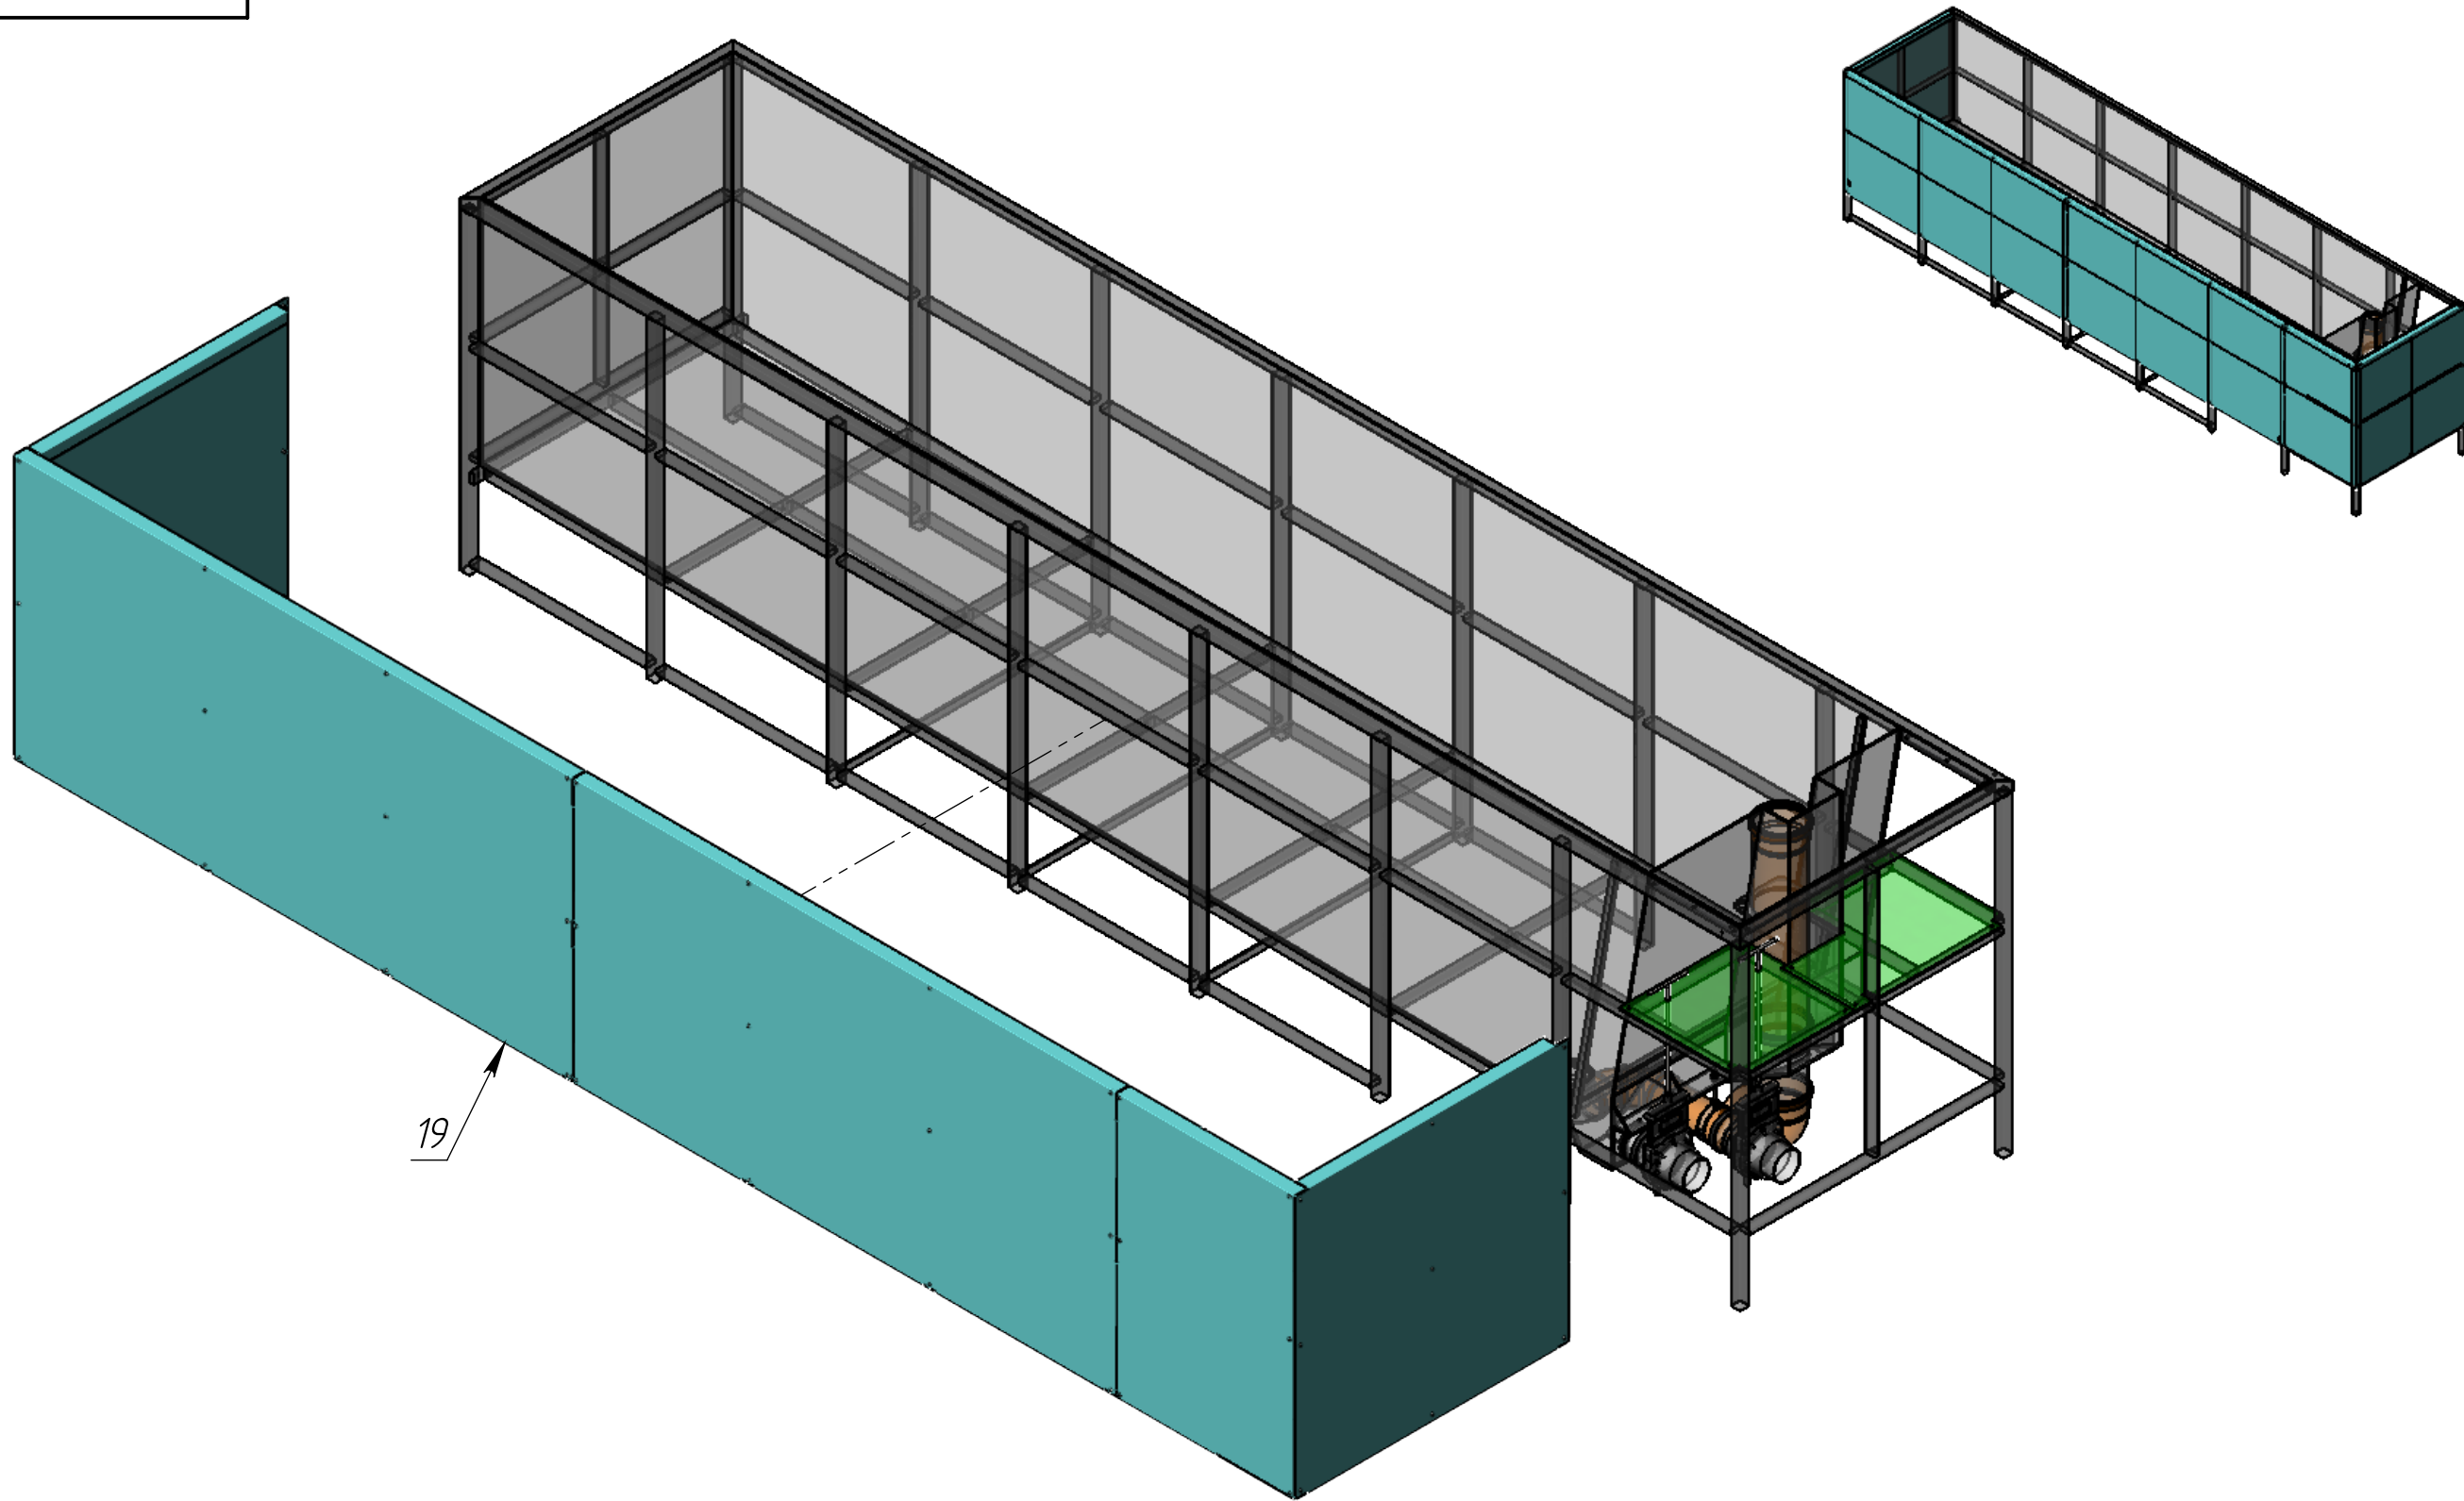

					ВРХИ.ВМ.01.32 СБ		
					Ванна (прав. стена) шаг 7		
					Лит.	Масса	Масштаб
						393.98	1:50
					Лист 8		Листов 10
					Сборочная единица		
Изм.	Лист	№ докум.	Подп.	Дата			
Разраб.							
Пров.							
Т. контр.							
Н. контр.							
Утв.							

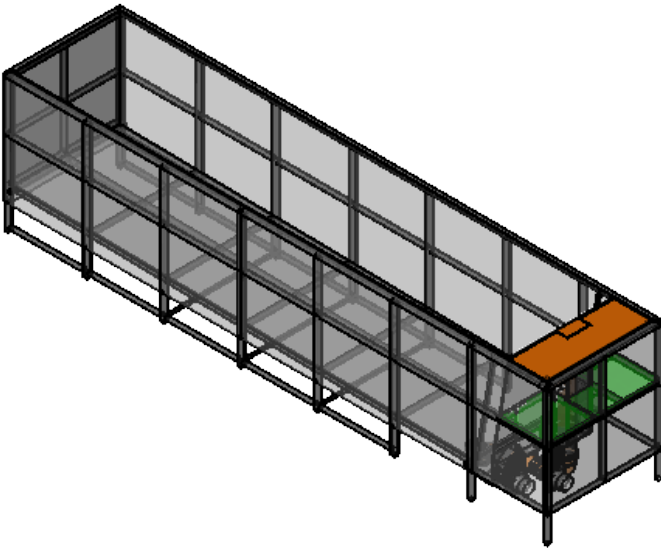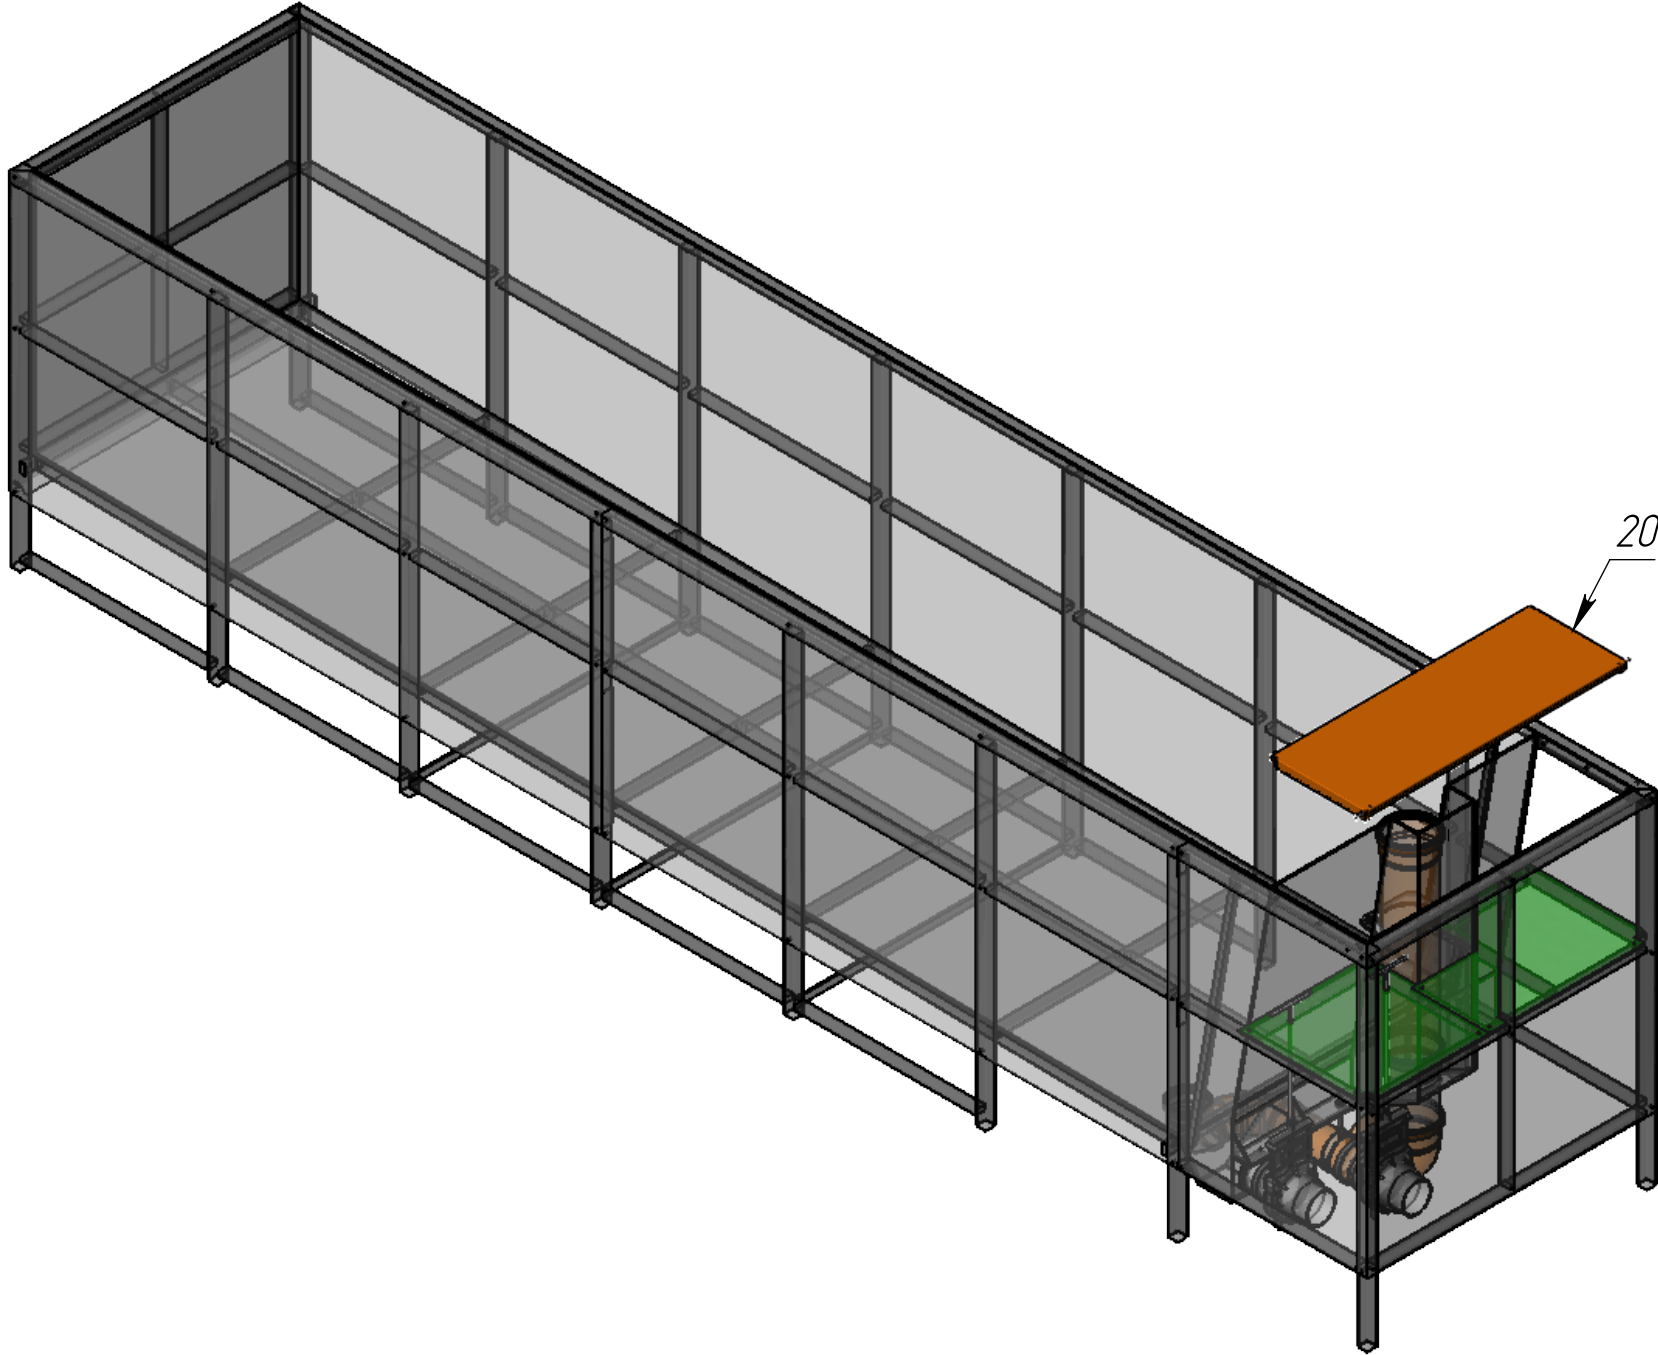


					ВРХИ.ВМ.01.32 СБ		
					Ванна (прав. стена) шаг 8		
Изм.	Лист	№ докум.	Подп.	Дата			
Разраб.						Лит.	Масса
Пров.							393.98
Т. контр.						Лист 9	Листов 10
Н. контр.					Сборочная единица		
Утв.							

Перв. примен.	Справ. №	Подп. и дата	Инв. № дубл.	Взам. инв. №	Подп. и дата	Инв. № подл.

ВРХИ.ВМ.01.32 СБ

Перв. примен.	Справ. №	Подп. и дата	Инв. № дубл.	Взам. инв. №	Подп. и дата	Инв. № подл.

ВРХИ.ВМ.01.32 СБ

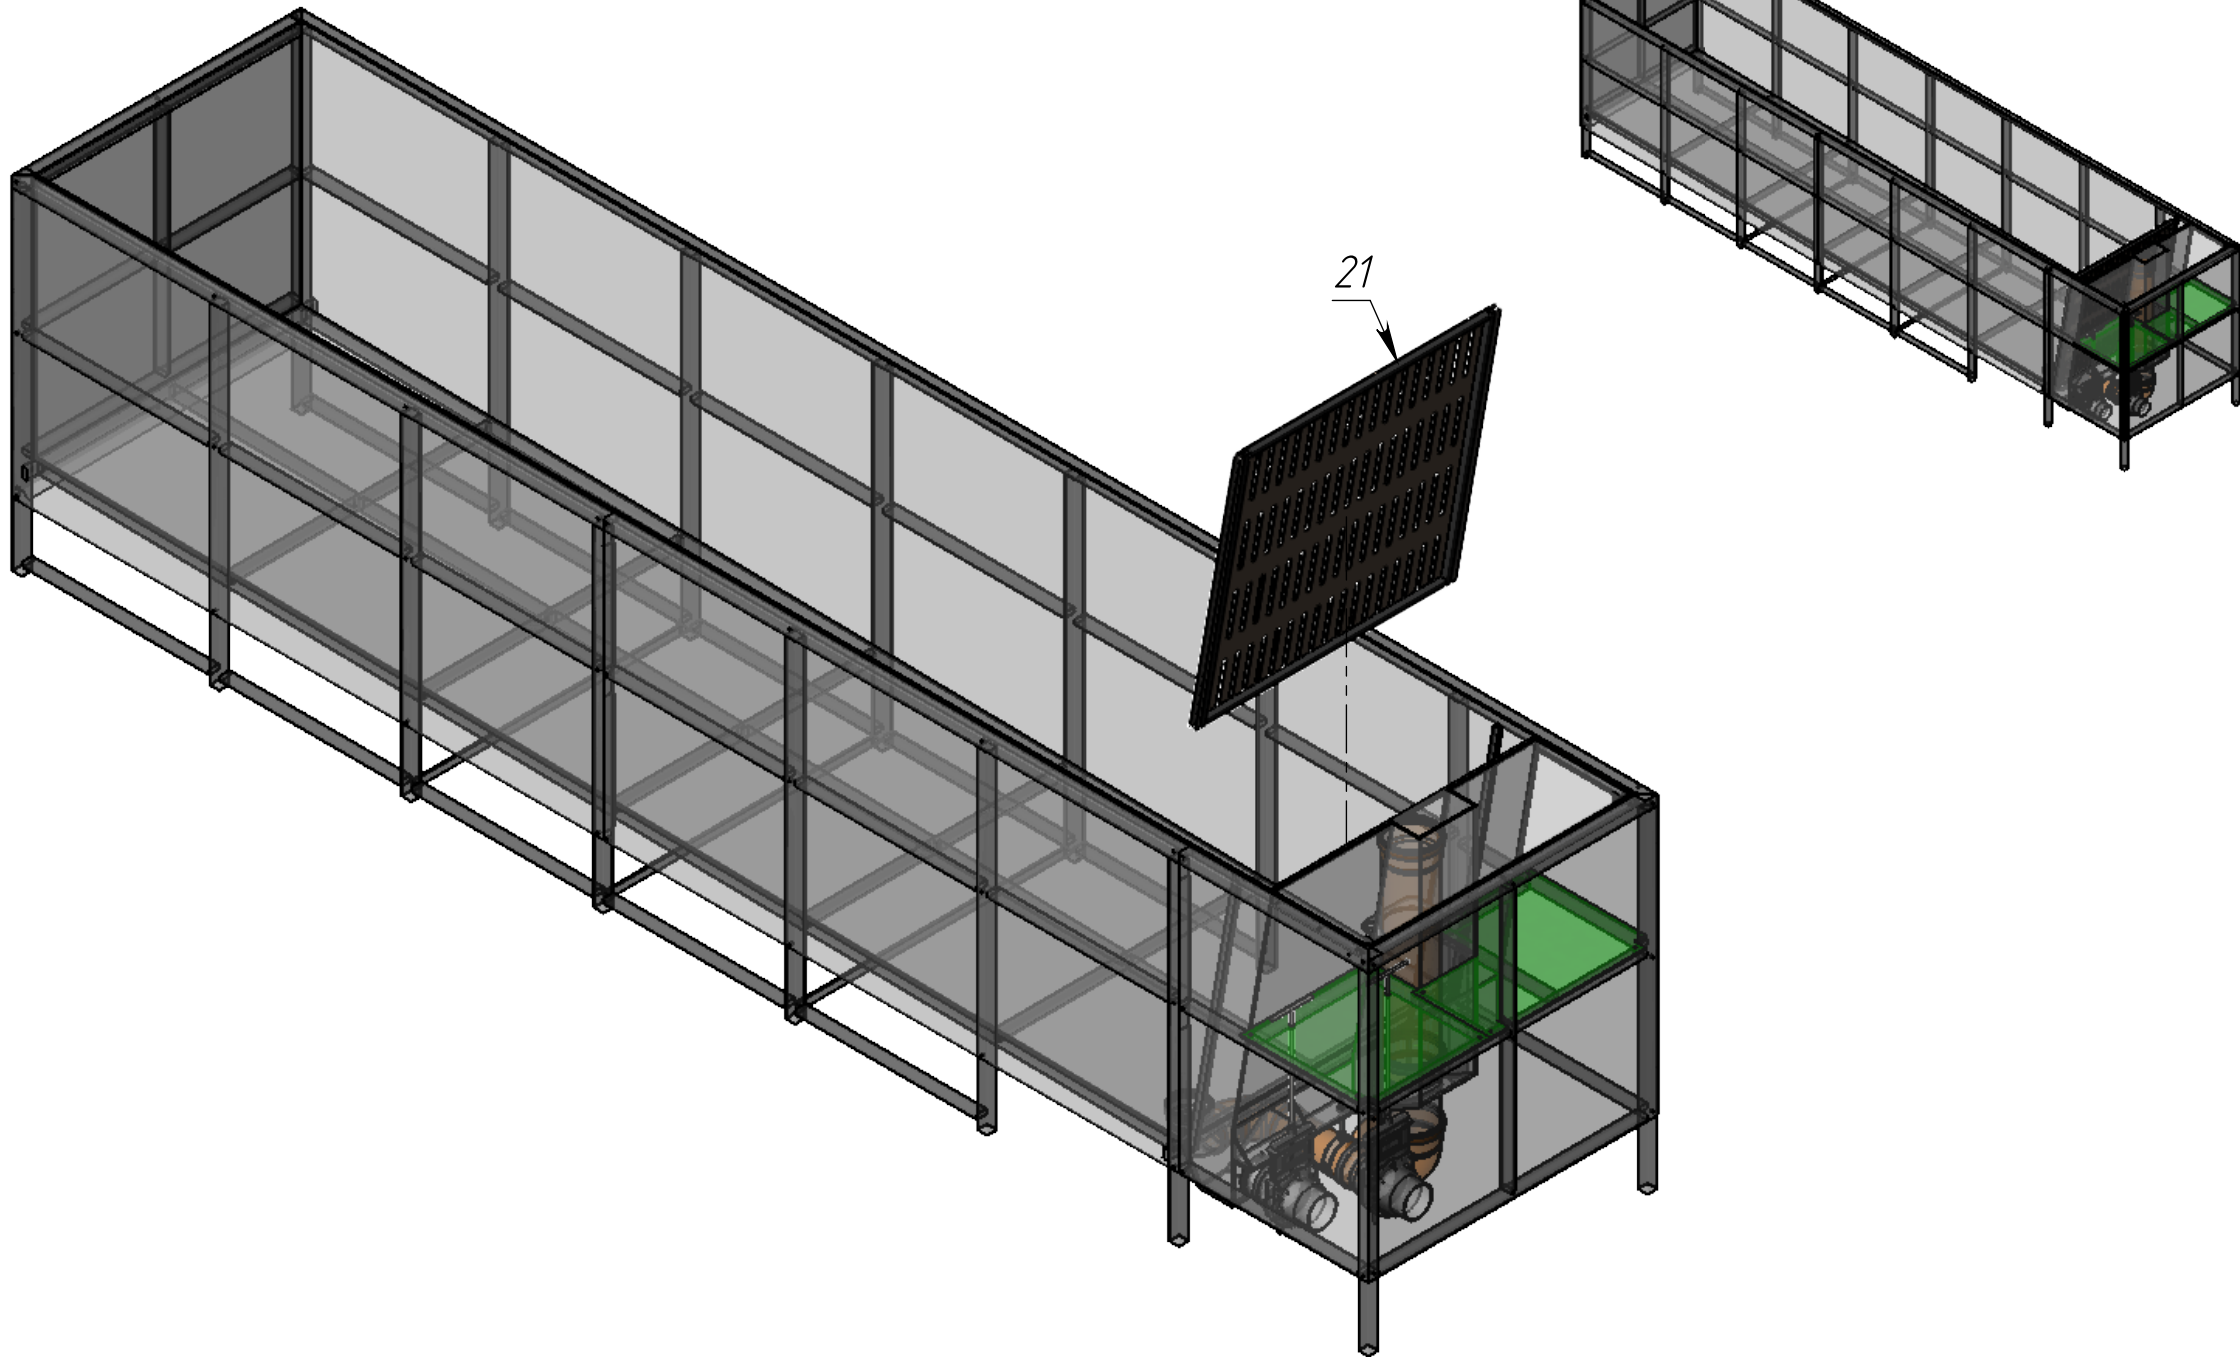

					ВРХИ.ВМ.01.32 СБ				
					Ванна (прав. стена) шаг 9	Лит.		Масса	Масштаб
Изм.	Лист	№ докум.	Подп.	Дата				393.98	1:50
Разраб.									
Пров.									
Т. контр.						Лист 10		Листов 10	
					Сборочная единица				
Н. контр.									
Утв.									

Файл: Схема (порядок сборки)